

BB Truss & Timber Pty.Ltd.

(A.B.N. 20 986 756 544)

41 Keilor Park Drive Keilor Park 3042 (PH) 9331 7075

DATE: 10/04/2026

BUILDING AUTHORITY ROOF TRUSS CERTIFICATION

PROJECT IDENTIFICATION

BSPOKE LUXURY HOMES PTY LTD

Quote Number: **K0964**

Site Address: **LOT 735 15 LEICHHARDT AVE
BURNSIDE VIC 3023 AUS**

Structure Type: **House**

This is to certify that the prefabricated timber roof trusses and pre-cut hip end members supplied to the above project were manufactured using MULTINAIL metal connectors and detailed using MULTINAIL computer truss design programs, in accordance with the National Construction Code (NCC 2022). The roof truss design and detailing assumes the supporting structure is stable within its own right before the installation of the roof trusses.

The specifications used in the design of the trusses were as follows :

ROOF SHAPE	: Standard	ROOFING	: Metal Sheet@7kg/m²
TIMBER	: Dry Softwood	TC Fixing/Restraint	: Metal @ 900c/900c
SPACING	: 900 mm	CEILING	: Plaster 10mm Supa Span@8.2kg/m
FASCIA TYPE	: As per AS1720.3-2016	BC Fixing/Restraint	: Metal direct @ 600c/600c
WIND / EXT / INT	: N2 / 0.6 / 0.2	PITCH	: 25.0 / 25.0 deg
		OVERHANG	: 550 / 550

All designed trusses and pre-cut members utilize the following codes:

AS/NZS 1170.0-2002: Structural Design Actions Part 0: General principles
AS/NZS 1170.1-2002: Structural Design Actions Part 1: Permanent, imposed and other actions
AS/NZS 1170.2-2021: Structural Design Actions Part 2: Wind actions
AS/NZS 1170.3-2003: Structural Design Actions Part 3: Snow and ice actions
AS 4055-2021: Wind loads for housing
AS 1720.1-2010: Timber structures Part 1: Design methods
AS 1720.3-2016: Timber structures Part 3: Design criteria for timber-framed residential buildings
AS 1720.5-2015: Timber structures Part 5: Nailplated timber roof trusses
AS 1649-2001: Timber-Methods of test for mechanical fasteners and connectors
AS 4100-2020: Steel Structures
AS/NZS 4600-2018: Cold-formed steel structures

All trusses must be braced and erected in accordance with AS4440, Installation of nailplated timber trusses, in conjunction with all local building authority requirements, and any other supplied details.

SIGNATURE :

NAME

POSITION

DATE

:


: Joey Meriales (TN-012-015)

: detailer

: 10/04/2026

For detailed load information, including AC, Solar, Tank and Storage loads, refer to the detailed Engineering and Submission reports and Roof Layout.

Client: BSPOKE LUXURY HOMES PTY LTD	BB Truss & Timber Pty.Ltd.	Job No: K0964
Site: LOT 735 15 LEICHHARDT AVE BURNSIDE VIC 3023 AUS	(A.B.N. 20 986 756 544) 41 Keilor Park Drive Keilor Park 3042 (PH) 9331 7075	Truss: Layout created T1
Ref:	(pt) : 1 mid panel tie(s) required to each bottom chord panel	Type: Standard
		Lamination/Quantity: 1/15

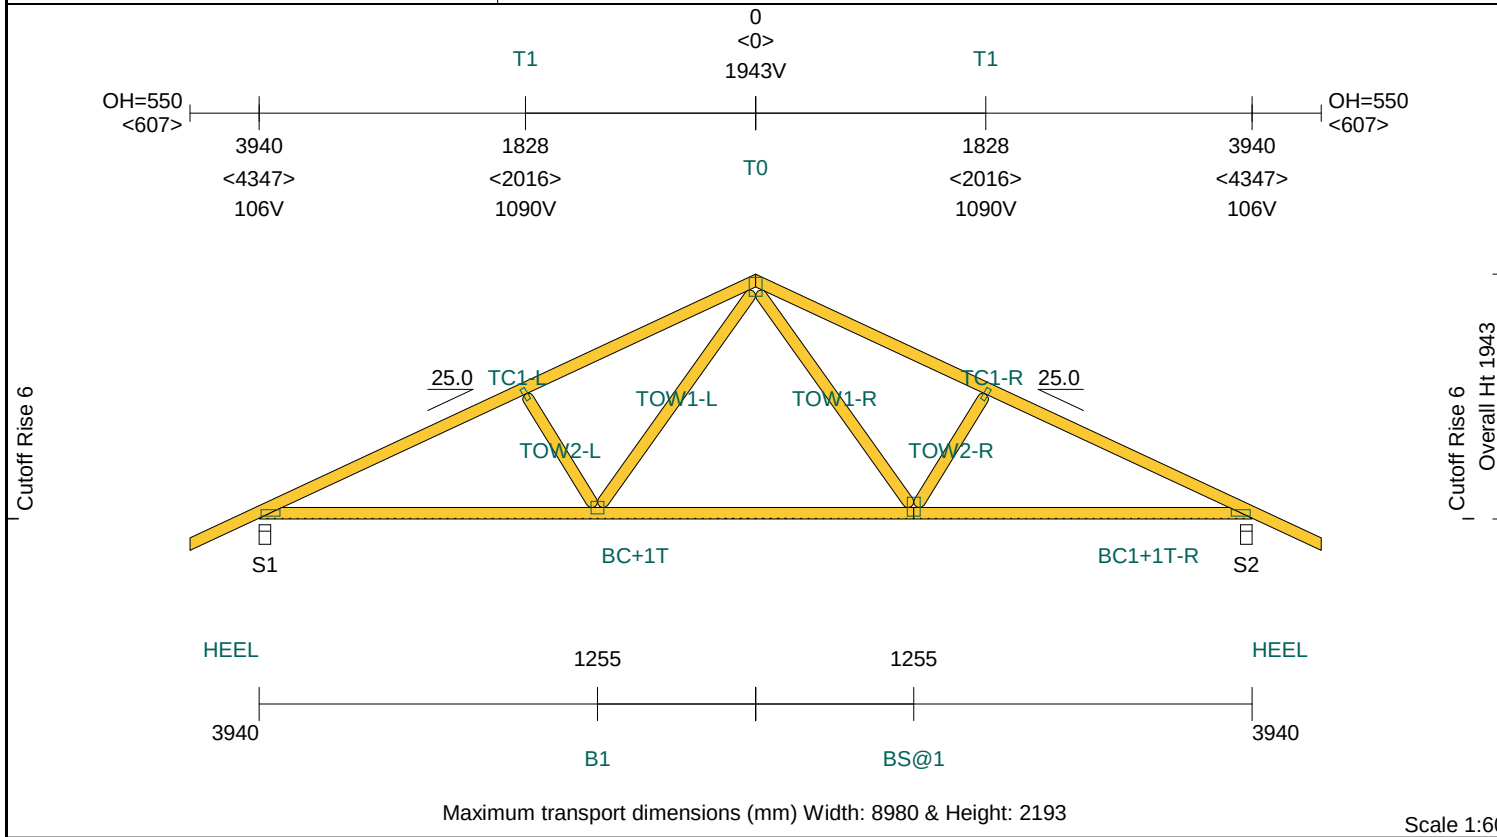

TIMBER:

Member	Size & Grade	Def	Jnt	Grp	Rest
TC1	90x35-MGP10 H0 ADS	1	JD5	900	
BC+1T	90x35-MGP10 H0 ADS	3	JD5	(pt)	
BC1+1T-R	90x35-MGP10 H0 ADS	3	JD5	(pt)	
TOW1	90x35-MGP10 H0 ADS		JD5		
TOW2	90x35-MGP10 H0 ADS		JD5		

PLATES:

Joint	Size & Grade	Camber	X	Y	Rtn
HEEL	50x150-MN		15	23	0
T0	150x100-MN		=	=	0
T1	38x100-MN		=	=	0
B1-L	100x100-MN	1	=	50	0
BS@1-R	150x100-MN	1	=	68	0

Vertical Reactions at Supports


Support	(No.)	S1	S2
1.35DL	(kN)	1.11	1.11
1.2DL + 1.5MLL	(kN)	2.51	2.51
0.9DL + 1WL	(kN)	-2.05	-2.05
Tie Down	Required	1 MGrip	1 MGrip
Bearing	Member/Support	0k/0k	0k/0k

(Note: Tie down capacity based on JD4. Bearing capacity based on timber properties of the member onto support, and SD7 for support.)

Weight of timber & plate (excl. brackets): **39.1kg**

Span: 7880	Roofing: Metal Sheet@7kg/m²	Wind / Ext / Int: N2 / 0.6 / 0.2	All dimensions in millimetres. This drawing should be read in conjunction with Multinail Technical sheets.	Version: 1.14.3
Pitch: 25.00/25.00	TC Fix/Rest: Metal @ 900c/900c	Fascia Type: As per AS1720.3-2016		User: (TN-012-015)
Overhang: 550/550	Ceiling: Plaster 10mm Supa Span@8.2kg/m²	Ground Snow Load:		Date: 10/04/2026
Spacing: 900	BC Fix/Rest: Metal direct @ 600c/600c	Structure: House		Page: 1

Client: BSPOKE LUXURY HOMES PTY LTD	BB Truss & Timber Pty.Ltd. (A.B.N. 20 986 756 544) 41 Keilor Park Drive Keilor Park 3042 (PH) 9331 7075	Job No: K0964
Site: LOT 735 15 LEICHHARDT AVE BURNSIDE VIC 3023 AUS		Truss: Layout created T2
Ref:		Type: TG2190 Lamination/Quantity: 1/1

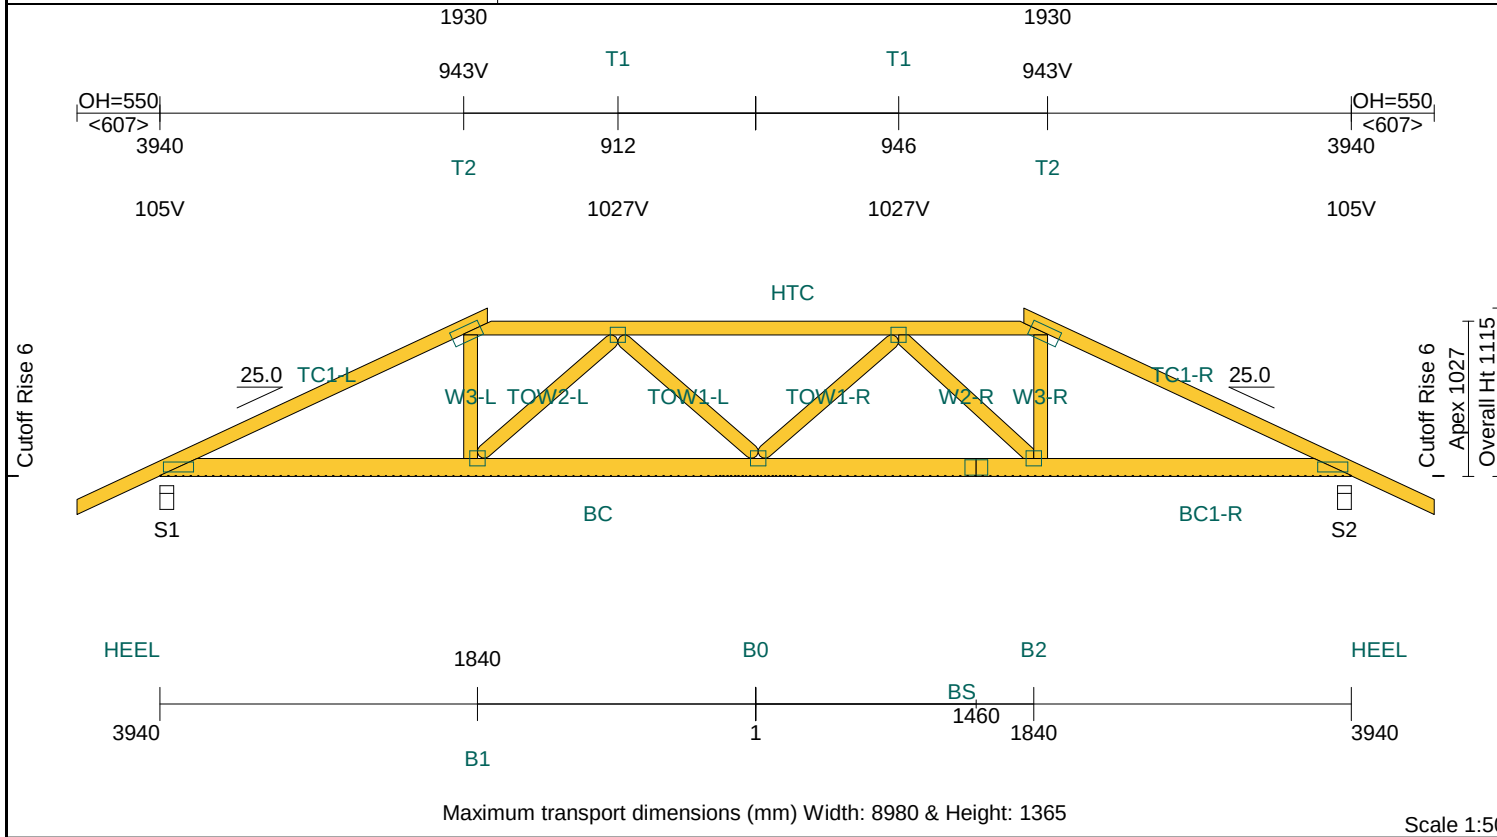

TIMBER:

Member	Size & Grade	Def	Jnt	Grp	Rest
TC1	90x35-MGP10 H0 ADS	1	JD5		900
BC	120x35-MGP10 H0 ADS	1	JD5		600
BC1-R	120x35-MGP10 H0 ADS	1	JD5		600
HTC	90x35-MGP10 H0 ADS	2	JD5		900
W2-R	90x35-MGP10 H0 ADS		JD5		
W3	90x35-MGP10 H0 ADS		JD5		
TOW1	90x35-MGP10 H0 ADS		JD5		
TOW2-L	90x35-MGP10 H0 ADS		JD5		

PLATES:

Joint	Size & Grade	Camber	X	Y	Rtn
HEEL	64x200-MN		22	31	0
T1	100x100-MN		50	50	0
T2	100x200-MN		118	45	25
B0	100x100-MN	3	=	50	0
B1-L	100x100-MN	3	=	50	0
B2-R	100x100-MN	3	=	50	0
BS	100x150-MN		=	50	0

Vertical Reactions at Supports

Support	(No.)	S1	S2
1.35DL	(kN)	2.02	2.02
1.2DL + 1.5MLL	(kN)	4.61	4.61
0.9DL + 1WL	(kN)	-3.72	-3.72
Tie Down	Required	2 MGrps	2 MGrps
Bearing	Member/Support	0k/0k	0k/0k

(Note: Tie down capacity based on JD4. Bearing capacity based on timber properties of the member onto support, and SD7 for support.)

Weight of timber & plate (excl. brackets): **44.4kg**


Span: 7880	Roofing: Metal Sheet@7kg/m²	Wind / Ext / Int: N2 / 0.6 / 0.2
Pitch: 25.00/25.00	TC Fix/Rest: Metal @ 900c/900c	Fascia Type: As per AS1720.3-2016
Overhang: 550/550	Ceiling: Plaster 10mm Supa Span@8.2kg/m²	Ground Snow Load:
Spacing: 900	BC Fix/Rest: Metal direct @ 600c/600c	Structure: House

All dimensions in millimetres. This drawing should be read in conjunction with Multinail Technical sheets.



Version: 1.14.3
User: (TN-012-015)
Date: 10/04/2026
Page: 2

Client: BSPOKE LUXURY HOMES PTY LTD	BB Truss & Timber Pty.Ltd. (A.B.N. 20 986 756 544) 41 Keilor Park Drive Keilor Park 3042 (PH) 9331 7075	Job No: K0964
Site: LOT 735 15 LEICHHARDT AVE BURNSIDE VIC 3023 AUS		Truss: Layout created T2
Ref:		Type: TG2190 Lamination/Quantity: 1/1

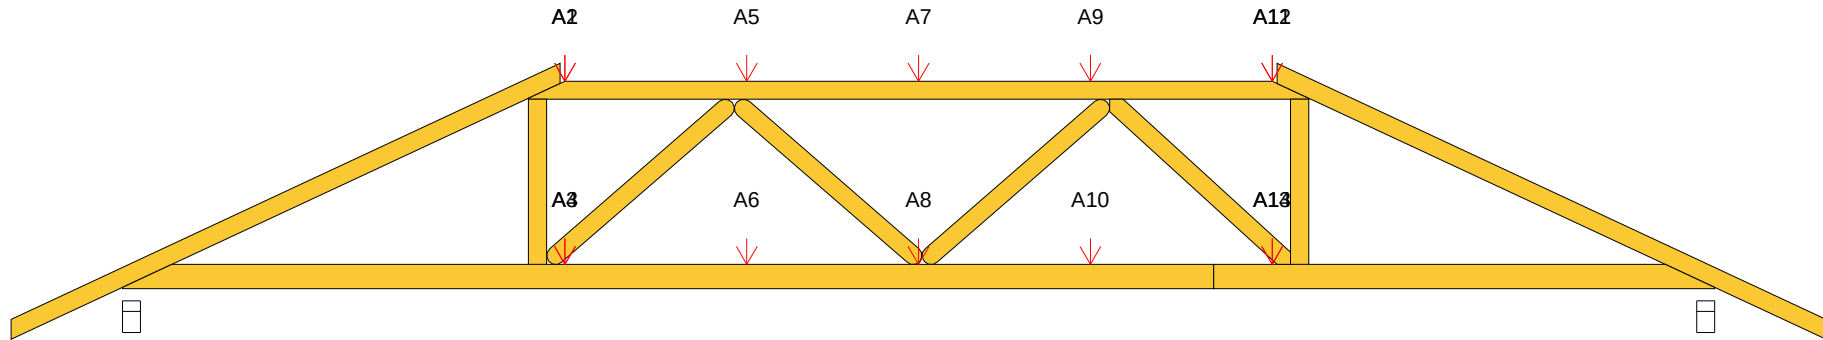


LOADS ON TRUSS: A=Auto loads by system; S=Service loads; Uc=User defined concentrated loads; Ud=User defined distributed loads
Note: -ve signed loads act downwards, +ve signed loads act upwards

Indicator	A1(kN)	A2(kN)	A3(kN)	A4(kN)	A5(kN)	A6(kN)	A7(kN)	A8(kN)	A9(kN)	A10(kN)
DL	-0.218	-0.052	0.016	-0.071	-0.071	-0.071	-0.301	-0.071	-0.071	-0.071
LL	-0.283	-0.135	0.007	-0.013	-0.162	-0.008	-0.424	-0.022	-0.162	-0.008
WL	0.753	0.294	-0.027	0.103	0.386	0.072	1.008	0.192	0.386	0.072
Desc	H1	J1	H1	J1	J2	J2	J3	J3	J2	J2

Indicator	A11(kN)	A12(kN)	A13(kN)	A14(kN)
DL	-0.218	-0.052	0.016	-0.071
LL	-0.283	-0.135	0.007	-0.013
WL	0.753	0.294	-0.027	0.103
Desc	H1	J1	H1	J1

Client: BSPOKE LUXURY HOMES PTY LTD	BB Truss & Timber Pty.Ltd. (A.B.N. 20 986 756 544) 41 Keilor Park Drive Keilor Park 3042 (PH) 9331 7075	Job No: K0964
Site: LOT 735 15 LEICHHARDT AVE BURNSIDE VIC 3023 AUS		Truss: Layout created T3
Ref:		Type: TS3090 Lamination/Quantity: 1/2

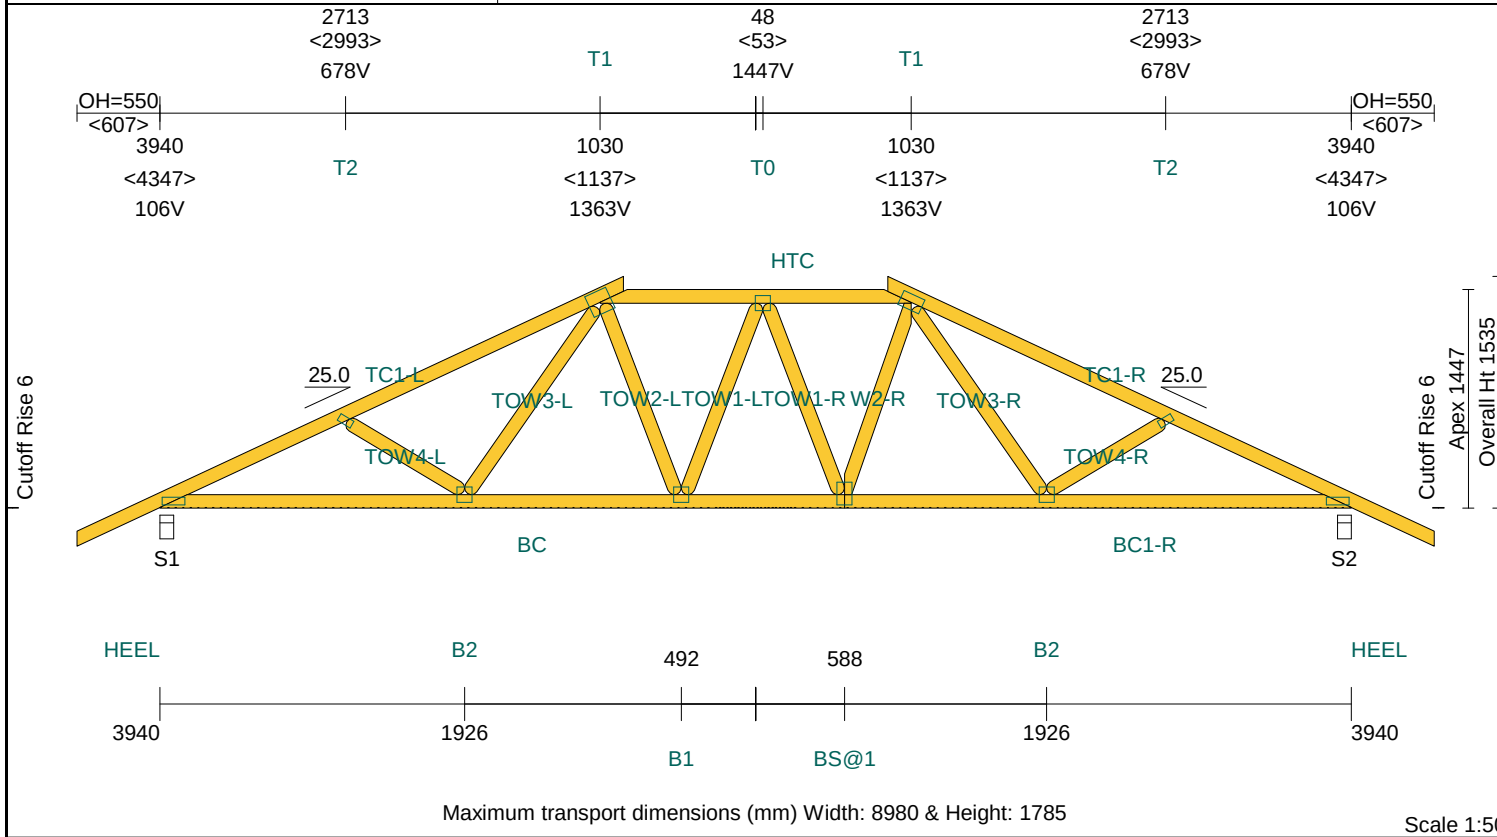

TIMBER:

Member	Size & Grade	Def	Jnt	Grp	Rest
TC1	90x35-MGP10 H0 ADS	1	JD5		900
BC	90x35-MGP10 H0 ADS	1	JD5		600
BC1-R	90x35-MGP10 H0 ADS	1	JD5		600
HTC	90x35-MGP10 H0 ADS		JD5		900
W2-R	90x35-MGP10 H0 ADS		JD5		
TOW1	90x35-MGP10 H0 ADS		JD5		
TOW2-L	90x35-MGP10 H0 ADS		JD5		
TOW3	90x35-MGP10 H0 ADS		JD5		
TOW4	90x35-MGP10 H0 ADS		JD5		

PLATES:

Joint	Size & Grade	Camber	X	Y	Rtn
HEEL	50x150-MN		15	23	0
T0	100x100-MN		50	50	0
T1-L	150x150-MN		=	75	25
T1-R	100x150-MN		=	50	25
T2	50x100-MN		=	=	0
B1-L	100x100-MN	2	=	50	0
B2	100x100-MN	1	=	50	0
BS@1-R	150x100-MN	2	=	68	0

Vertical Reactions at Supports


Support	(No.)	S1	S2
1.35DL	(kN)	1.15	1.15
1.2DL + 1.5MLL	(kN)	2.58	2.58
0.9DL + 1WL	(kN)	-2.07	-2.07
Tie Down	Required	1 MGrip	1 MGrip
Bearing	Member/Support	Ok/Ok	Ok/Ok

(Note: Tie down capacity based on JD4. Bearing capacity based on timber properties of the member onto support, and SD7 for support.)

Weight of timber & plate (excl. brackets): **46.3kg**

Span: 7880	Roofing: Metal Sheet@7kg/m²	Wind / Ext / Int: N2 / 0.6 / 0.2	All dimensions in millimetres. This drawing should be read in conjunction with Multinail Technical sheets.	Version: 1.14.3
Pitch: 25.00/25.00	TC Fix/Rest: Metal @ 900c/900c	Fascia Type: As per AS1720.3-2016		User: (TN-012-015)
Overhang: 550/550	Ceiling: Plaster 10mm Supa Span@8.2kg/m²	Ground Snow Load:		Date: 10/04/2026
Spacing: 900	BC Fix/Rest: Metal direct @ 600c/600c	Structure: House		Page: 4

Client: BSPOKE LUXURY HOMES PTY LTD	BB Truss & Timber Pty.Ltd. (A.B.N. 20 986 756 544) 41 Keilor Park Drive Keilor Park 3042 (PH) 9331 7075	Job No: K0964
Site: LOT 735 15 LEICHHARDT AVE BURNSIDE VIC 3023 AUS		Truss: Layout created H1
Ref:		Type: Hip Truss Lamination/Quantity: 1/4

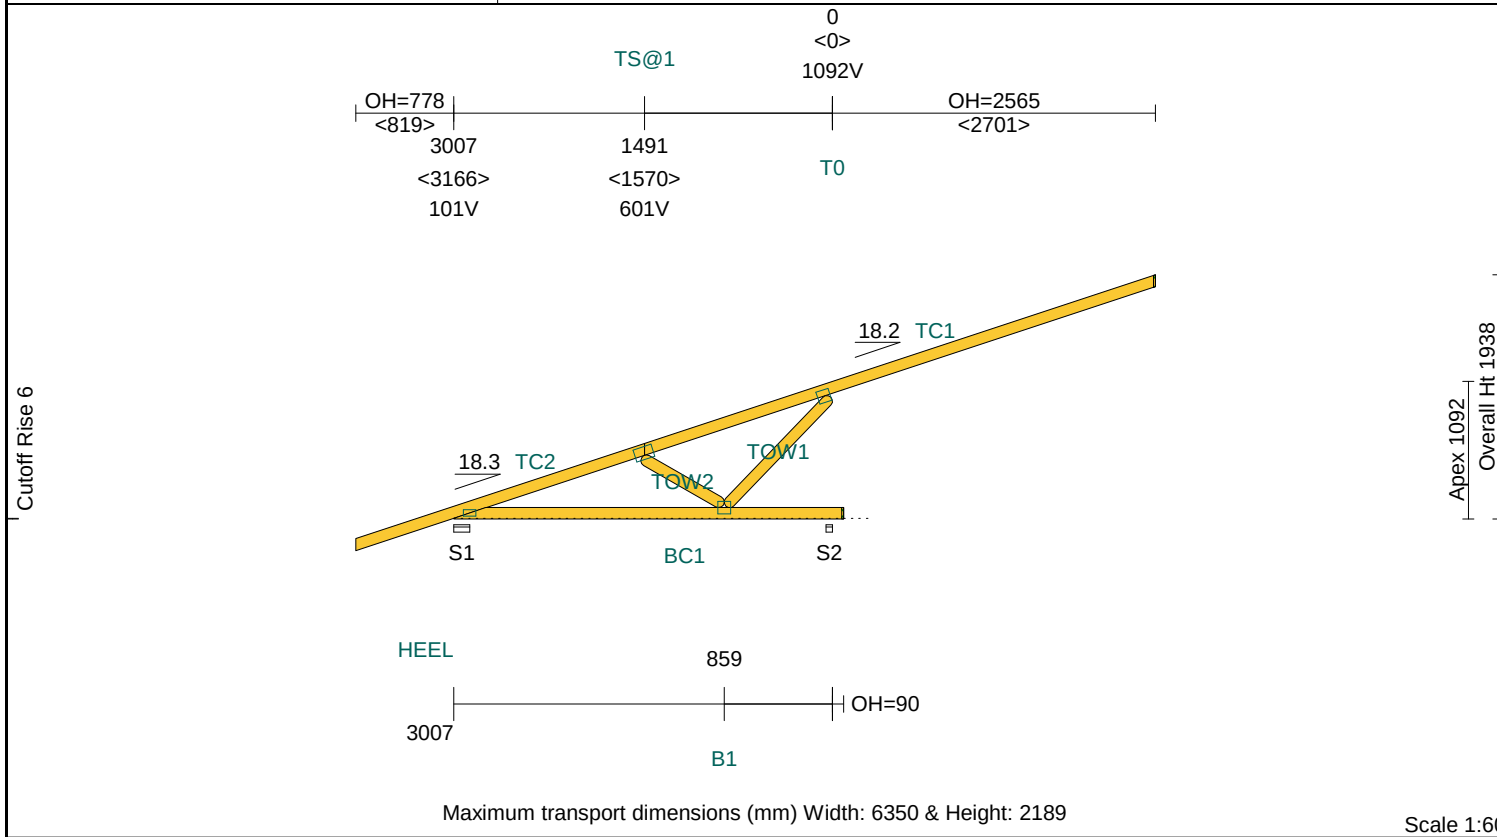

TIMBER:

Member	Size & Grade	Def	Jnt	Grp	Rest
TC1	90x35-MGP12 H0 ADS		JD4		900
TC2	90x35-MGP12 H0 ADS	1	JD4		900
BC1	90x35-MGP10 H0 ADS	1	JD5		600
TOW1	90x35-MGP10 H0 ADS		JD5		
TOW2	90x35-MGP10 H0 ADS		JD5		

PLATES:

Joint	Size & Grade	Camber	X	Y	Rtn
HEEL	50x100-MN		77	23	0
T0	100x100-MN		-22	=	0
B1	100x100-MN	1	=	50	0
TS@1	100x150-MN		=	68	0

Vertical Reactions at Supports


Support	(No.)	S1	S2
1.35DL	(kN)	0.16	0.37
1.2DL + 1.5MLL	(kN)	0.32	0.79
0.9DL + 1WL	(kN)	-0.13	-0.62
Tie Down	Required	1 M Grip	1 M Grip
Bearing	Member/Support	0k/0k	0k/0k

(Note: Tie down capacity based on JD4. Bearing capacity based on timber properties of the member onto support, and SD7 for support.)

Weight of timber & plate (excl. brackets): **20.1kg**

Span: 3007	Roofing: Metal Sheet@7kg/m²	Wind / Ext / Int: N2 / 0.6 / 0.2	All dimensions in millimetres. This drawing should be read in conjunction with Multinail Technical sheets.	Version: 1.14.3
Pitch: 18.25	TC Fix/Rest: Metal @ 900c/900c	Fascia Type: As per AS1720.3-2016		User: (TN-012-015)
Overhang: 778/2565	Ceiling: Plaster 10mm Supa Span@8.2kg/m²	Ground Snow Load:		Date: 10/04/2026
Spacing: 900	BC Fix/Rest: Metal direct @ 600c/600c	Structure: House		Page: 5


Client: BSPOKE LUXURY HOMES PTY LTD	BB Truss & Timber Pty.Ltd. (A.B.N. 20 986 756 544) 41 Keilor Park Drive Keilor Park 3042 (PH) 9331 7075	Job No: K0964
Site: LOT 735 15 LEICHHARDT AVE BURNSIDE VIC 3023 AUS		Truss: Layout created H1
Ref:		Type: Hip Truss
		Lamination/Quantity: 1/4

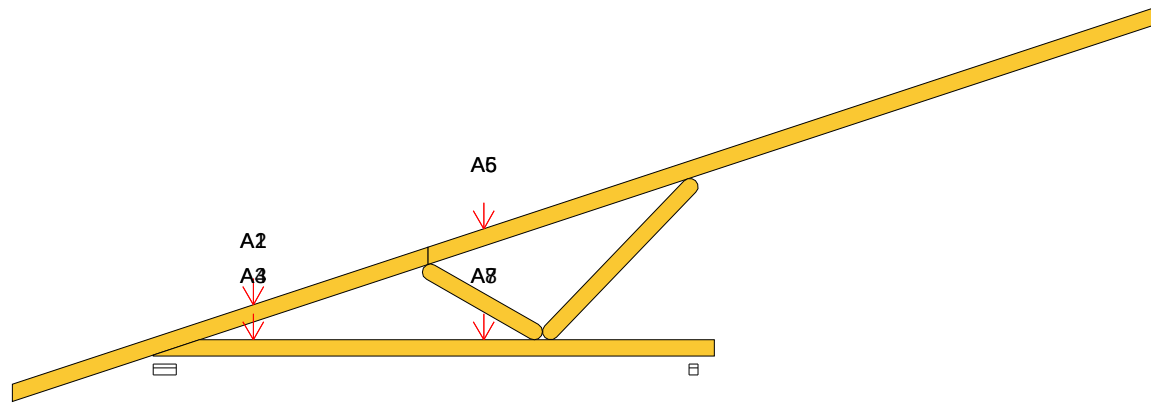

LOADS ON TRUSS: A=Auto loads by system; S=Service loads; Uc=User defined concentrated loads; Ud=User defined distributed loads
Note: -ve signed loads act downwards, +ve signed loads act upwards

Indicator	A1(kN)	A2(kN)	A3(kN)	A4(kN)	A5(kN)	A6(kN)	A7(kN)	A8(kN)
DL	0.089	0.089	0.009	0.009	-0.022	-0.022	-0.035	-0.035
LL	0.116	0.116	0.001	0.001	-0.057	-0.057	-0.012	-0.012
WL	-0.290	-0.290	-0.035	-0.035	0.132	0.132	0.057	0.057
Desc	C1	C1	C1	C1	C2	C2	C2	C2

Client: BSPOKE LUXURY HOMES PTY LTD	BB Truss & Timber Pty.Ltd. (A.B.N. 20 986 756 544) 41 Keilor Park Drive Keilor Park 3042 (PH) 9331 7075	Job No: K0964
Site: LOT 735 15 LEICHHARDT AVE BURNSIDE VIC 3023 AUS		Truss: Layout created C1
Ref:		Type: 390 Creeper
		Lamination/Quantity: 1/8

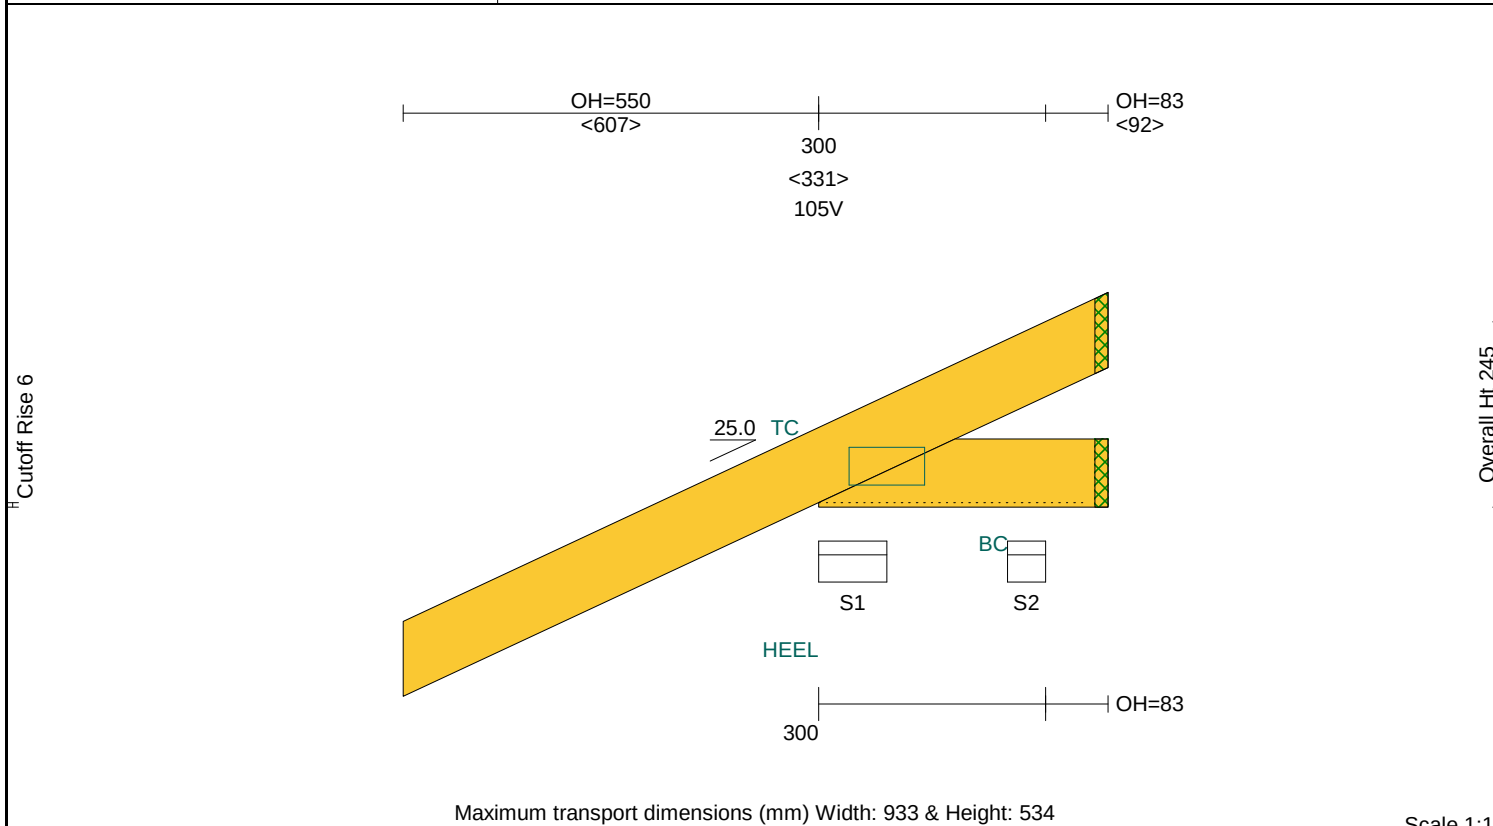

TIMBER:						
Member	Size & Grade			Def	Jnt	Grp Rest
TC	90x35-MGP10	H0	ADS		JD5	900
BC	90x35-MGP10	H0	ADS		JD5	600


PLATES:						
Joint	Size & Grade		Camber	X / Y / Rtn		
HEEL	50x100-MN			40 29 0		

Vertical Reactions at Supports				[AS/NZS 1170.0-2002, 1170.1-2002, 1170.2-2021, 1170.3-2003][AS 1720.1-2010]
Support	(No.)	S1	S2	
1.35DL	(kN)	0.27	-0.07	
1.2DL + 1.5MLL	(kN)	0.64	-0.18	
0.9DL + 1WL	(kN)	-0.44	0.13	
Tie Down	Required	1 MGrip	1 MGrip	
Bearing				
(Note: Tie down capacity based on JD4. Bearing capacity based on timber properties of the member onto support, and SD7 for support.)				

Weight of timber & plate (excl. brackets):	2.4kg
--	--------------

Span: 300	Roofing: Metal Sheet@7kg/m²	Wind / Ext / Int: N2 / 0.6 / 0.2	All dimensions in millimetres. This drawing should be read in conjunction with Multinail Technical sheets.	Version: 1.14.3
Pitch: 25.00	TC Fix/Rest: Metal @ 900c/900c	Fascia Type: As per AS1720.3-2016		User: (TN-012-015)
Overhang: 550/83	Ceiling: Plaster 10mm Supa Span@8.2kg/m²	Ground Snow Load:		Date: 10/04/2026
Spacing: 900	BC Fix/Rest: Metal direct @ 600c/600c	Structure: House		Page: 7

Client: BSPOKE LUXURY HOMES PTY LTD	BB Truss & Timber Pty.Ltd. (A.B.N. 20 986 756 544) 41 Keilor Park Drive Keilor Park 3042 (PH) 9331 7075	Job No: K0964
Site: LOT 735 15 LEICHHARDT AVE BURNSIDE VIC 3023 AUS		Truss: Layout created C2
Ref:		Type: 1290 Creeper
		Lamination/Quantity: 1/8

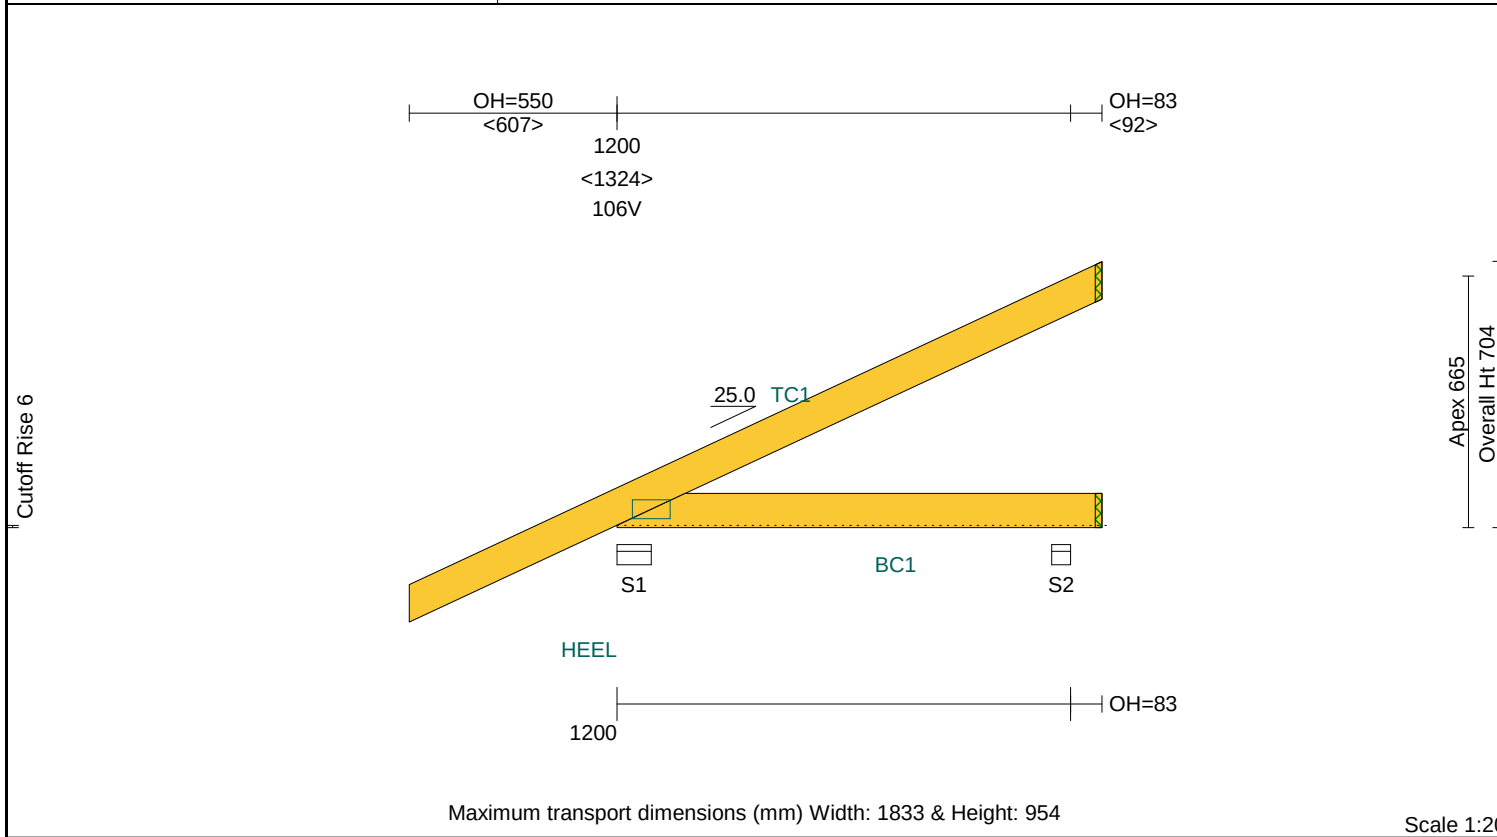

TIMBER:

Member	Size & Grade	Def	Jnt	Grp	Rest
TC1	90x35-MGP10 H0 ADS		JD5		900
BC1	90x35-MGP10 H0 ADS		JD5		600

PLATES:

Joint	Size & Grade	Camber	X	/	Y	/	Rtn
HEEL	50x100-MN		40		23		0

Vertical Reactions at Supports

Support	(No.)	S1	S2
1.35DL	(kN)	0.28	0.14
1.2DL + 1.5MLL	(kN)	0.69	0.35
0.9DL + 1WL	(kN)	-0.53	-0.38
Tie Down	Required	1 MGrip	1 MGrip

Bearing

(Note: Tie down capacity based on JD4. Bearing capacity based on timber properties of the member onto support, and SD7 for support.)

Weight of timber & plate (excl. brackets): **5.4kg**


Span: 1200	Roofing: Metal Sheet@7kg/m²	Wind / Ext / Int: N2 / 0.6 / 0.2
Pitch: 25.00	TC Fix/Rest: Metal @ 900c/900c	Fascia Type: As per AS1720.3-2016
Overhang: 550/83	Ceiling: Plaster 10mm Supa Span@8.2kg/m²	Ground Snow Load:
Spacing: 900	BC Fix/Rest: Metal direct @ 600c/600c	Structure: House

All dimensions in millimetres. This drawing should be read in conjunction with Multinail Technical sheets.



Version: 1.14.3
User: (TN-012-015)
Date: 10/04/2026
Page: 8

Client: BSPOKE LUXURY HOMES PTY LTD	BB Truss & Timber Pty.Ltd. (A.B.N. 20 986 756 544) 41 Keilor Park Drive Keilor Park 3042 (PH) 9331 7075	Job No: K0964
Site: LOT 735 15 LEICHHARDT AVE BURNSIDE VIC 3023 AUS		Truss: Layout created J1
Ref:		Type: 2190 Jack
		Lamination/Quantity: 1/4

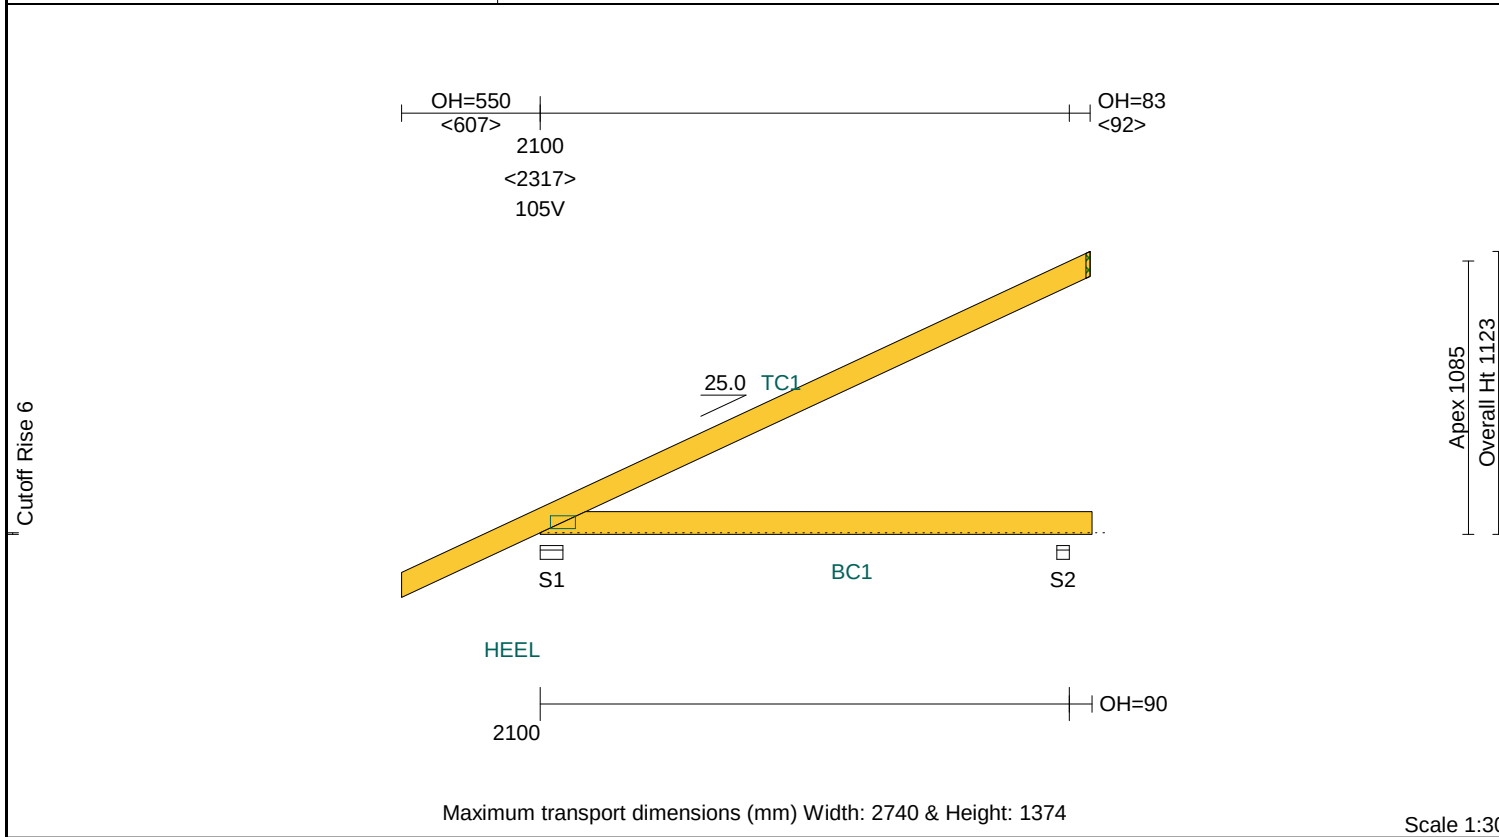

TIMBER:									
Member	Size & Grade				Def	Jnt	Grp	Rest	
TC1	90x35-MGP10	H0	ADS		2	JD5		900	
BC1	90x35-MGP10	H0	ADS		2	JD5		600	

PLATES:									
Joint	Size & Grade				Camber	X	/	Y	/ Rtn
HEEL	50x100-MN					40		23	0


Vertical Reactions at Supports				[AS/NZS 1170.0-2002, 1170.1-2002, 1170.2-2021, 1170.3-2003][AS 1720.1-2010]	
Support	(No.)	S1	S2		
1.35DL	(kN)	0.38	0.26		
1.2DL + 1.5MLL	(kN)	0.89	0.63		
0.9DL + 1WL	(kN)	-0.67	-0.65		
Tie Down	Required	1 MGrip	1 MGrip		
Bearing					
(Note: Tie down capacity based on JD4. Bearing capacity based on timber properties of the member onto support, and SD7 for support.)					

Weight of timber & plate (excl. brackets): **8.3kg**

Span:	2100	Roofing:	Metal Sheet@7kg/m²	Wind / Ext / Int:	N2 / 0.6 / 0.2	All dimensions in millimetres. This drawing should be read in conjunction with Multinail Technical sheets.	Version:	1.14.3
Pitch:	25.00	TC Fix/Rest:	Metal @ 900c/900c	Fascia Type:	As per AS1720.3-2016		User:	(TN-012-015)
Overhang:	550/83	Ceiling:	Plaster 10mm Supa Span@8.2kg/m²	Ground Snow Load:			Date:	10/04/2026
Spacing:	900	BC Fix/Rest:	Metal direct @ 600c/600c	Structure:	House		Page:	9



Client: BSPOKE LUXURY HOMES PTY LTD	BB Truss & Timber Pty.Ltd. (A.B.N. 20 986 756 544) 41 Keilor Park Drive Keilor Park 3042 (PH) 9331 7075	Job No: K0964
Site: LOT 735 15 LEICHHARDT AVE BURNSIDE VIC 3023 AUS		Truss: Layout created J2
Ref:		Type: 3090 Jack Lamination/Quantity: 1/2

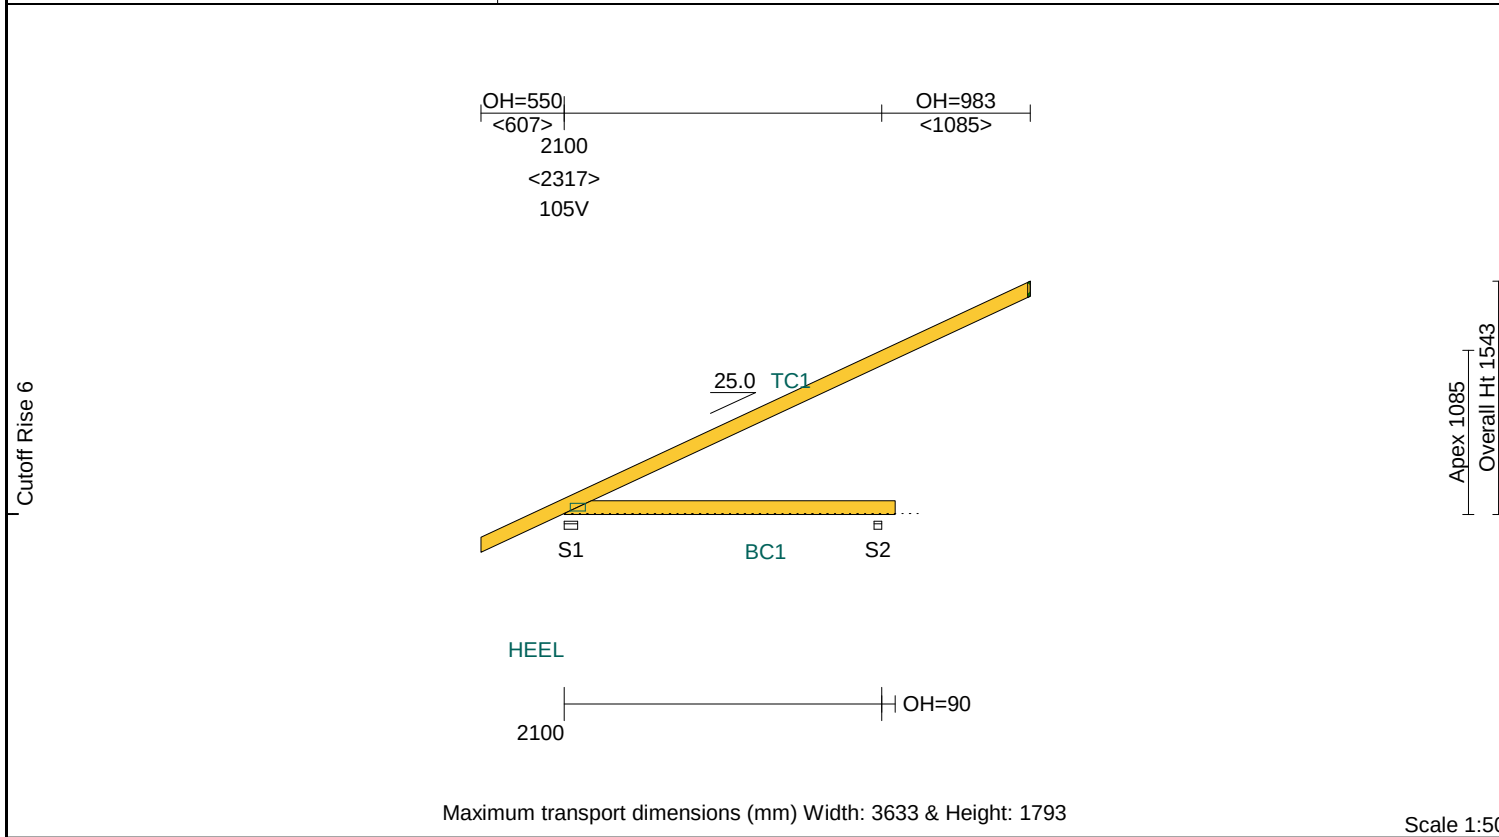

TIMBER:									
Member	Size & Grade				Def	Jnt	Grp	Rest	
TC1	90x35-MGP10	H0	ADS		1	JD5		900	
BC1	90x35-MGP10	H0	ADS		2	JD5		600	


PLATES:									
Joint	Size & Grade				Camber	X	/	Y	/ Rtn
HEEL	50x100-MN					40		23	0

Vertical Reactions at Supports				[AS/NZS 1170.0-2002, 1170.1-2002, 1170.2-2021, 1170.3-2003][AS 1720.1-2010]	
Support	(No.)	S1	S2		
1.35DL	(kN)	0.37	0.36		
1.2DL + 1.5MLL	(kN)	0.83	1.03		
0.9DL + 1WL	(kN)	-0.49	-1.12		
Tie Down	Required	1 M Grip	1 M Grip		
Bearing					
(Note: Tie down capacity based on JD4. Bearing capacity based on timber properties of the member onto support, and SD7 for support.)					

Weight of timber & plate (excl. brackets):	9.9kg
--	--------------

Span: 2100	Roofing: Metal Sheet@7kg/m²	Wind / Ext / Int: N2 / 0.6 / 0.2	All dimensions in millimetres. This drawing should be read in conjunction with Multinail Technical sheets.	Version: 1.14.3
Pitch: 25.00	TC Fix/Rest: Metal @ 900c/900c	Fascia Type: As per AS1720.3-2016		User: (TN-012-015)
Overhang: 550/983	Ceiling: Plaster 10mm Supa Span@8.2kg/m²	Ground Snow Load:		Date: 10/04/2026
Spacing: 900	BC Fix/Rest: Metal direct @ 600c/600c	Structure: House		Page: 10

Client: BSPOKE LUXURY HOMES PTY LTD	BB Truss & Timber Pty.Ltd. (A.B.N. 20 986 756 544) 41 Keilor Park Drive Keilor Park 3042 (PH) 9331 7075	Job No: K0964
Site: LOT 735 15 LEICHHARDT AVE BURNSIDE VIC 3023 AUS		Truss: Layout created J3
Ref:	This truss has USER DEFINED LOADS applied.	Type: 3922 Jack -UL
		Lamination/Quantity: 1/2

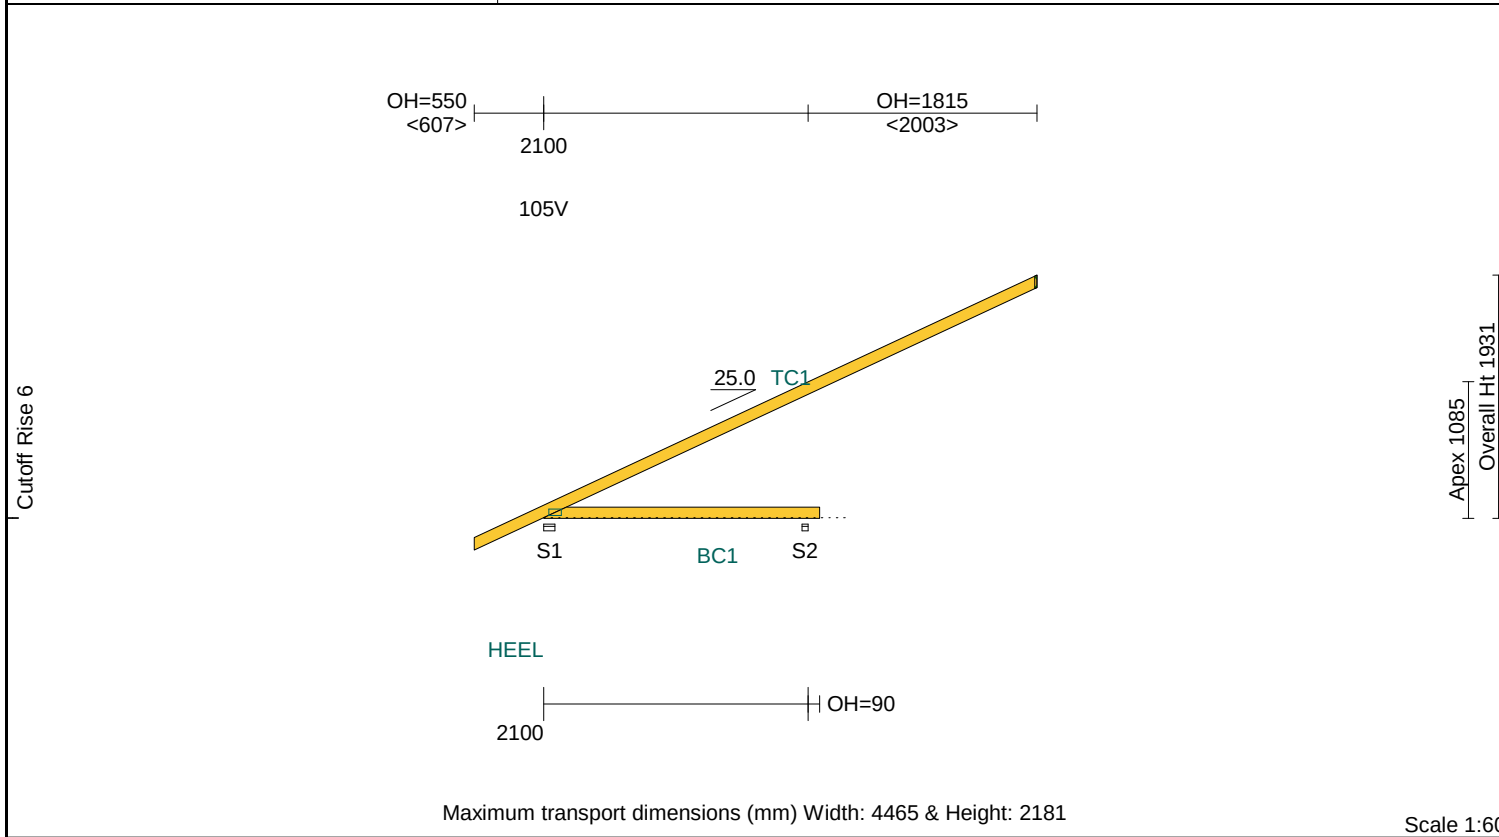

TIMBER:									
Member	Size & Grade				Def	Jnt	Grp	Rest	
TC1	90x35-MGP10	H0	ADS		1	JD5		900	
BC1	90x35-MGP10	H0	ADS		2	JD5		600	

PLATES:									
Joint	Size & Grade				Camber	X	/	Y	/ Rtn
HEEL	50x100-MN					40		23	0


Vertical Reactions at Supports				[AS/NZS 1170.0-2002, 1170.1-2002, 1170.2-2021, 1170.3-2003][AS 1720.1-2010]	
Support	(No.)	S1	S2		
1.35DL	(kN)	0.37	0.67		
1.2DL + 1.5MLL	(kN)	0.83	1.29		
0.9DL + 1WL	(kN)	-0.40	-0.89		
Tie Down	Required	1 MGrip	1 MGrip		
Bearing					

(Note: Tie down capacity based on JD4. Bearing capacity based on timber properties of the member onto support, and SD7 for support.)

Weight of timber & plate (excl. brackets): **11.4kg**

Span: 2100	Roofing: Metal Sheet@7kg/m²	Wind / Ext / Int: N2 / 0.6 / 0.2	All dimensions in millimetres. This drawing should be read in conjunction with Multinail Technical sheets.	Version: 1.14.3
Pitch: 25.00	TC Fix/Rest: Metal @ 900c/900c	Fascia Type: As per AS1720.3-2016		User: (TN-012-015)
Overhang: 550/1815	Ceiling: Plaster 10mm Supa Span@8.2kg/m²	Ground Snow Load:		Date: 10/04/2026
Spacing: 900	BC Fix/Rest: Metal direct @ 600c/600c	Structure: House		Page: 11


Client: BSPOKE LUXURY HOMES PTY LTD	BB Truss & Timber Pty.Ltd. (A.B.N. 20 986 756 544) 41 Keilor Park Drive Keilor Park 3042 (PH) 9331 7075	Job No: K0964
Site: LOT 735 15 LEICHHARDT AVE BURNSIDE VIC 3023 AUS		Truss: Layout created J3
Ref:	This truss has USER DEFINED LOADS applied.	Type: 3922 Jack -UL
		Lamination/Quantity: 1/2

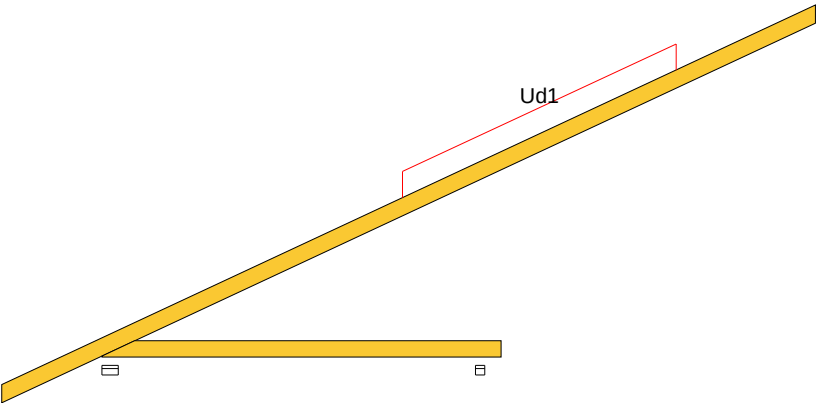

LOADS ON TRUSS: A=Auto loads by system; S=Service loads; Uc=User defined concentrated loads; Ud=User defined distributed loads
Note: -ve signed loads act downwards, +ve signed loads act upwards

Indicator	Ud1(kN/m)
DL	-0.221
LL	0.000
WL	0.000
Desc	

Client: BSPOKE LUXURY HOMES PTY LTD	BB Truss & Timber Pty.Ltd. (A.B.N. 20 986 756 544) 41 Keilor Park Drive Keilor Park 3042 (PH) 9331 7075	Job No: K0964
Site: LOT 735 15 LEICHHARDT AVE BURNSIDE VIC 3023 AUS		Truss: Layout created T4
Ref:		Type: TG2190 Lamination/Quantity: 1/1

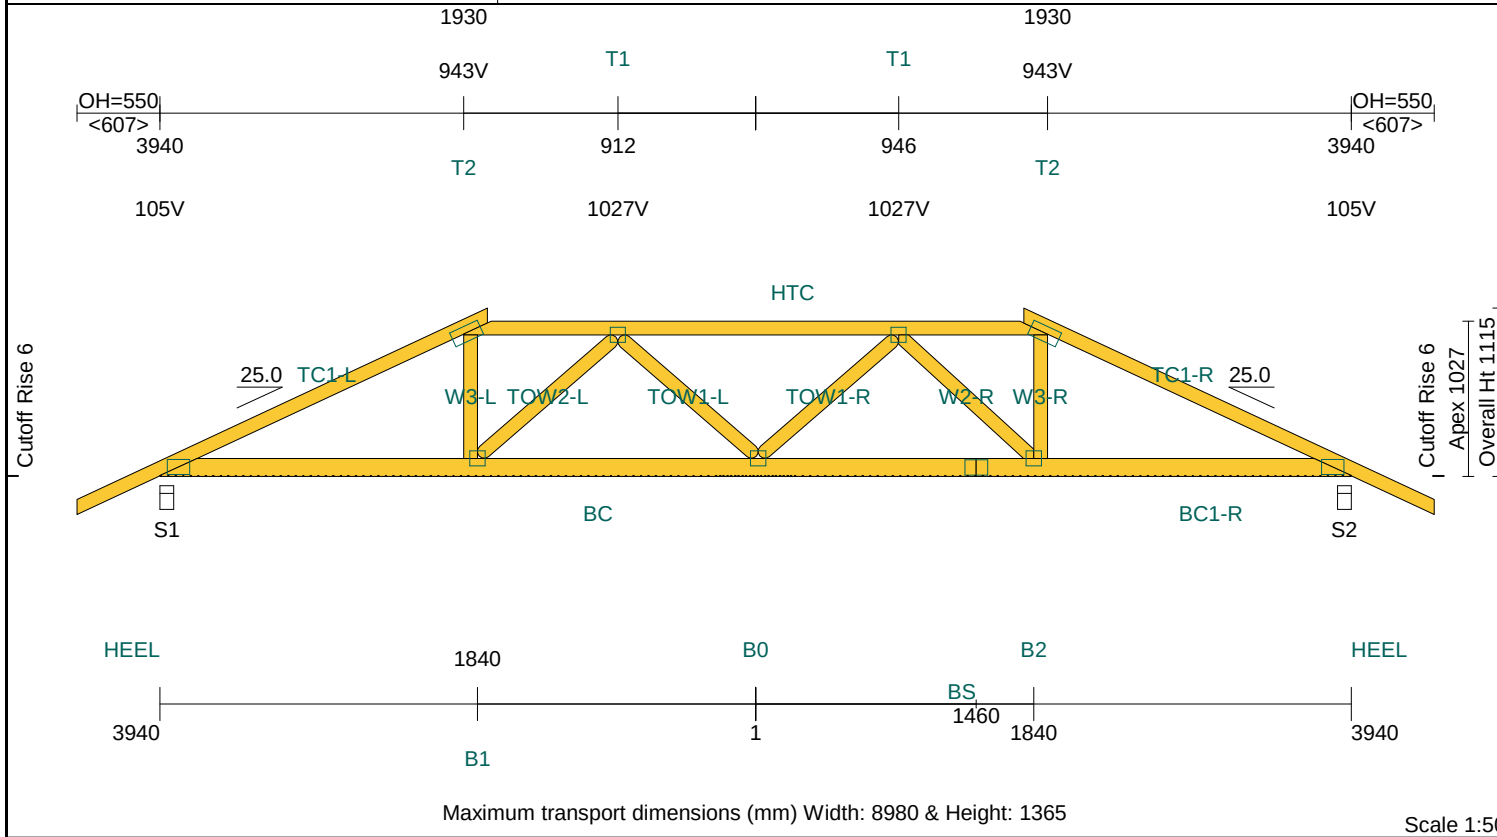

TIMBER:

Member	Size & Grade	Def	Jnt	Grp	Rest
TC1	90x35-MGP10 H0 ADS	1	JD5		900
BC	120x35-MGP10 H0 ADS	1	JD5		600
BC1-R	120x35-MGP10 H0 ADS	1	JD5		600
HTC	90x35-MGP10 H0 ADS	2	JD5		900
W2-R	90x35-MGP10 H0 ADS		JD5		
W3	90x35-MGP10 H0 ADS		JD5		
TOW1	90x35-MGP10 H0 ADS		JD5		
TOW2-L	90x35-MGP10 H0 ADS		JD5		

PLATES:

Joint	Size & Grade	Camber	X	Y	Rtn
HEEL	100x150-MN		47	13	0
T1	100x100-MN		50	50	0
T2	100x200-MN		118	45	25
B0	100x100-MN	4	=	50	0
B1-L	100x100-MN	3	=	50	0
B2-R	100x100-MN	3	=	50	0
BS	100x150-MN		=	50	0

Vertical Reactions at Supports

Support	(No.)	S1	S2
1.35DL	(kN)	2.36	2.36
1.2DL + 1.5MLL	(kN)	5.37	5.37
0.9DL + 1WL	(kN)	-4.28	-4.28
Tie Down	Required	2 MGrps	2 MGrps
Bearing	Member/Support	0k/0k	0k/0k

(Note: Tie down capacity based on JD4. Bearing capacity based on timber properties of the member onto support, and SD7 for support.)

Weight of timber & plate (excl. brackets): **44.5kg**


Span: 7880	Roofing: Metal Sheet@7kg/m²	Wind / Ext / Int: N2 / 0.6 / 0.2
Pitch: 25.00/25.00	TC Fix/Rest: Metal @ 900c/900c	Fascia Type: As per AS1720.3-2016
Overhang: 550/550	Ceiling: Plaster 10mm Supa Span@8.2kg/m²	Ground Snow Load:
Spacing: 900	BC Fix/Rest: Metal direct @ 600c/600c	Structure: House

All dimensions in millimetres. This drawing should be read in conjunction with Multinail Technical sheets.



Version: 1.14.3
User: (TN-012-015)
Date: 10/04/2026
Page: 13

Client: BSPOKE LUXURY HOMES PTY LTD	BB Truss & Timber Pty.Ltd. (A.B.N. 20 986 756 544) 41 Keilor Park Drive Keilor Park 3042 (PH) 9331 7075	Job No: K0964
Site: LOT 735 15 LEICHHARDT AVE BURNSIDE VIC 3023 AUS		Truss: Layout created T4
Ref:		Type: TG2190
		Lamination/Quantity: 1/1

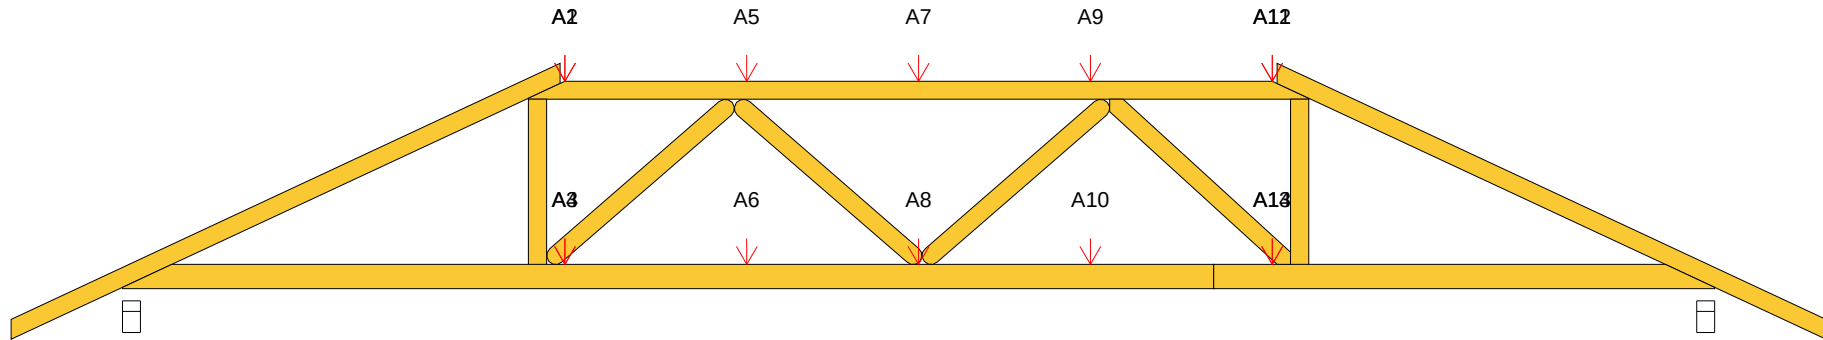


LOADS ON TRUSS: A=Auto loads by system; S=Service loads; Uc=User defined concentrated loads; Ud=User defined distributed loads
Note: -ve signed loads act downwards, +ve signed loads act upwards

Indicator	A1(kN)	A2(kN)	A3(kN)	A4(kN)	A5(kN)	A6(kN)	A7(kN)	A8(kN)	A9(kN)	A10(kN)
DL	-0.218	-0.052	0.016	-0.071	-0.323	-0.071	-0.301	-0.071	-0.323	-0.071
LL	-0.283	-0.135	0.007	-0.013	-0.449	-0.023	-0.424	-0.022	-0.449	-0.023
WL	0.744	0.290	-0.027	0.102	1.058	0.198	0.996	0.190	1.058	0.198
Desc	H1	J1	H1	J1	J4	J4	J3	J3	J5	J5

Indicator	A11(kN)	A12(kN)	A13(kN)	A14(kN)
DL	-0.218	-0.052	0.016	-0.071
LL	-0.283	-0.135	0.007	-0.013
WL	0.744	0.290	-0.027	0.102
Desc	H1	J1	H1	J1

Client: BSPOKE LUXURY HOMES PTY LTD	BB Truss & Timber Pty.Ltd. (A.B.N. 20 986 756 544) 41 Keilor Park Drive Keilor Park 3042 (PH) 9331 7075	Job No: K0964
Site: LOT 735 15 LEICHHARDT AVE BURNSIDE VIC 3023 AUS		Truss: Layout created J4
Ref:	This truss has USER DEFINED LOADS applied.	Type: 3090 Jack -UL
		Lamination/Quantity: 1/1

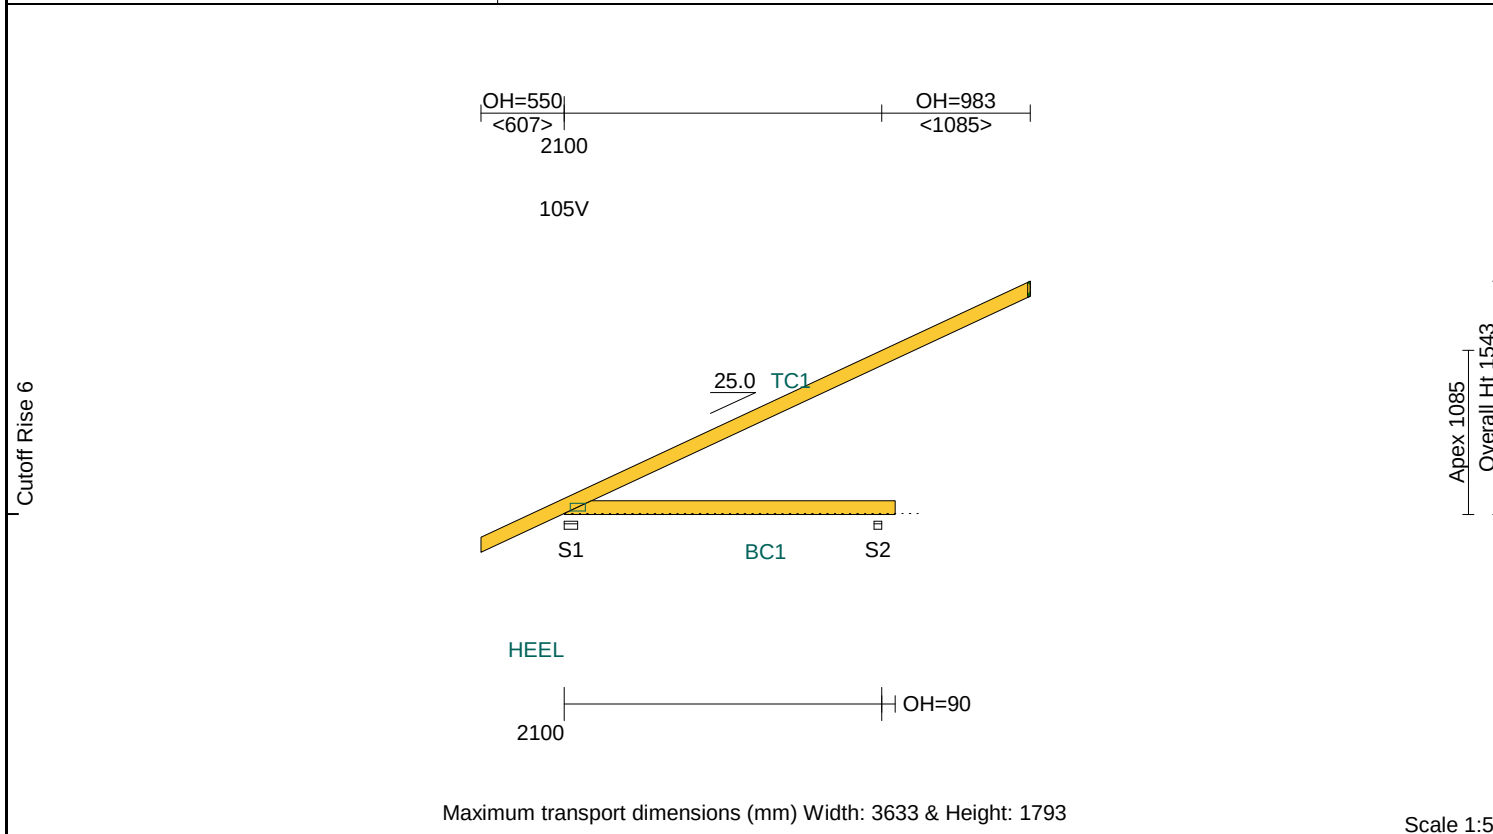

TIMBER:

Member	Size & Grade	Def	Jnt	Grp	Rest
TC1	90x35-MGP10 H0 ADS	1	JD5		900
BC1	90x35-MGP10 H0 ADS	2	JD5		600

PLATES:

Joint	Size & Grade	Camber	X	Y	Rtn
HEEL	50x100-MN		40	23	0

Vertical Reactions at Supports [AS/NZS 1170.0-2002, 1170.1-2002, 1170.2-2021, 1170.3-2003][AS 1720.1-2010]

Support	(No.)	S1	S2
1.35DL	(kN)	0.37	0.70
1.2DL + 1.5MLL	(kN)	0.83	1.33
0.9DL + 1WL	(kN)	-0.49	-0.89
Tie Down	Required	1 MGrip	1 MGrip
Bearing			

(Note: Tie down capacity based on JD4. Bearing capacity based on timber properties of the member onto support, and SD7 for support.)

Weight of timber & plate (excl. brackets): **9.9kg**


Span: 2100	Roofing: Metal Sheet@7kg/m²	Wind / Ext / Int: N2 / 0.6 / 0.2
Pitch: 25.00	TC Fix/Rest: Metal @ 900c/900c	Fascia Type: As per AS1720.3-2016
Overhang: 550/983	Ceiling: Plaster 10mm Supa Span@8.2kg/m²	Ground Snow Load:
Spacing: 900	BC Fix/Rest: Metal direct @ 600c/600c	Structure: House

All dimensions in millimetres. This drawing should be read in conjunction with Multinail Technical sheets.



Version: 1.14.3
User: (TN-012-015)
Date: 10/04/2026
Page: 15


Client: BSPOKE LUXURY HOMES PTY LTD	BB Truss & Timber Pty.Ltd. (A.B.N. 20 986 756 544) 41 Keilor Park Drive Keilor Park 3042 (PH) 9331 7075	Job No: K0964
Site: LOT 735 15 LEICHHARDT AVE BURNSIDE VIC 3023 AUS		Truss: Layout created J4
Ref:	This truss has USER DEFINED LOADS applied.	Type: 3090 Jack -UL
		Lamination/Quantity: 1/1

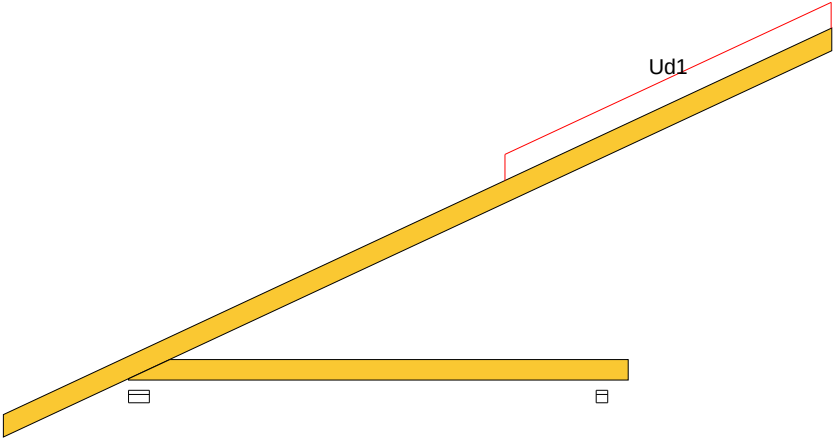

LOADS ON TRUSS: A=Auto loads by system; S=Service loads; Uc=User defined concentrated loads; Ud=User defined distributed loads
Note: -ve signed loads act downwards, +ve signed loads act upwards

Indicator	Ud1(kN/m)
DL	-0.221
LL	0.000
WL	0.000
Desc	

Client: BSPOKE LUXURY HOMES PTY LTD	BB Truss & Timber Pty.Ltd. (A.B.N. 20 986 756 544) 41 Keilor Park Drive Keilor Park 3042 (PH) 9331 7075	Job No: K0964
Site: LOT 735 15 LEICHHARDT AVE BURNSIDE VIC 3023 AUS		Truss: Layout created J5
Ref:	This truss has USER DEFINED LOADS applied.	Type: 3090 Jack -UL
		Lamination/Quantity: 1/1

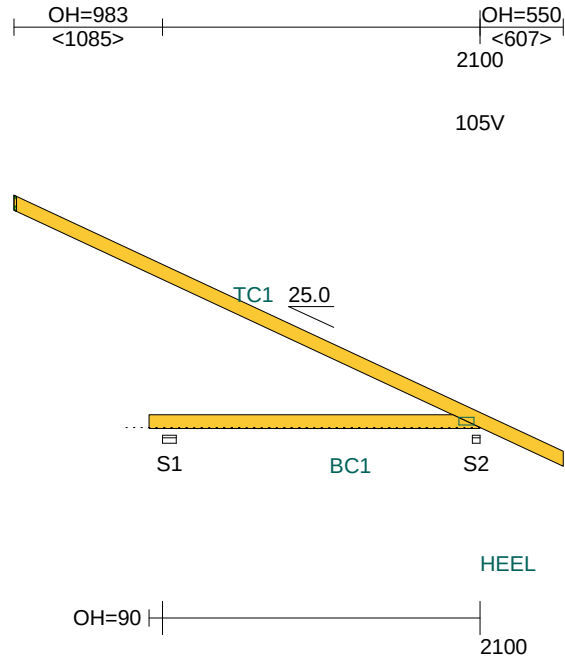

Cutoff Rise 6
Apex 1085
Overall Ht 1543

TIMBER:

Member	Size & Grade	Def	Jnt	Grp	Rest
TC1	90x35-MGP10 H0 ADS	1	JD5		900
BC1	90x35-MGP10 H0 ADS	2	JD5		600

PLATES:

Joint	Size & Grade	Camber	X	Y	Rtn
HEEL	50x100-MN		40	23	0

Maximum transport dimensions (mm) Width: 3633 & Height: 1793

Scale 1:50

Vertical Reactions at Supports

[AS/NZS 1170.0-2002, 1170.1-2002, 1170.2-2021, 1170.3-2003][AS 1720.1-2010]


Support	(No.)	S1	S2
1.35DL	(kN)	0.70	0.37
1.2DL + 1.5MLL	(kN)	1.33	0.83
0.9DL + 1WL	(kN)	-0.89	-0.49
Tie Down	Required	1 MGrip	1 MGrip
Bearing			

(Note: Tie down capacity based on JD4. Bearing capacity based on timber properties of the member onto support, and SD7 for support.)

Weight of timber & plate (excl. brackets): **9.9kg**

Span: 2100	Roofing: Metal Sheet@7kg/m²	Wind / Ext / Int: N2 / 0.6 / 0.2	All dimensions in millimetres. This drawing should be read in conjunction with Multinail Technical sheets.	Version: 1.14.3
Pitch: 25.00	TC Fix/Rest: Metal @ 900c/900c	Fascia Type: As per AS1720.3-2016		User: (TN-012-015)
Overhang: 983/550	Ceiling: Plaster 10mm Supa Span@8.2kg/m²	Ground Snow Load:		Date: 10/04/2026
Spacing: 900	BC Fix/Rest: Metal direct @ 600c/600c	Structure: House		Page: 17


Client: BSPOKE LUXURY HOMES PTY LTD	BB Truss & Timber Pty.Ltd. (A.B.N. 20 986 756 544) 41 Keilor Park Drive Keilor Park 3042 (PH) 9331 7075	Job No: K0964
Site: LOT 735 15 LEICHHARDT AVE BURNSIDE VIC 3023 AUS		Truss: Layout created J5
Ref:	This truss has USER DEFINED LOADS applied.	Type: 3090 Jack -UL
		Lamination/Quantity: 1/1

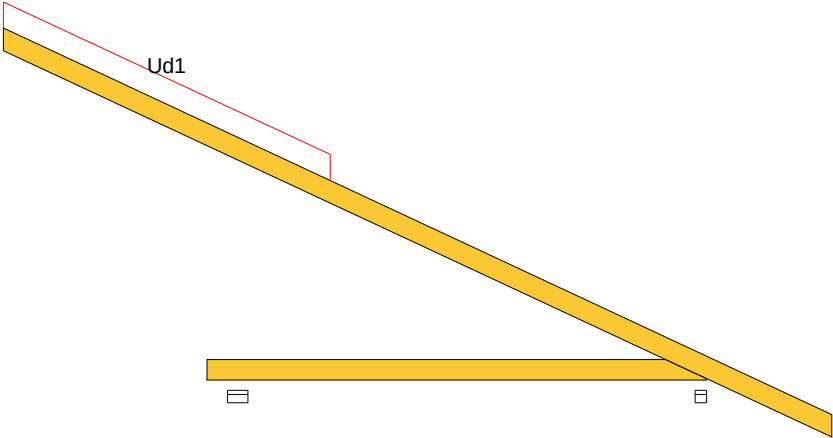

LOADS ON TRUSS: A=Auto loads by system; S=Service loads; Uc=User defined concentrated loads; Ud=User defined distributed loads
Note: -ve signed loads act downwards, +ve signed loads act upwards

Indicator	Ud1(kN/m)
DL	-0.221
LL	0.000
WL	0.000
Desc	

Client: BSPOKE LUXURY HOMES PTY LTD	BB Truss & Timber Pty.Ltd.	Job No: K0964
Site: LOT 735 15 LEICHHARDT AVE BURNSIDE VIC 3023 AUS	(A.B.N. 20 986 756 544) 41 Keilor Park Drive Keilor Park 3042 (PH) 9331 7075	Truss: Layout created T5
Ref:	(pt) : 1 mid panel tie(s) required to each bottom chord panel	Type: LeftHalf Standard
		Lamination/Quantity: 1/8

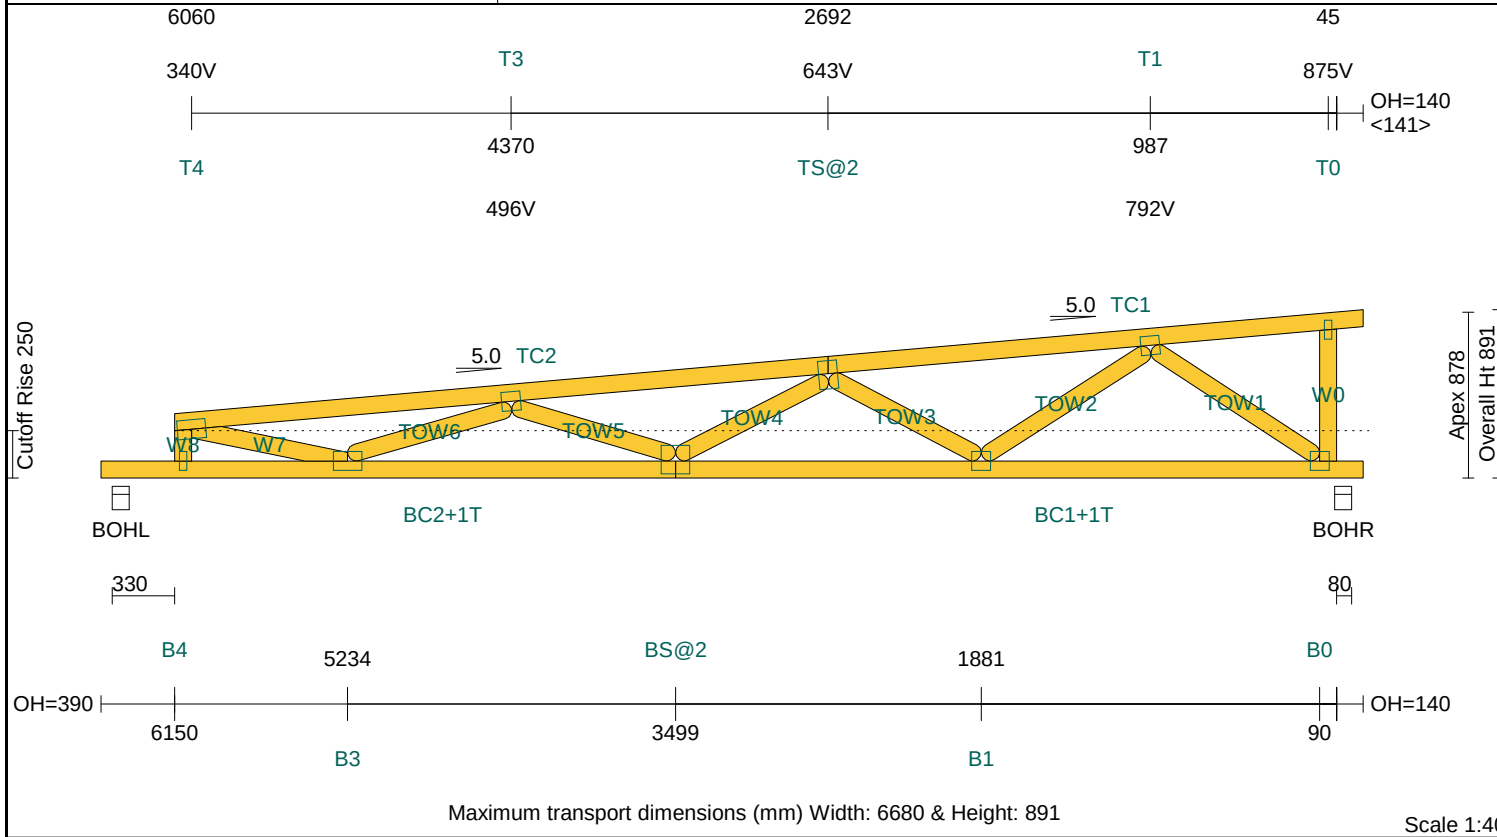

TIMBER:

Member	Size & Grade	Def	Jnt	Grp	Rest
TC1	90x35-MGP10 H0 ADS		JD5		900
TC2	90x35-MGP10 H0 ADS	1	JD5		900
BC1+1T	90x35-MGP10 H0 ADS	1	JD5		(pt)
BC2+1T	90x35-MGP10 H0 ADS	1	JD5		(pt)
W0	90x35-MGP10 H0 ADS		JD5		
W7	90x35-MGP10 H0 ADS		JD5		
W8	90x35-MGP10 H0 ADS		JD5		
TOW1	90x35-MGP10 H0 ADS		JD5		
TOW2	90x35-MGP10 H0 ADS		JD5		
TOW3	90x35-MGP10 H0 ADS		JD5		
TOW4	90x35-MGP10 H0 ADS		JD5		
TOW5	90x35-MGP10 H0 ADS		JD5		
TOW6	90x35-MGP10 H0 ADS		JD5		

PLATES:

Joint	Size & Grade	Camber	X	Y	Rtn
T0	38x100-MN		=	=	0
T1	100x100-MN		50	50	0
T3	100x100-MN		50	50	0
T4	100x150-MN		75	50	0
B0	100x100-MN		50	50	0
B1	100x100-MN	3	50	50	0
B3	100x150-MN	4	75	50	0
B4	38x100-MN	3	=	=	0
TS@2	150x100-MN		=	68	0
BS@2	150x150-MN	4	=	68	0

Vertical Reactions at Supports

Support	(No.)	BOHL	BOHR
1.35DL	(kN)	0.81	0.89
1.2DL + 1.5MLL	(kN)	1.82	2.00
0.9DL + 1WL	(kN)	-2.25	-2.50
Tie Down	Required	1 M Grip	1 M Grip
Bearing	Member/Support	Ok/Ok	Ok/Ok

(Note: Tie down capacity based on JD4. Bearing capacity based on timber properties of the member onto support, and SD7 for support.)

Weight of timber & plate (excl. brackets): **34.0kg**


Span:	6150	Roofing:	Metal Sheet@7kg/m²	Wind / Ext / Int:	N2 / 0.9 / 0.2
Pitch:	5.00	TC Fix/Rest:	Metal @ 900c/900c	Fascia Type:	As per AS1720.3-2016
Overhang:	0/140	Ceiling:	Plaster 10mm Supa Span@8.2kg/m²	Ground Snow Load:	
Spacing:	900	BC Fix/Rest:	Metal direct @ 600c/600c	Structure:	House

All dimensions in millimetres. This drawing should be read in conjunction with Multinail Technical sheets.



Version:	1.14.3
User:	(TN-012-015)
Date:	10/04/2026
Page:	19

Client: BSPOKE LUXURY HOMES PTY LTD	BB Truss & Timber Pty.Ltd. (A.B.N. 20 986 756 544) 41 Keilor Park Drive Keilor Park 3042 (PH) 9331 7075	Job No: K0964
Site: LOT 735 15 LEICHHARDT AVE BURNSIDE VIC 3023 AUS		Truss: Layout created T6
Ref:		Type: LeftHalf Standard Lamination/Quantity: 1/5

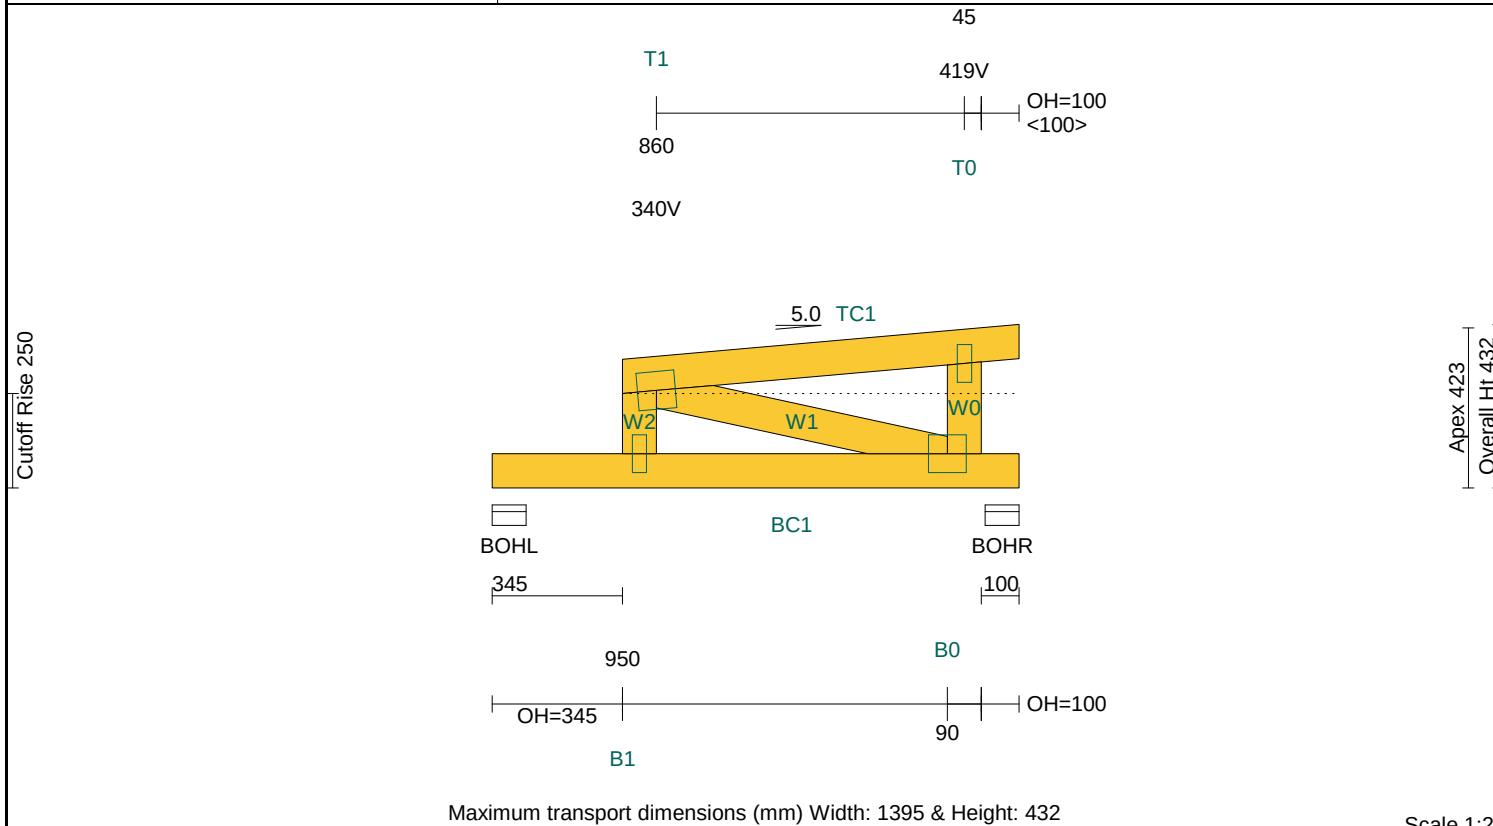

TIMBER:

Member	Size & Grade	Def	Jnt	Grp	Rest
TC1	90x35-MGP10 H0 ADS		JD5		900
BC1	90x35-MGP10 H0 ADS		JD5		600
W0	90x35-MGP10 H0 ADS		JD5		
W1	90x35-MGP10 H0 ADS		JD5		
W2	90x35-MGP10 H0 ADS		JD5		

PLATES:

Joint	Size & Grade	Camber	X /	Y /	Rtn
T0	38x100-MN		=	=	0
T1	100x100-MN		50	50	0
B0	100x100-MN	1	50	50	0
B1	38x100-MN	1	=	=	0


Vertical Reactions at Supports [AS/NZS 1170.0-2002, 1170.1-2002, 1170.2-2021, 1170.3-2003][AS 1720.1-2010]

Support	(No.)	BOHL	BOHR
1.35DL	(kN)	0.17	0.20
1.2DL + 1.5MLL	(kN)	0.39	0.46
0.9DL + 1WL	(kN)	-0.48	-0.60
Tie Down	Required	1 M Grip	1 M Grip
Bearing	Member/Support	0k/0k	0k/0k

(Note: Tie down capacity based on JD4. Bearing capacity based on timber properties of the member onto support, and SD7 for support.)


Weight of timber & plate (excl. brackets): **6.2kg**

Span: 950	Roofing: Metal Sheet@7kg/m²	Wind / Ext / Int: N2 / 0.9 / 0.2	All dimensions in millimetres. This drawing should be read in conjunction with Multinail Technical sheets.	Version: 1.14.3
Pitch: 5.00	TC Fix/Rest: Metal @ 900c/900c	Fascia Type: As per AS1720.3-2016		User: (TN-012-015)
Overhang: 0/100	Ceiling: Plaster 10mm Supa Span@8.2kg/m²	Ground Snow Load:		Date: 10/04/2026
Spacing: 900	BC Fix/Rest: Metal direct @ 600c/600c	Structure: House		Page: 20

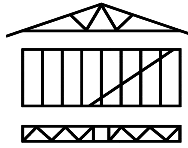

BB TRUSS & TIMBER PTY LTD
email: sales@bbtruss.com.au

MELBOURNE: 9331 7075
BENDIGO: 5444 3636
BALLARAT: 5333 1100

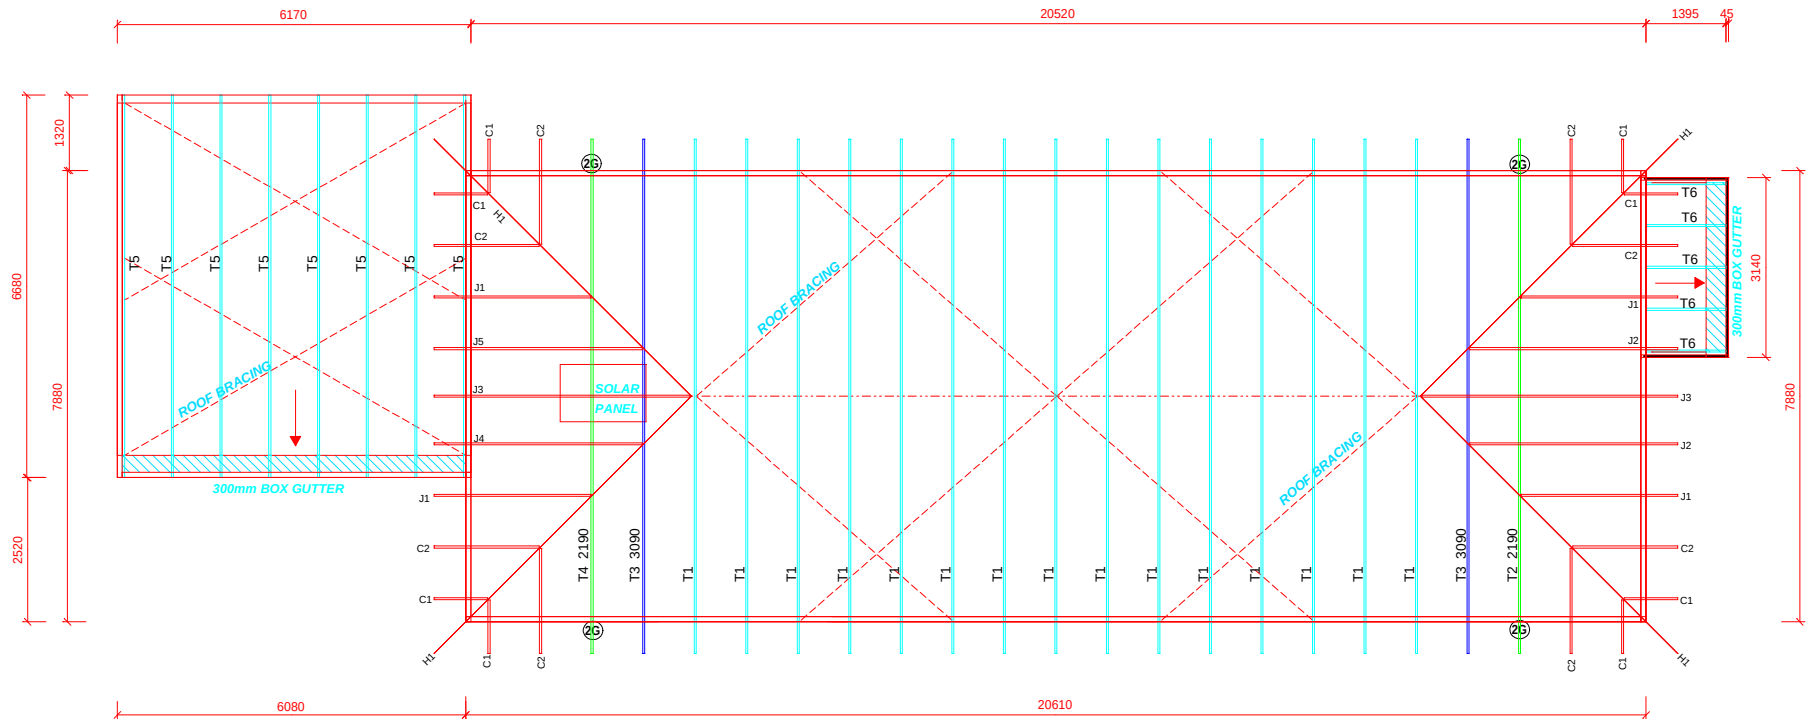

Do not stand on truss chords whilst installing

▬ - Loadbearing Wall

NOTE 1: All beams by others to engineers comps.

NOTE 2: Permanent mid panel bottom chord ties required for plaster direct ceilings.

Trusses to be erected in accordance with Australian Standard AS4440 -2004
Trusses are not to be cut, modified or altered without prior authorisation

Connection of Jack truss top chord to truncated girder:
- 1 Multigrip for Jack span 1800 > unless note otherwise

Connection of truss to top plate:
- 1 Multigrip unless noted otherwise
Ⓔ = Double MultiGrip

Timber: Dry Softwood	Roofing: Metal Sheet@7kg/m ²	Wind Classificatn: N2 / 0.6 / 0.2	BSPOKE LUXURY HOMES PTY LTD LOT 735 15 LEICHHARDT AVE BURNSIDE VIC 3023 AUS 	Detailer: JOEY
Pitch: 5.0 / 25.0 deg	TC fix/rest: Metal @ 900c/900c	Fascia Type: As per AS1720.3-2016		Date: 3/04/2026
Truss Tail: 550 mm	Ceiling: Plaster 10mm Supa Span@8.2kg/m ²	Ground Snow Load: Sg = 0.0 kPa		Scale: 1:85
Spacing: 900 mm	BC fix/rest: Metal direct @ 600c/600c	Structure Type: House		Job No: K0964