

BUILDING AUTHORITY FLOOR JOIST CERTIFICATION

BB Truss & Timber Pty Ltd

JOB : K0964

41 Keilor Park Drive Keilor Park 3042 PH 03 9331 7075 A.C.N.059 242 134

Customer : **LUXURY HOMES PTY LTD**

Site Address : **LOT 735 15 LEICHHARDT AVE
BURNSIDE VIC 3023 AUS**

Reference :

This is to certify that the prefabricated timber floor joists supplied to the above project were manufactured using MULTINAIL metal connectors and detailed using MULTINAIL computer joist design programs in accordance with the National Construction Code (NCC 2022).

The floor joist design and detailing assumes the supporting structure is stable within its own right before the installation of the floor joists.

The specifications used in the design of the joists were as follows:

Timber :	Dry Swd (can include KD Hwd)	Flooring :	Particle (13.9kg/m²)
Spacing :	450	TC Restraints :	300
Wind :	N2	Ceiling Material:	Plaster 10mm Std Core (6.7 kg/m²)
Structure:	House	Ceiling Fixing:	Direct fix @ 450c
Floor Application :	General Areas	Std Chords :	45 TC / 45 BC
Treatment :	H0 - Individual members may be treated different.	Live Load: 1.5 kPa	Point Load: 1.8 kN

All designed joists and pre-cut members utilize the following Australian standards:

AS/NZS 1170.0-2002 Structural design actions Part 0: General Principles
AS/NZS 1170.1-2002 Structural design actions Part 1: Permanent, imposed and other actions
AS/NZS 1170.2-2021 Structural design actions Part 2: Wind actions
AS/NZS 1170.3-2003 Structural design actions Part 3: Snow and Ice
AS 1720.1-2010 Timber Structures Part1 : Design Methods
AS 1720.3-2016 Timber Structures Part3 : Design criteria for timber-framed residential buildings
AS 4055-2021 Wind Loads for Housing
AS 1649-2001 Determination of basic working loads for metal fasteners for timber
AS 4100-2020 Steel Structures Code
AS/NZS 4600-2018 Cold-formed Steel Structures Code

Special Note: Special attention must be given to floor trusses that have a 35mm MGP10 as a top chord.

Due to the design processes and analysis for the design of floor trusses with 35mm MGP10 Top Chords it is essential that the flooring material as specified in the design criteria for this job is securely fixed (according to the manufacture's recommendations, instructions and guidelines) as the flooring material and top chord act together for the design to resist the loads applied.

In conjunction with Multinail Australia's recommendations, all local building authority requirements and any other supplied details must be followed.

Floor joist designs assumes strongbacks are placed and fixed according to Multinail Australia's recommendations.

SIGNATURE: _____




NAME : Joey Meriales (TN-012-015)


POSITION : detailer

DATE : 10/04/2026

For detailed load information refer to the engineering output.

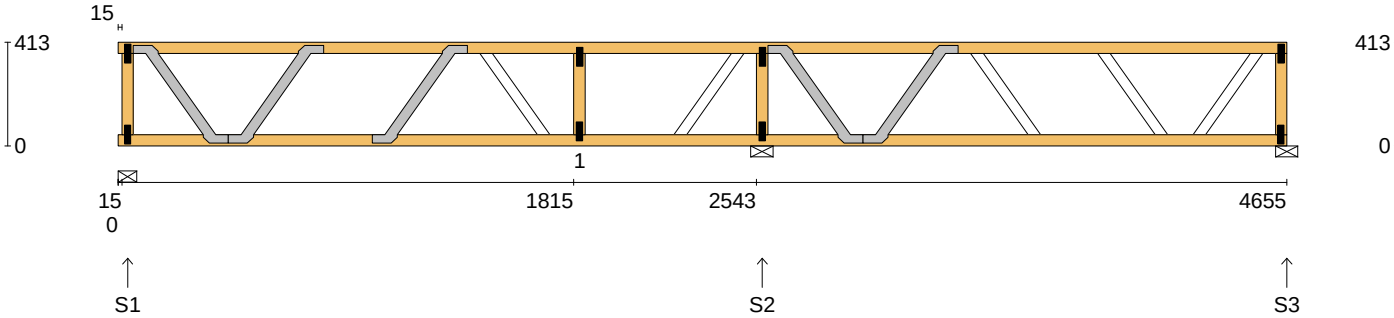		BB Truss & Timber Pty Ltd		Job No: K0964					
Site: LOT 735 15 LEICHHARDT AVE BURNSIDE VIC 3023 AUS		41 Keilor Park Drive, Keilor Park 3042		Weight: 24.42 kg					
Ref:		Joist Name: FJ1 Type: MSJ-400-45 Joists: FJ95, FJ96, FJ97, FJ98		Total Weight: 97.66 kg					
				Laminations: 1					
				TIMBER / PLATES					
				Member	Size	Plating		Restraint	
				BC1	90x45-MGP10 H0 ADS	JD5	450		
				TC1	90x45-MGP10 H0 ADS	JD5	300		
				LEW1	90x45-MGP10 H0 ADS	JD5			
				W1	90x45-MGP10 H0 ADS	JD5			
				W2	90x45-MGP10 H0 ADS	JD5			
				REW1	90x45-MGP10 H0 ADS	JD5			
				Vertical Reactions at Supports				Joint	
					S1	S2	S3	Nail Plate	
1.35DL (kN)	0.30	0.60	0.24	TL1	25x75-MN				
1.2DL + 1.5LL (kN)	1.59	2.86	1.26	BL2	25x75-MN				
				T1	25x75-MN				
				B1	25x75-MN				
				T2	25x75-MN				
				B2	25x75-MN				
				TR1	25x75-MN				
				BR2	25x75-MN				
Span:	4655	Floor Material:	Particle (13.9 kg/m²)	Application:	General Areas	All dimensions in millimetres. This drawing should be read in conjunction with Multinail Technical sheets. Wall plates must be placed at supports only.		Joey Meriales (TN-012-015)	
Overhang:	0/0	Floor Covering:	Std Carpet + Underlay (8 kg/m²)	Live Load:	1.5 kPa			Ver:	Floor 1.14.3
Spacing:	450	Ceiling Material:	Plaster 10mm Std Core (6.7 kg/m²)	Point Load:	1.8 kN			Date:	10/04/2026
Quantity:	4	Ceiling Fixing:	Direct fix @ 450c	Design:	AS 1720.1-2010			Page:	1 of 45


Site: LOT 735 15 LEICHHARDT AVE BURNSIDE VIC 3023 AUS	BB Truss & Timber Pty Ltd 41 Keilor Park Drive, Keilor Park 3042		Job No: K0964
	Joist Name: FJ1 Type: MSJ-400-45		Weight: 24.42 kg
	Joists: FJ95, FJ96, FJ97, FJ98		Total Weight: 97.66 kg
Ref:			Laminations: 1

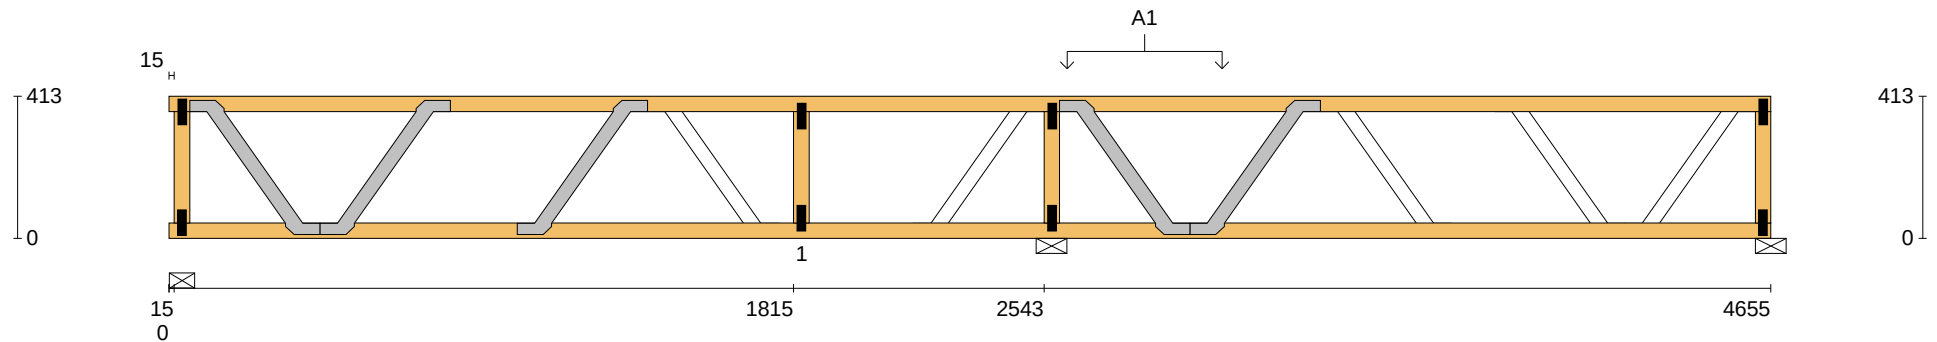


User Def. Load A1
8.70 kg/m²

Applied Load
DL (kN)
LL (kN)
WL Up (kN)
WL Dn (kN)

Span: 4655	Floor Material: Particle (13.9 kg/m²)	Application: General Areas	All dimensions in millimetres. This drawing should be read in conjunction with Multinail Technical sheets. Wall plates must be placed at supports only.	Joey Meriales (TN-012-015)
Overhang: 0/0	Floor Covering: Std Carpet + Underlay (8 kg/m²)	Live Load: 1.5 kPa		Ver: Floor 1.14.3
Spacing: 450	Ceiling Material: Plaster 10mm Std Core (6.7 kg/m²)	Point Load: 1.8 kN		Date: 10/04/2026
Quantity: 4	Ceiling Fixing: Direct fix @ 450c	Design: AS 1720.1-2010		Page: 2 of 45

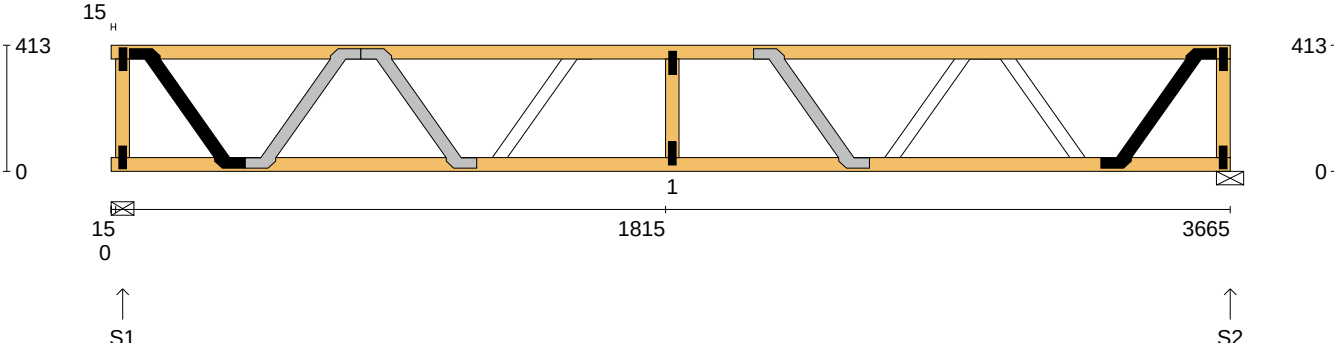		BB Truss & Timber Pty Ltd		Job No: K0964																								
Site: LOT 735 15 LEICHHARDT AVE BURNSIDE VIC 3023 AUS		41 Keilor Park Drive, Keilor Park 3042		Weight: 19.68 kg																								
Ref:		Joist Name: FJ2 Type: MSJ-400-45 Joists: FJ99, FJ100, FJ101, FJ102, FJ103		Total Weight: 98.42 kg																								
				Laminations: 1																								
				TIMBER / PLATES																								
				<table><thead><tr><th>Member</th><th>Size</th><th>Plating</th><th>Restraint</th></tr></thead><tbody><tr><td>BC1</td><td>90x45-MGP10 H0 ADS</td><td>JD5</td><td>450</td></tr><tr><td>TC1</td><td>90x45-MGP10 H0 ADS</td><td>JD5</td><td>300</td></tr><tr><td>LEW1</td><td>90x45-MGP10 H0 ADS</td><td>JD5</td><td></td></tr><tr><td>W1</td><td>90x45-MGP10 H0 ADS</td><td>JD5</td><td></td></tr><tr><td>REW1</td><td>90x45-MGP10 H0 ADS</td><td>JD5</td><td></td></tr></tbody></table>	Member	Size	Plating	Restraint	BC1	90x45-MGP10 H0 ADS	JD5	450	TC1	90x45-MGP10 H0 ADS	JD5	300	LEW1	90x45-MGP10 H0 ADS	JD5		W1	90x45-MGP10 H0 ADS	JD5		REW1	90x45-MGP10 H0 ADS	JD5	
Member	Size	Plating	Restraint																									
BC1	90x45-MGP10 H0 ADS	JD5	450																									
TC1	90x45-MGP10 H0 ADS	JD5	300																									
LEW1	90x45-MGP10 H0 ADS	JD5																										
W1	90x45-MGP10 H0 ADS	JD5																										
REW1	90x45-MGP10 H0 ADS	JD5																										
Vertical Reactions at Supports <table><thead><tr><th></th><th>S1</th><th>S2</th></tr></thead><tbody><tr><td>1.35DL (kN)</td><td>0.44</td><td>0.43</td></tr><tr><td>1.2DL + 1.5LL (kN)</td><td>2.26</td><td>2.21</td></tr></tbody></table>					S1	S2	1.35DL (kN)	0.44	0.43	1.2DL + 1.5LL (kN)	2.26	2.21	<table><thead><tr><th>Joint</th><th>Nail Plate</th></tr></thead><tbody><tr><td>TL1</td><td>25x75-MN</td></tr><tr><td>BL2</td><td>25x75-MN</td></tr><tr><td>T1</td><td>25x75-MN</td></tr><tr><td>B1</td><td>25x75-MN</td></tr><tr><td>TR1</td><td>25x75-MN</td></tr><tr><td>BR2</td><td>25x75-MN</td></tr></tbody></table>		Joint	Nail Plate	TL1	25x75-MN	BL2	25x75-MN	T1	25x75-MN	B1	25x75-MN	TR1	25x75-MN	BR2	25x75-MN
					S1	S2																						
1.35DL (kN)	0.44	0.43																										
1.2DL + 1.5LL (kN)	2.26	2.21																										
Joint	Nail Plate																											
TL1	25x75-MN																											
BL2	25x75-MN																											
T1	25x75-MN																											
B1	25x75-MN																											
TR1	25x75-MN																											
BR2	25x75-MN																											
Span: 3665		Floor Material: Particle (13.9 kg/m²)		Application: General Areas		All dimensions in millimetres. This drawing should be read in conjunction with Multinail Technical sheets. Wall plates must be placed at supports only.		Joey Meriales (TN-012-015)																				
Overhang: 0/0		Floor Covering: Std Carpet + Underlay (8 kg/m²)		Live Load: 1.5 kPa				Ver: Floor 1.14.3																				
Spacing: 450		Ceiling Material: Plaster 10mm Std Core (6.7 kg/m²)		Point Load: 1.8 kN				Date: 10/04/2026																				
Quantity: 5		Ceiling Fixing: Direct fix @ 450c		Design: AS 1720.1-2010				Page: 3 of 45																				

		BB Truss & Timber Pty Ltd 41 Keilor Park Drive, Keilor Park 3042	Job No: K0964
Site: LOT 735 15 LEICHHARDT AVE BURNSIDE VIC 3023 AUS			Weight: 19.57 kg
Ref:		Joist Name: FJ3 Type: MSJ-360-45 Joists: FJ104, FJ105, FJ168, FJ169	Total Weight: 78.27 kg
			Laminations: 1

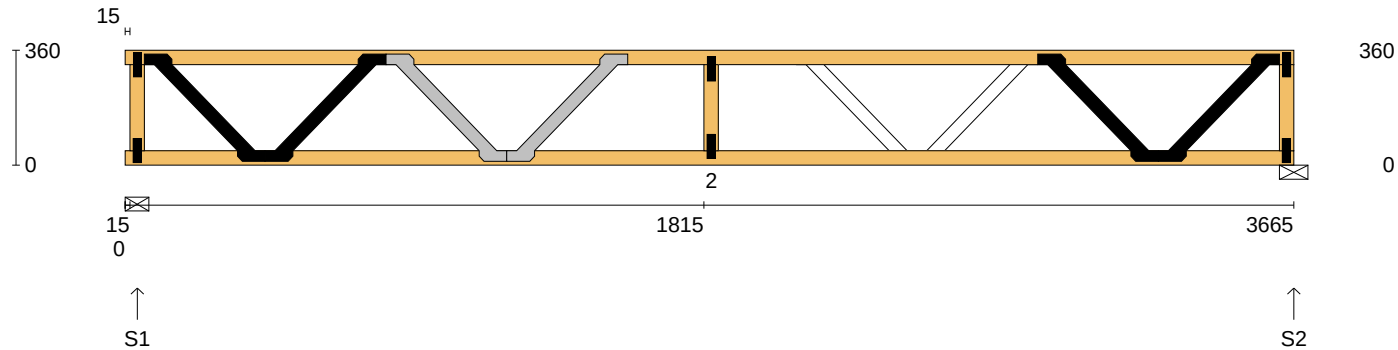

TIMBER / PLATES				
Member	Size	Plating	Restraint	
BC1	90x45-MGP10 H0 ADS	JD5	450	
TC1	90x45-MGP10 H0 ADS	JD5	300	
LEW1	90x45-MGP10 H0 ADS	JD5		
W1	90x45-MGP10 H0 ADS	JD5		
REW1	90x45-MGP10 H0 ADS	JD5		


Vertical Reactions at Supports

	S1	S2
1.35DL (kN)	1.27	0.86
1.2DL + 1.5LL (kN)	3.00	2.59

Joint	Nail Plate
TL1	25x75-MN
BL2	25x75-MN
T1	25x75-MN
B1	25x75-MN
TR1	25x75-MN
BR2	25x75-MN

Span: 3665	Floor Material: Particle (13.9 kg/m²)	Application: General Areas	All dimensions in millimetres. This drawing should be read in conjunction with Multinail Technical sheets. Wall plates must be placed at supports only.	Joey Meriales (TN-012-015)
Overhang: 0/0	Floor Covering: Std Carpet + Underlay (8 kg/m²)	Live Load: 1.5 kPa		Ver: Floor 1.14.3
Spacing: 450	Ceiling Material: Plaster 10mm Std Core (6.7 kg/m²)	Point Load: 1.8 kN		Date: 10/04/2026
Quantity: 4	Ceiling Fixing: Direct fix @ 450c	Design: AS 1720.1-2010		Page: 4 of 45

Site: LOT 735 15 LEICHHARDT AVE BURNSIDE VIC 3023 AUS Ref:	BB Truss & Timber Pty Ltd 41 Keilor Park Drive, Keilor Park 3042	Job No: K0964 Weight: 19.57 kg Total Weight: 78.27 kg Laminations: 1
	Joist Name: FJ3 Type: MSJ-360-45 Joists: FJ104, FJ105, FJ168, FJ169	

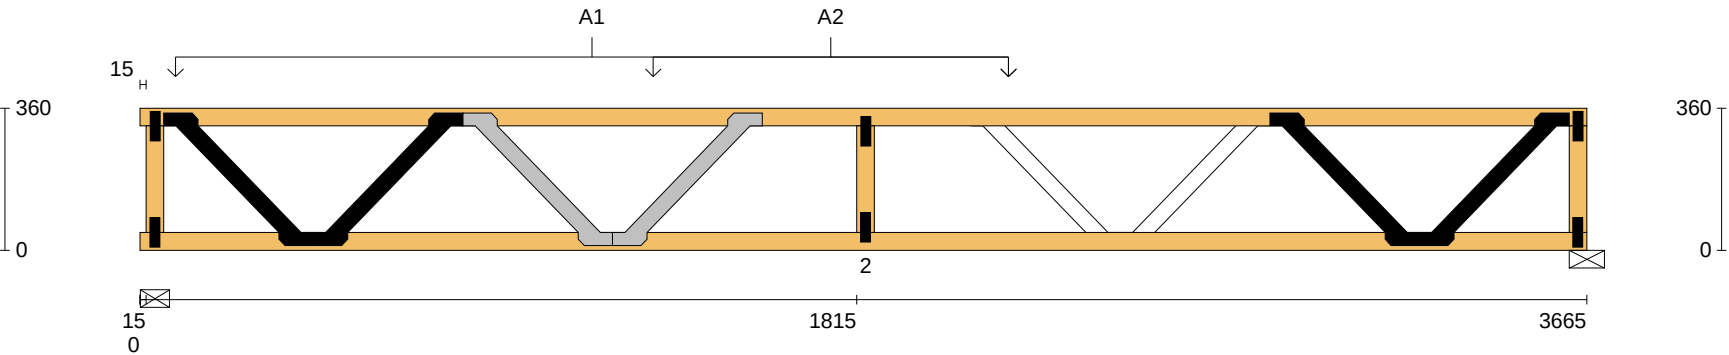


User Def. Load	A1	A2
	80.00 kg/m²	50.00 kg/m²

Applied Load	
DL	(kN)
LL	(kN)
WL Up	(kN)
WL Dn	(kN)

Span:	3665	Floor Material:	Particle (13.9 kg/m³)	Application:	General Areas	All dimensions in millimetres. This drawing should be read in conjunction with Multinail Technical sheets. Wall plates must be placed at supports only.	Joey Meriales (TN-012-015)
Overhang:	0/0	Floor Covering:	Std Carpet + Underlay (8 kg/m³)	Live Load:	1.5 kPa		Ver: Floor 1.14.3
Spacing:	450	Ceiling Material:	Plaster 10mm Std Core (6.7 kg/m³)	Point Load:	1.8 kN		Date: 10/04/2026
Quantity:	4	Ceiling Fixing:	Direct fix @ 450c	Design:	AS 1720.1-2010		Page: 5 of 45

Client: BSPOKE LUXURY HOMES PTY LTD	BB Truss & Timber Pty Ltd 41 Keilor Park Drive, Keilor Park 3042	Job No: K0964
Site: LOT 735 15 LEICHHARDT AVE BURNSIDE VIC 3023 AUS		Weight: 20.22 kg
Ref:	Joist Name: FJ4 Type: MSJ-400-45 Joists: FJ106, FJ107, FJ108	Total Weight: 60.66 kg
		Laminations: 1

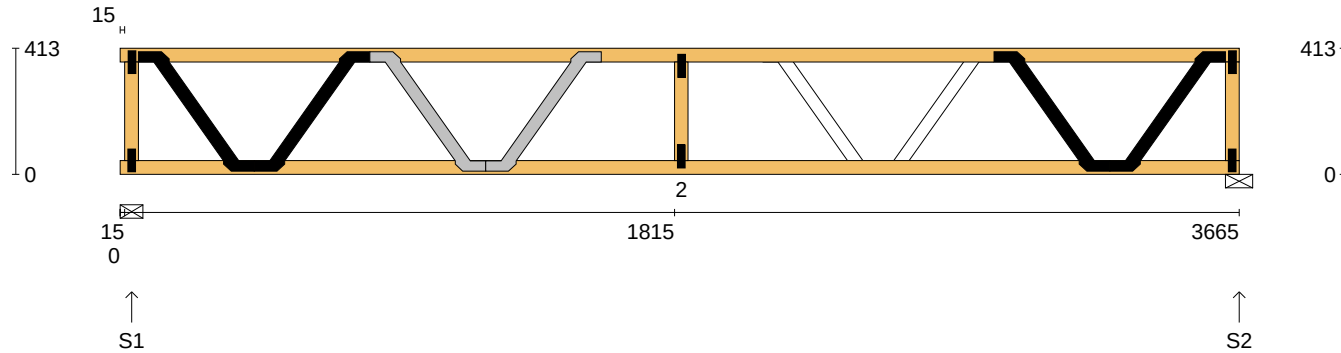

TIMBER / PLATES

Member	Size	Plating	Restraint
BC1	90x45-MGP10 H0 ADS	JD5	450
TC1	90x45-MGP10 H0 ADS	JD5	300
LEW1	90x45-MGP10 H0 ADS	JD5	
W1	90x45-MGP10 H0 ADS	JD5	
REW1	90x45-MGP10 H0 ADS	JD5	

Vertical Reactions at Supports


	S1	S2
1.35DL (kN)	1.14	0.74
1.2DL + 1.5LL (kN)	2.88	2.49

Joint Nail Plate

TL1	25x75-MN
BL2	25x75-MN
T1	25x75-MN
B1	25x75-MN
TR1	25x75-MN
BR2	25x75-MN

Span: 3665	Floor Material: Particle (13.9 kg/m²)	Application: General Areas	All dimensions in millimetres. This drawing should be read in conjunction with Multinail Technical sheets. Wall plates must be placed at supports only.	Joey Meriales (TN-012-015)
Overhang: 0/0	Floor Covering: Std Carpet + Underlay (8 kg/m²)	Live Load: 1.5 kPa		Ver: Floor 1.14.3
Spacing: 450	Ceiling Material: Plaster 10mm Std Core (6.7 kg/m²)	Point Load: 1.8 kN		Date: 10/04/2026
Quantity: 3	Ceiling Fixing: Direct fix @ 450c	Design: AS 1720.1-2010		Page: 6 of 45

Client: BSPOKE LUXURY HOMES PTY LTD	BB Truss & Timber Pty Ltd 41 Keilor Park Drive, Keilor Park 3042	Job No: K0964
Site: LOT 735 15 LEICHHARDT AVE BURNSIDE VIC 3023 AUS		Weight: 20.22 kg
Ref:	Joist Name: FJ4 Type: MSJ-400-45 Joists: FJ106, FJ107, FJ108	Total Weight: 60.66 kg
		Laminations: 1

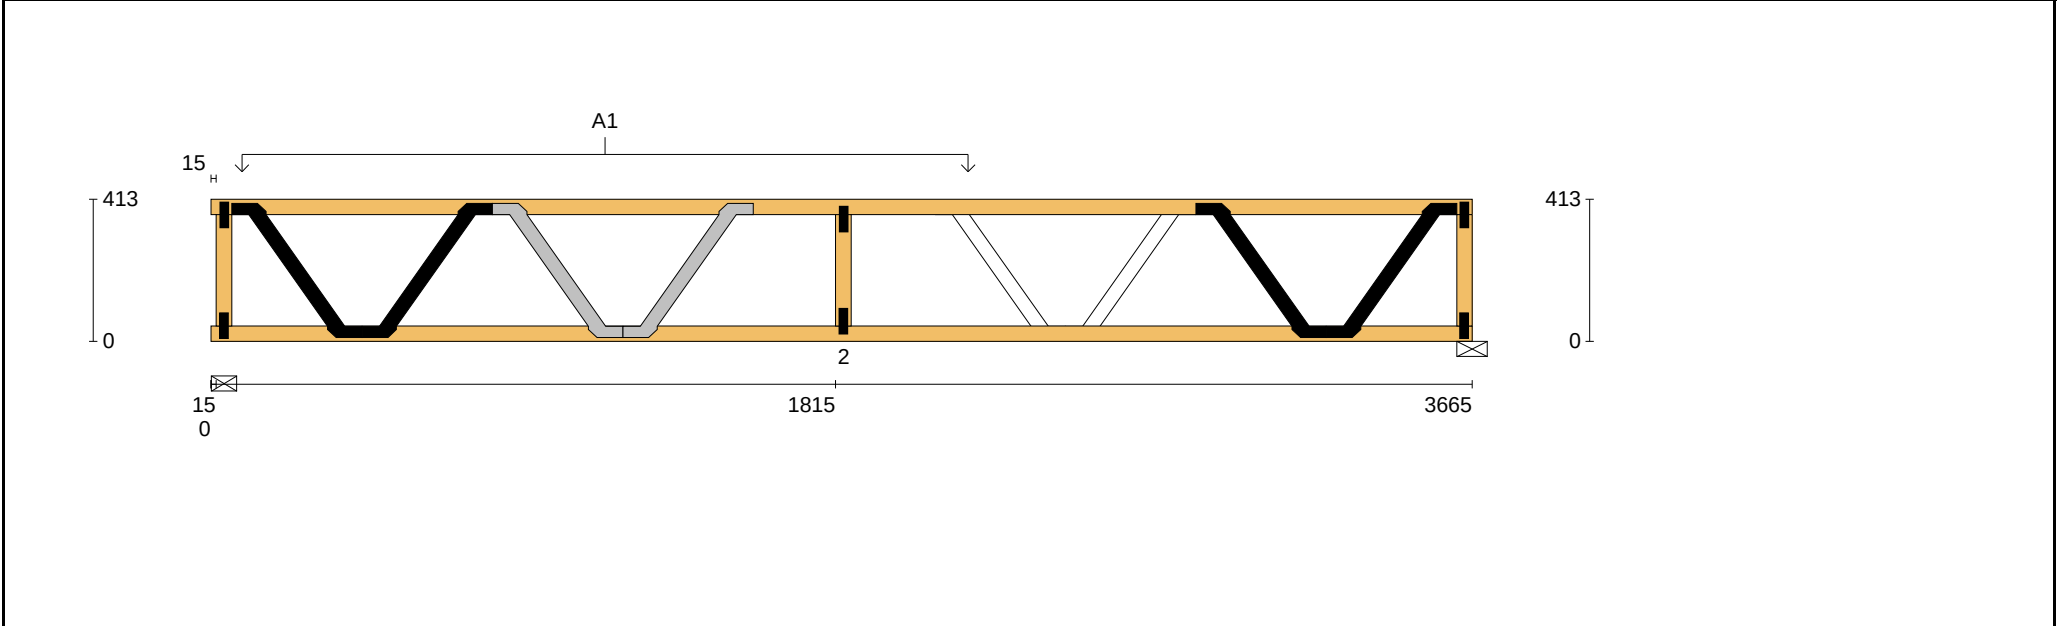


User Def. Load	A1 80.00 kg/m²
----------------	-------------------

Applied Load	
DL (kN)	
LL (kN)	
WL Up (kN)	
WL Dn (kN)	

Span:	3665	Floor Material:	Particle (13.9 kg/m³)	Application:	General Areas	All dimensions in millimetres. This drawing should be read in conjunction with Multinail Technical sheets. Wall plates must be placed at supports only.	Joey Meriales (TN-012-015)
Overhang:	0/0	Floor Covering:	Std Carpet + Underlay (8 kg/m³)	Live Load:	1.5 kPa		Ver: Floor 1.14.3
Spacing:	450	Ceiling Material:	Plaster 10mm Std Core (6.7 kg/m³)	Point Load:	1.8 kN		Date: 10/04/2026
Quantity:	3	Ceiling Fixing:	Direct fix @ 450c	Design:	AS 1720.1-2010		Page: 7 of 45

Client: BSPOKE LUXURY HOMES PTY LTD	BB Truss & Timber Pty Ltd 41 Keilor Park Drive, Keilor Park 3042	Job No: K0964
Site: LOT 735 15 LEICHHARDT AVE BURNSIDE VIC 3023 AUS		Weight: 20.53 kg
Ref:	Joist Name: FJ5 Type: MSJ-400-45 Joists: FJ109, FJ110, FJ111, FJ112, FJ113, FJ114, FJ115, FJ116, FJ117, FJ118, FJ119	Total Weight: 225.79 kg
		Laminations: 1

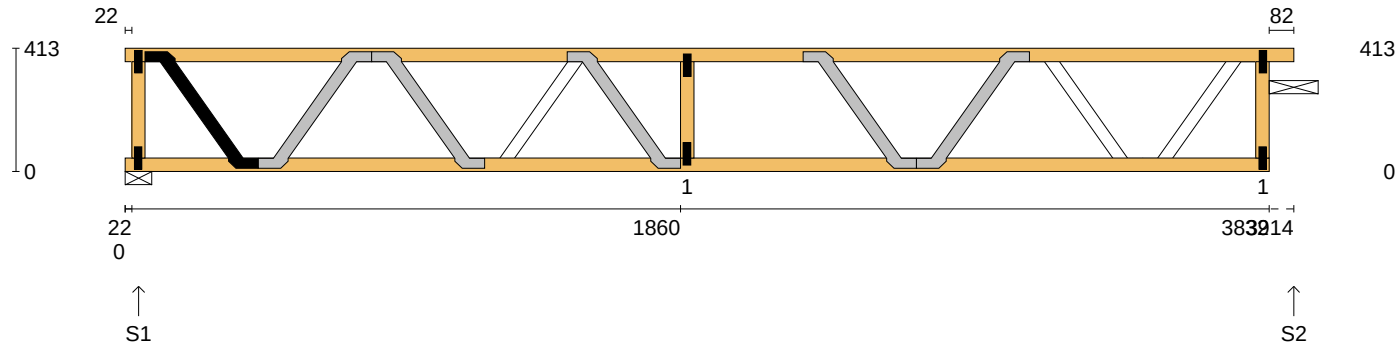

TIMBER / PLATES

Member	Size	Plating	Restraint
BC1	90x45-MGP10 H0 ADS	JD5	450
TC1	90x45-MGP10 H0 ADS	JD5	300
LEW1	90x45-MGP10 H0 ADS	JD5	
W1	90x45-MGP10 H0 ADS	JD5	
REW1	90x45-MGP10 H0 ADS	JD5	

Vertical Reactions at Supports


	S1	S2
1.35DL (kN)	0.46	0.47
1.2DL + 1.5LL (kN)	2.36	2.43

Joint Nail Plate

TL1	25x75-MN
BL2	25x75-MN
T1	25x75-MN
B1	25x75-MN
TR1	25x75-MN
BR2	25x75-MN

Span: 3914	Floor Material: Particle (13.9 kg/m²)	Application: General Areas	All dimensions in millimetres. This drawing should be read in conjunction with Multinail Technical sheets. Wall plates must be placed at supports only.	Joey Meriales (TN-012-015)
Overhang: 0/0	Floor Covering: Std Carpet + Underlay (8 kg/m²)	Live Load: 1.5 kPa		Ver: Floor 1.14.3
Spacing: 450	Ceiling Material: Plaster 10mm Std Core (6.7 kg/m²)	Point Load: 1.8 kN		Date: 10/04/2026
Quantity: 11	Ceiling Fixing: Direct fix @ 450c	Design: AS 1720.1-2010		Page: 8 of 45

Client: BSPOKE LUXURY HOMES PTY LTD	BB Truss & Timber Pty Ltd 41 Keilor Park Drive, Keilor Park 3042	Job No: K0964
Site: LOT 735 15 LEICHHARDT AVE BURNSIDE VIC 3023 AUS		Weight: 20.53 kg
Ref:	Joist Name: FJ6 Type: MSJ-400-45 Joists: FJ120	Total Weight: 20.53 kg
		Laminations: 1

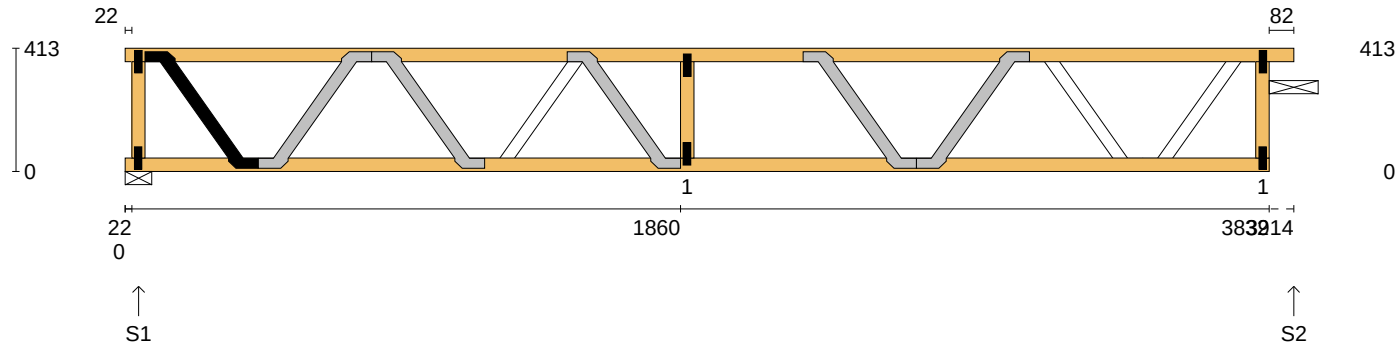

TIMBER / PLATES

Member	Size	Plating	Restraint
BC1	90x45-MGP10 H0 ADS	JD5	450
TC1	90x45-MGP10 H0 ADS	JD5	300
LEW1	90x45-MGP10 H0 ADS	JD5	
W1	90x45-MGP10 H0 ADS	JD5	
REW1	90x45-MGP10 H0 ADS	JD5	


Vertical Reactions at Supports

	S1	S2
1.35DL (kN)	0.46	0.47
1.2DL + 1.5LL (kN)	2.36	2.43


Joint Nail Plate

TL1	25x75-MN
BL2	25x75-MN
T1	25x75-MN
B1	25x75-MN
TR1	25x75-MN
BR2	25x75-MN

Span: 3914	Floor Material: Particle (13.9 kg/m²)	Application: General Areas	All dimensions in millimetres. This drawing should be read in conjunction with Multinail Technical sheets. Wall plates must be placed at supports only.	Joey Meriales (TN-012-015)
Overhang: 0/0	Floor Covering: Std Carpet + Underlay (8 kg/m²)	Live Load: 1.5 kPa		Ver: Floor 1.14.3
Spacing: 450	Ceiling Material: Plaster 10mm Std Core (6.7 kg/m²)	Point Load: 1.8 kN		Date: 10/04/2026
Quantity: 1	Ceiling Fixing: Direct fix @ 450c	Design: AS 1720.1-2010		Page: 9 of 45

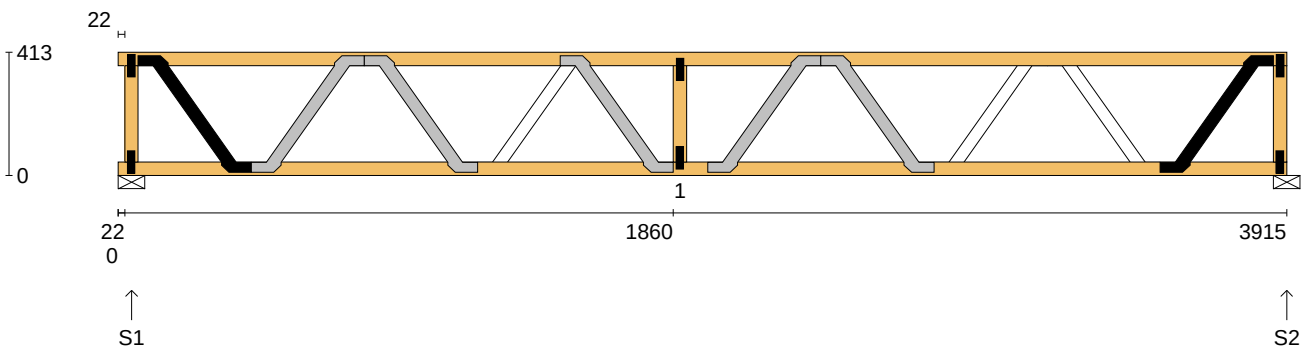		BB Truss & Timber Pty Ltd		Job No: K0964																								
Site: LOT 735 15 LEICHHARDT AVE BURNSIDE VIC 3023 AUS		41 Keilor Park Drive, Keilor Park 3042		Weight: 21.23 kg																								
Ref:		Joist Name: FJ7 Type: MSJ-400-45 Joists: FJ121		Total Weight: 21.23 kg																								
				Laminations: 1																								
				TIMBER / PLATES																								
				<table><thead><tr><th>Member</th><th>Size</th><th>Plating</th><th>Restraint</th></tr></thead><tbody><tr><td>BC1</td><td>90x45-MGP10 H0 ADS</td><td>JD5</td><td>450</td></tr><tr><td>TC1</td><td>90x45-MGP10 H0 ADS</td><td>JD5</td><td>300</td></tr><tr><td>LEW1</td><td>90x45-MGP10 H0 ADS</td><td>JD5</td><td></td></tr><tr><td>W1</td><td>90x45-MGP10 H0 ADS</td><td>JD5</td><td></td></tr><tr><td>REW1</td><td>90x45-MGP10 H0 ADS</td><td>JD5</td><td></td></tr></tbody></table>	Member	Size	Plating	Restraint	BC1	90x45-MGP10 H0 ADS	JD5	450	TC1	90x45-MGP10 H0 ADS	JD5	300	LEW1	90x45-MGP10 H0 ADS	JD5		W1	90x45-MGP10 H0 ADS	JD5		REW1	90x45-MGP10 H0 ADS	JD5	
Member	Size	Plating	Restraint																									
BC1	90x45-MGP10 H0 ADS	JD5	450																									
TC1	90x45-MGP10 H0 ADS	JD5	300																									
LEW1	90x45-MGP10 H0 ADS	JD5																										
W1	90x45-MGP10 H0 ADS	JD5																										
REW1	90x45-MGP10 H0 ADS	JD5																										
Vertical Reactions at Supports <table><thead><tr><th></th><th>S1</th><th>S2</th></tr></thead><tbody><tr><td>1.35DL (kN)</td><td>0.54</td><td>0.54</td></tr><tr><td>1.2DL + 1.5LL (kN)</td><td>2.48</td><td>2.42</td></tr></tbody></table>					S1	S2	1.35DL (kN)	0.54	0.54	1.2DL + 1.5LL (kN)	2.48	2.42	<table><thead><tr><th>Joint</th><th>Nail Plate</th></tr></thead><tbody><tr><td>TL1</td><td>25x75-MN</td></tr><tr><td>BL2</td><td>25x75-MN</td></tr><tr><td>T1</td><td>25x75-MN</td></tr><tr><td>B1</td><td>25x75-MN</td></tr><tr><td>TR1</td><td>25x75-MN</td></tr><tr><td>BR2</td><td>25x75-MN</td></tr></tbody></table>		Joint	Nail Plate	TL1	25x75-MN	BL2	25x75-MN	T1	25x75-MN	B1	25x75-MN	TR1	25x75-MN	BR2	25x75-MN
					S1	S2																						
1.35DL (kN)	0.54	0.54																										
1.2DL + 1.5LL (kN)	2.48	2.42																										
Joint	Nail Plate																											
TL1	25x75-MN																											
BL2	25x75-MN																											
T1	25x75-MN																											
B1	25x75-MN																											
TR1	25x75-MN																											
BR2	25x75-MN																											
Span: 3915		Floor Material: Particle (13.9 kg/m³)		Application: General Areas																								
Overhang: 0/0		Floor Covering: Std Carpet + Underlay (8 kg/m²)		Live Load: 1.5 kPa																								
Spacing: 450		Ceiling Material: Plaster 10mm Std Core (6.7 kg/m²)		Point Load: 1.8 kN																								
Quantity: 1		Ceiling Fixing: Direct fix @ 450c		Design: AS 1720.1-2010																								
All dimensions in millimetres. This drawing should be read in conjunction with Multinail Technical sheets. Wall plates must be placed at supports only.																												
																												
				Joey Meriales (TN-012-015)																								
				Ver: Floor 1.14.3																								
				Date: 10/04/2026																								
				Page: 10 of 45																								


		BB Truss & Timber Pty Ltd 41 Keilor Park Drive, Keilor Park 3042	Job No: K0964
Site: LOT 735 15 LEICHHARDT AVE BURNSIDE VIC 3023 AUS			Weight: 21.23 kg
Ref:		Joist Name: FJ7 Type: MSJ-400-45 Joists: FJ121	Total Weight: 21.23 kg
			Laminations: 1

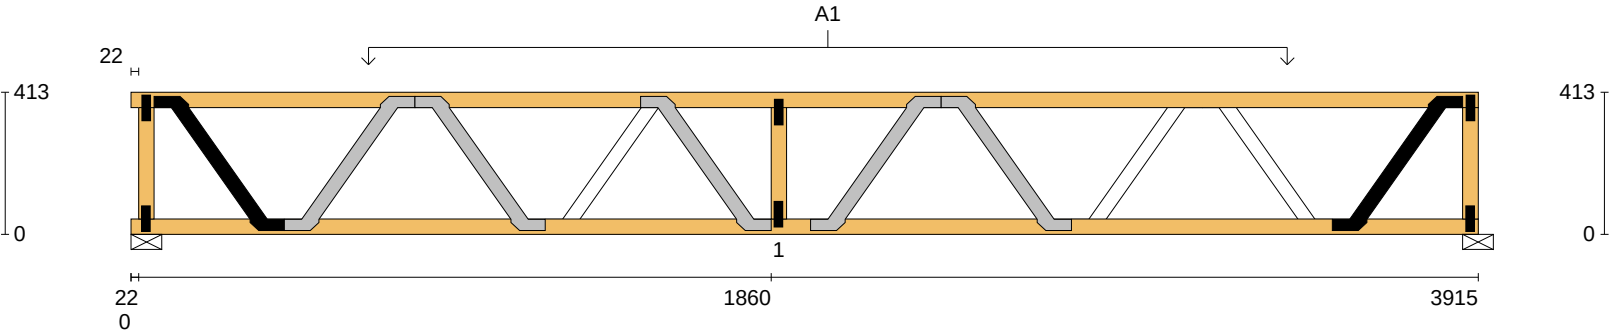



User Def. Load A1
8.70 kg/m²

Applied Load
DL (kN)
LL (kN)
WL Up (kN)
WL Dn (kN)


Span:	3915	Floor Material:	Particle (13.9 kg/m²)	Application:	General Areas	All dimensions in millimetres. This drawing should be read in conjunction with Multinail Technical sheets. Wall plates must be placed at supports only.	Joey Meriales (TN-012-015)
Overhang:	0/0	Floor Covering:	Std Carpet + Underlay (8 kg/m²)	Live Load:	1.5 kPa		Ver: Floor 1.14.3
Spacing:	450	Ceiling Material:	Plaster 10mm Std Core (6.7 kg/m²)	Point Load:	1.8 kN		Date: 10/04/2026
Quantity:	1	Ceiling Fixing:	Direct fix @ 450c	Design:	AS 1720.1-2010		Page: 11 of 45

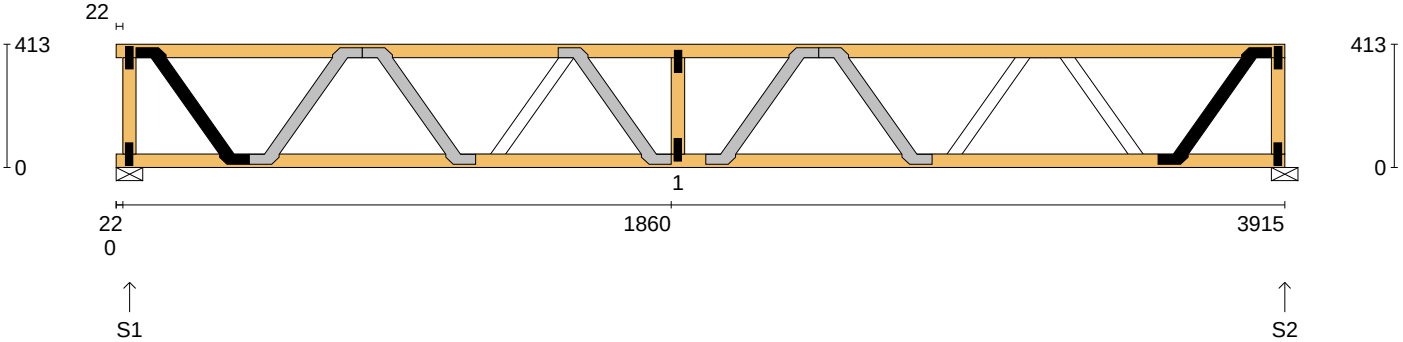		BB Truss & Timber Pty Ltd		Job No: K0964																								
Site: LOT 735 15 LEICHHARDT AVE BURNSIDE VIC 3023 AUS		41 Keilor Park Drive, Keilor Park 3042		Weight: 21.23 kg																								
Ref:		Joist Name: FJ7 Type: MSJ-400-45		Total Weight: 212.32 kg																								
		Joists: FJ122, FJ123, FJ124, FJ125, FJ126, FJ127, FJ128, FJ129, FJ130, FJ198		Laminations: 1																								
				TIMBER / PLATES																								
				<table><thead><tr><th>Member</th><th>Size</th><th>Plating</th><th>Restraint</th></tr></thead><tbody><tr><td>BC1</td><td>90x45-MGP10 H0 ADS</td><td>JD5</td><td>450</td></tr><tr><td>TC1</td><td>90x45-MGP10 H0 ADS</td><td>JD5</td><td>300</td></tr><tr><td>LEW1</td><td>90x45-MGP10 H0 ADS</td><td>JD5</td><td></td></tr><tr><td>W1</td><td>90x45-MGP10 H0 ADS</td><td>JD5</td><td></td></tr><tr><td>REW1</td><td>90x45-MGP10 H0 ADS</td><td>JD5</td><td></td></tr></tbody></table>	Member	Size	Plating	Restraint	BC1	90x45-MGP10 H0 ADS	JD5	450	TC1	90x45-MGP10 H0 ADS	JD5	300	LEW1	90x45-MGP10 H0 ADS	JD5		W1	90x45-MGP10 H0 ADS	JD5		REW1	90x45-MGP10 H0 ADS	JD5	
Member	Size	Plating	Restraint																									
BC1	90x45-MGP10 H0 ADS	JD5	450																									
TC1	90x45-MGP10 H0 ADS	JD5	300																									
LEW1	90x45-MGP10 H0 ADS	JD5																										
W1	90x45-MGP10 H0 ADS	JD5																										
REW1	90x45-MGP10 H0 ADS	JD5																										
Vertical Reactions at Supports <table><thead><tr><th></th><th>S1</th><th>S2</th></tr></thead><tbody><tr><td>1.35DL (kN)</td><td>0.48</td><td>0.46</td></tr><tr><td>1.2DL + 1.5LL (kN)</td><td>2.42</td><td>2.36</td></tr></tbody></table>					S1	S2	1.35DL (kN)	0.48	0.46	1.2DL + 1.5LL (kN)	2.42	2.36	<table><thead><tr><th>Joint</th><th>Nail Plate</th></tr></thead><tbody><tr><td>TL1</td><td>25x75-MN</td></tr><tr><td>BL2</td><td>25x75-MN</td></tr><tr><td>T1</td><td>25x75-MN</td></tr><tr><td>B1</td><td>25x75-MN</td></tr><tr><td>TR1</td><td>25x75-MN</td></tr><tr><td>BR2</td><td>25x75-MN</td></tr></tbody></table>		Joint	Nail Plate	TL1	25x75-MN	BL2	25x75-MN	T1	25x75-MN	B1	25x75-MN	TR1	25x75-MN	BR2	25x75-MN
					S1	S2																						
1.35DL (kN)	0.48	0.46																										
1.2DL + 1.5LL (kN)	2.42	2.36																										
Joint	Nail Plate																											
TL1	25x75-MN																											
BL2	25x75-MN																											
T1	25x75-MN																											
B1	25x75-MN																											
TR1	25x75-MN																											
BR2	25x75-MN																											
Span: 3915		Floor Material: Particle (13.9 kg/m²)		Application: General Areas		All dimensions in millimetres. This drawing should be read in conjunction with Multinail Technical sheets. Wall plates must be placed at supports only.		Joey Meriales (TN-012-015)																				
Overhang: 0/0		Floor Covering: Std Carpet + Underlay (8 kg/m²)		Live Load: 1.5 kPa				Ver: Floor 1.14.3																				
Spacing: 450		Ceiling Material: Plaster 10mm Std Core (6.7 kg/m²)		Point Load: 1.8 kN				Date: 10/04/2026																				
Quantity: 10		Ceiling Fixing: Direct fix @ 450c		Design: AS 1720.1-2010				Page: 12 of 45																				

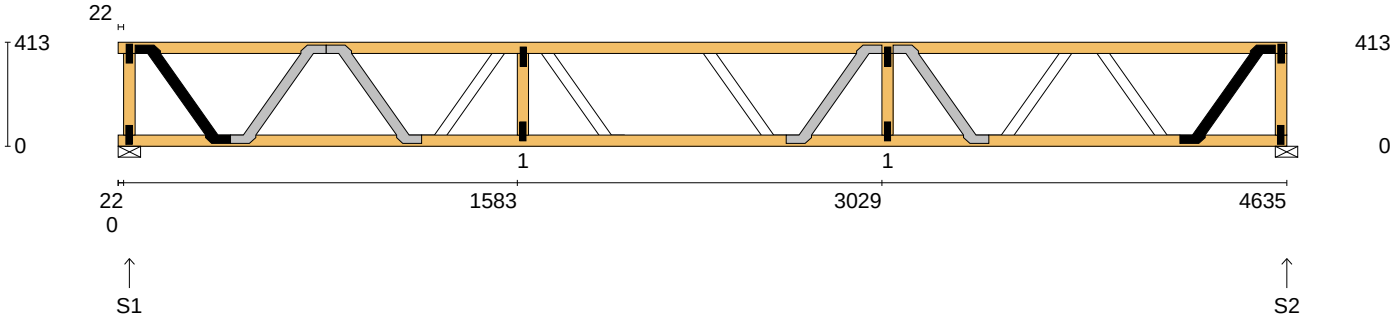		BB Truss & Timber Pty Ltd		Job No: K0964																												
Site: LOT 735 15 LEICHHARDT AVE BURNSIDE VIC 3023 AUS		41 Keilor Park Drive, Keilor Park 3042		Weight: 25.14 kg																												
Ref:		Joist Name: FJ8 Type: MSJ-400-45		Total Weight: 100.55 kg																												
		Joists: FJ131, FJ132, FJ133, FJ134		Laminations: 1																												
				TIMBER / PLATES																												
				<table><thead><tr><th>Member</th><th>Size</th><th>Plating</th><th>Restraint</th></tr></thead><tbody><tr><td>BC1</td><td>90x45-MGP10 H0 ADS</td><td>JD5</td><td>450</td></tr><tr><td>TC1</td><td>90x45-MGP10 H0 ADS</td><td>JD5</td><td>300</td></tr><tr><td>LEW1</td><td>90x45-MGP10 H0 ADS</td><td>JD5</td><td></td></tr><tr><td>W1</td><td>90x45-MGP10 H0 ADS</td><td>JD5</td><td></td></tr><tr><td>W2</td><td>90x45-MGP10 H0 ADS</td><td>JD5</td><td></td></tr><tr><td>REW1</td><td>90x45-MGP10 H0 ADS</td><td>JD5</td><td></td></tr></tbody></table>	Member	Size	Plating	Restraint	BC1	90x45-MGP10 H0 ADS	JD5	450	TC1	90x45-MGP10 H0 ADS	JD5	300	LEW1	90x45-MGP10 H0 ADS	JD5		W1	90x45-MGP10 H0 ADS	JD5		W2	90x45-MGP10 H0 ADS	JD5		REW1	90x45-MGP10 H0 ADS	JD5	
Member	Size	Plating	Restraint																													
BC1	90x45-MGP10 H0 ADS	JD5	450																													
TC1	90x45-MGP10 H0 ADS	JD5	300																													
LEW1	90x45-MGP10 H0 ADS	JD5																														
W1	90x45-MGP10 H0 ADS	JD5																														
W2	90x45-MGP10 H0 ADS	JD5																														
REW1	90x45-MGP10 H0 ADS	JD5																														
Vertical Reactions at Supports <table><thead><tr><th></th><th>S1</th><th>S2</th></tr></thead><tbody><tr><td>1.35DL (kN)</td><td>0.56</td><td>0.55</td></tr><tr><td>1.2DL + 1.5LL (kN)</td><td>2.86</td><td>2.80</td></tr></tbody></table>					S1	S2	1.35DL (kN)	0.56	0.55	1.2DL + 1.5LL (kN)	2.86	2.80	<table><thead><tr><th>Joint</th><th>Nail Plate</th></tr></thead><tbody><tr><td>TL1</td><td>25x75-MN</td></tr><tr><td>BL2</td><td>25x75-MN</td></tr><tr><td>T1</td><td>25x75-MN</td></tr><tr><td>B1</td><td>25x75-MN</td></tr><tr><td>T2</td><td>25x75-MN</td></tr><tr><td>B2</td><td>25x75-MN</td></tr><tr><td>TR1</td><td>25x75-MN</td></tr><tr><td>BR2</td><td>25x75-MN</td></tr></tbody></table>		Joint	Nail Plate	TL1	25x75-MN	BL2	25x75-MN	T1	25x75-MN	B1	25x75-MN	T2	25x75-MN	B2	25x75-MN	TR1	25x75-MN	BR2	25x75-MN
					S1	S2																										
1.35DL (kN)	0.56	0.55																														
1.2DL + 1.5LL (kN)	2.86	2.80																														
Joint	Nail Plate																															
TL1	25x75-MN																															
BL2	25x75-MN																															
T1	25x75-MN																															
B1	25x75-MN																															
T2	25x75-MN																															
B2	25x75-MN																															
TR1	25x75-MN																															
BR2	25x75-MN																															
Span: 4635		Floor Material: Particle (13.9 kg/m²)		Application: General Areas		All dimensions in millimetres. This drawing should be read in conjunction with Multinail Technical sheets. Wall plates must be placed at supports only.		Joey Meriales (TN-012-015)																								
Overhang: 0/0		Floor Covering: Std Carpet + Underlay (8 kg/m²)		Live Load: 1.5 kPa				Ver: Floor 1.14.3																								
Spacing: 450		Ceiling Material: Plaster 10mm Std Core (6.7 kg/m²)		Point Load: 1.8 kN				Date: 10/04/2026																								
Quantity: 4		Ceiling Fixing: Direct fix @ 450c		Design: AS 1720.1-2010				Page: 13 of 45																								

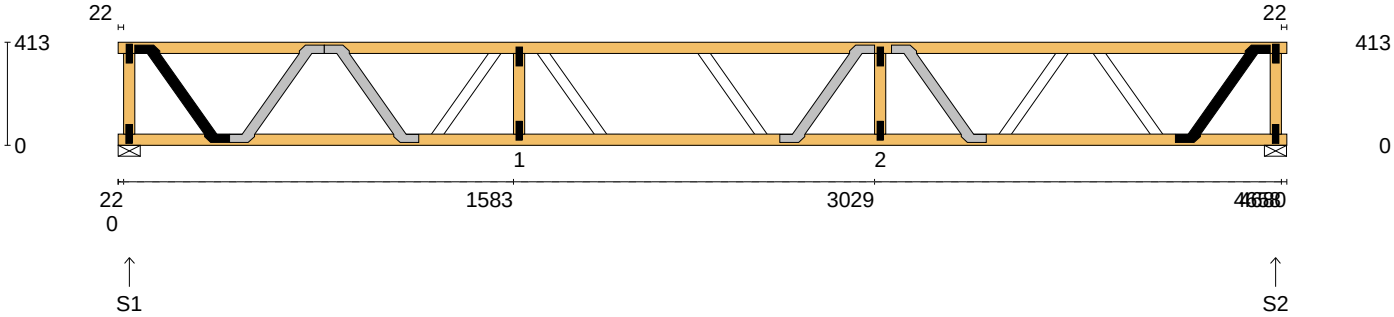		BB Truss & Timber Pty Ltd		Job No: K0964																												
Site: LOT 735 15 LEICHHARDT AVE BURNSIDE VIC 3023 AUS		41 Keilor Park Drive, Keilor Park 3042		Weight: 25.32 kg																												
Ref:		Joist Name: FJ9 Type: MSJ-400-45 Joists: FJ135, FJ136, FJ137, FJ138, FJ139		Total Weight: 126.60 kg																												
				Laminations: 1																												
				TIMBER / PLATES																												
				<table><tr><th>Member</th><th>Size</th><th>Plating</th><th>Restraint</th></tr><tr><td>BC1</td><td>90x45-MGP10 H0 ADS</td><td>JD5</td><td>450</td></tr><tr><td>TC1</td><td>90x45-MGP10 H0 ADS</td><td>JD5</td><td>300</td></tr><tr><td>LEW1</td><td>90x45-MGP10 H0 ADS</td><td>JD5</td><td></td></tr><tr><td>W1</td><td>90x45-MGP10 H0 ADS</td><td>JD5</td><td></td></tr><tr><td>W2</td><td>90x45-MGP10 H0 ADS</td><td>JD5</td><td></td></tr><tr><td>REW1</td><td>90x45-MGP10 H0 ADS</td><td>JD5</td><td></td></tr></table>		Member	Size	Plating	Restraint	BC1	90x45-MGP10 H0 ADS	JD5	450	TC1	90x45-MGP10 H0 ADS	JD5	300	LEW1	90x45-MGP10 H0 ADS	JD5		W1	90x45-MGP10 H0 ADS	JD5		W2	90x45-MGP10 H0 ADS	JD5		REW1	90x45-MGP10 H0 ADS	JD5
Member	Size	Plating	Restraint																													
BC1	90x45-MGP10 H0 ADS	JD5	450																													
TC1	90x45-MGP10 H0 ADS	JD5	300																													
LEW1	90x45-MGP10 H0 ADS	JD5																														
W1	90x45-MGP10 H0 ADS	JD5																														
W2	90x45-MGP10 H0 ADS	JD5																														
REW1	90x45-MGP10 H0 ADS	JD5																														
Vertical Reactions at Supports <table><tr><th></th><th>S1</th><th>S2</th></tr><tr><td>1.35DL (kN)</td><td>0.57</td><td>0.57</td></tr><tr><td>1.2DL + 1.5LL (kN)</td><td>2.87</td><td>2.87</td></tr></table>					S1	S2	1.35DL (kN)	0.57	0.57	1.2DL + 1.5LL (kN)	2.87	2.87	<table><tr><th>Joint</th><th>Nail Plate</th></tr><tr><td>TL1</td><td>25x75-MN</td></tr><tr><td>BL2</td><td>25x75-MN</td></tr><tr><td>T1</td><td>25x75-MN</td></tr><tr><td>B1</td><td>25x75-MN</td></tr><tr><td>T2</td><td>25x75-MN</td></tr><tr><td>B2</td><td>25x75-MN</td></tr><tr><td>TR1</td><td>25x75-MN</td></tr><tr><td>BR2</td><td>25x75-MN</td></tr></table>		Joint	Nail Plate	TL1	25x75-MN	BL2	25x75-MN	T1	25x75-MN	B1	25x75-MN	T2	25x75-MN	B2	25x75-MN	TR1	25x75-MN	BR2	25x75-MN
					S1	S2																										
1.35DL (kN)	0.57	0.57																														
1.2DL + 1.5LL (kN)	2.87	2.87																														
Joint	Nail Plate																															
TL1	25x75-MN																															
BL2	25x75-MN																															
T1	25x75-MN																															
B1	25x75-MN																															
T2	25x75-MN																															
B2	25x75-MN																															
TR1	25x75-MN																															
BR2	25x75-MN																															
Span:	4680	Floor Material:	Particle (13.9 kg/m²)	Application:	General Areas	All dimensions in millimetres. This drawing should be read in conjunction with Multinail Technical sheets. Wall plates must be placed at supports only.	Joey Meriales (TN-012-015)																									
Overhang:	0/0	Floor Covering:	Std Carpet + Underlay (8 kg/m²)	Live Load:	1.5 kPa		Ver: Floor 1.14.3																									
Spacing:	450	Ceiling Material:	Plaster 10mm Std Core (6.7 kg/m²)	Point Load:	1.8 kN		Date: 10/04/2026																									
Quantity:	5	Ceiling Fixing:	Direct fix @ 450c	Design:	AS 1720.1-2010		Page: 14 of 45																									

Client: BSPOKE LUXURY HOMES PTY LTD	BB Truss & Timber Pty Ltd 41 Keilor Park Drive, Keilor Park 3042	Job No: K0964
Site: LOT 735 15 LEICHHARDT AVE BURNSIDE VIC 3023 AUS		Weight: 21.27 kg
Ref:	Joist Name: FJ10 Type: MSJ-400-45 Joists: FJ140	Total Weight: 21.27 kg
		Laminations: 1

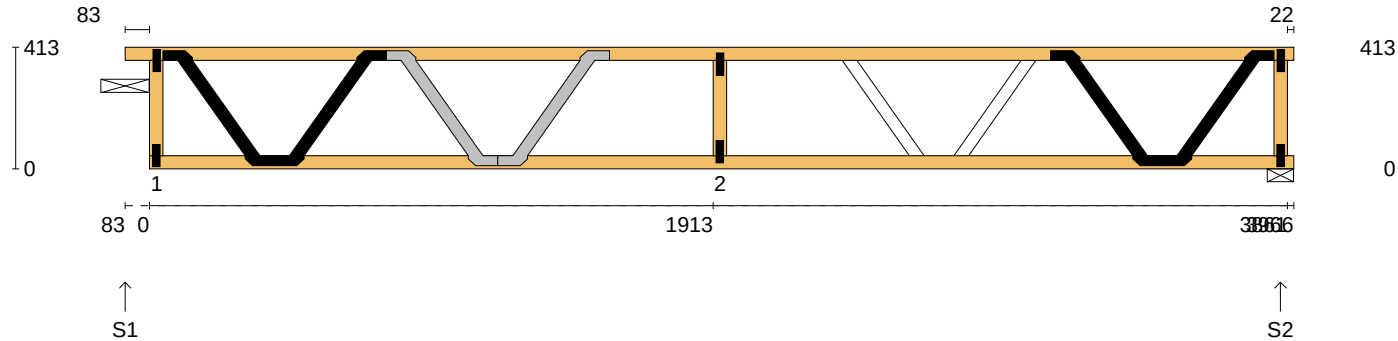

TIMBER / PLATES

Member	Size	Plating	Restraint
TC1	90x45-MGP10 H0 ADS	JD5	300
BC1	90x45-MGP10 H0 ADS	JD5	450
LEW1	90x45-MGP10 H0 ADS	JD5	
W1	90x45-MGP10 H0 ADS	JD5	
REW1	90x45-MGP10 H0 ADS	JD5	

Vertical Reactions at Supports


	S1	S2
1.35DL (kN)	1.18	1.42
1.2DL + 1.5LL (kN)	3.09	3.24

Joint Nail Plate

TL1	25x75-MN
BL2	25x75-MN
T1	25x75-MN
B1	25x75-MN
TR1	25x75-MN
BR2	25x75-MN

Span: 3966	Floor Material: Particle (13.9 kg/m²)	Application: General Areas	All dimensions in millimetres. This drawing should be read in conjunction with Multinail Technical sheets. Wall plates must be placed at supports only.	Joey Meriales (TN-012-015)
Overhang: 0/0	Floor Covering: Std Carpet + Underlay (8 kg/m²)	Live Load: 1.5 kPa		Ver: Floor 1.14.3
Spacing: 450	Ceiling Material: Plaster 10mm Std Core (6.7 kg/m²)	Point Load: 1.8 kN		Date: 10/04/2026
Quantity: 1	Ceiling Fixing: Direct fix @ 450c	Design: AS 1720.1-2010		Page: 15 of 45

Client: BSPOKE LUXURY HOMES PTY LTD	BB Truss & Timber Pty Ltd 41 Keilor Park Drive, Keilor Park 3042	Job No: K0964
Site: LOT 735 15 LEICHHARDT AVE BURNSIDE VIC 3023 AUS		Weight: 21.27 kg
Ref:	Joist Name: FJ10 Type: MSJ-400-45 Joists: FJ140	Total Weight: 21.27 kg
		Laminations: 1

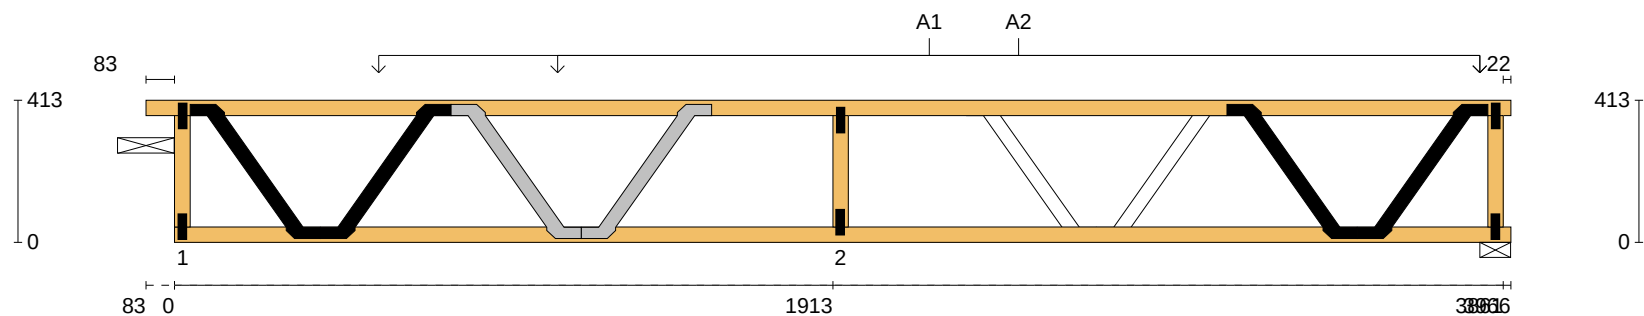


User Def. Load	A1	A2
	80.00 kg/m ²	8.70 kg/m ²

Applied Load
DL (kN)
LL (kN)
WL Up (kN)
WL Dn (kN)

Span: 3966	Floor Material: Particle (13.9 kg/m²)	Application: General Areas	All dimensions in millimetres. This drawing should be read in conjunction with Multinail Technical sheets. Wall plates must be placed at supports only.	Joey Meriales (TN-012-015)
Overhang: 0/0	Floor Covering: Std Carpet + Underlay (8 kg/m²)	Live Load: 1.5 kPa		Ver: Floor 1.14.3
Spacing: 450	Ceiling Material: Plaster 10mm Std Core (6.7 kg/m²)	Point Load: 1.8 kN		Date: 10/04/2026
Quantity: 1	Ceiling Fixing: Direct fix @ 450c	Design: AS 1720.1-2010		Page: 16 of 45

Client: BSPOKE LUXURY HOMES PTY LTD	BB Truss & Timber Pty Ltd 41 Keilor Park Drive, Keilor Park 3042	Job No: K0964
Site: LOT 735 15 LEICHHARDT AVE BURNSIDE VIC 3023 AUS		Weight: 20.62 kg
Ref:	Joist Name: FJ11 Type: MSJ-360-45 Joists: FJ141, FJ142, FJ143, FJ170	Total Weight: 82.47 kg
		Laminations: 1

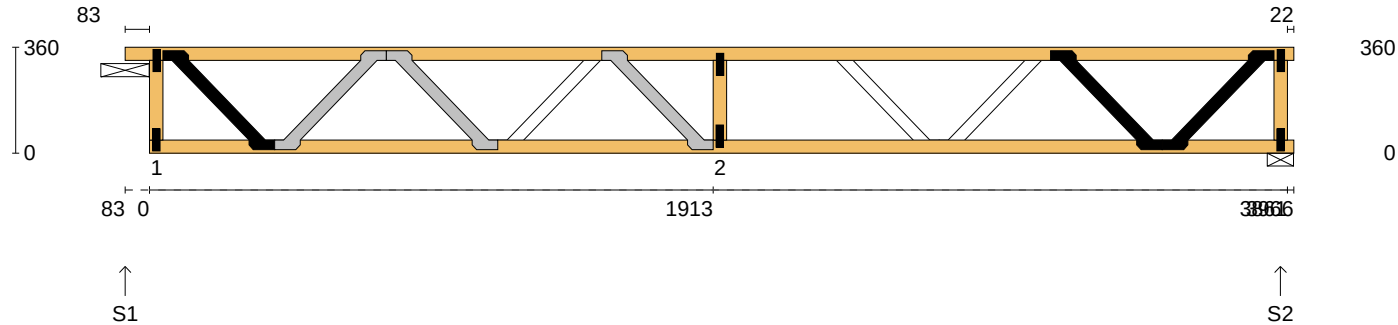

TIMBER / PLATES

Member	Size	Plating	Restraint
TC1	90x45-MGP10 H0 ADS	JD5	300
BC1	90x45-MGP10 H0 ADS	JD5	450
LEW1	90x45-MGP10 H0 ADS	JD5	
W1	90x45-MGP10 H0 ADS	JD5	
REW1	90x45-MGP10 H0 ADS	JD5	

Vertical Reactions at Supports


	S1	S2
1.35DL (kN)	1.03	1.67
1.2DL + 1.5LL (kN)	2.95	3.46

Joint Nail Plate

TL1	25x75-MN
BL2	25x75-MN
T1	25x75-MN
B1	25x75-MN
TR1	25x75-MN
BR2	25x75-MN

Span: 3966	Floor Material: Particle (13.9 kg/m²)	Application: General Areas	All dimensions in millimetres. This drawing should be read in conjunction with Multinail Technical sheets. Wall plates must be placed at supports only.	Joey Meriales (TN-012-015)
Overhang: 0/0	Floor Covering: Std Carpet + Underlay (8 kg/m²)	Live Load: 1.5 kPa		Ver: Floor 1.14.3
Spacing: 450	Ceiling Material: Plaster 10mm Std Core (6.7 kg/m²)	Point Load: 1.8 kN		Date: 10/04/2026
Quantity: 4	Ceiling Fixing: Direct fix @ 450c	Design: AS 1720.1-2010		Page: 17 of 45

Client: BSPOKE LUXURY HOMES PTY LTD	BB Truss & Timber Pty Ltd 41 Keilor Park Drive, Keilor Park 3042	Job No: K0964
Site: LOT 735 15 LEICHHARDT AVE BURNSIDE VIC 3023 AUS		Weight: 20.62 kg
Ref:	Joist Name: FJ11 Type: MSJ-360-45 Joists: FJ141, FJ142, FJ143, FJ170	Total Weight: 82.47 kg
		Laminations: 1

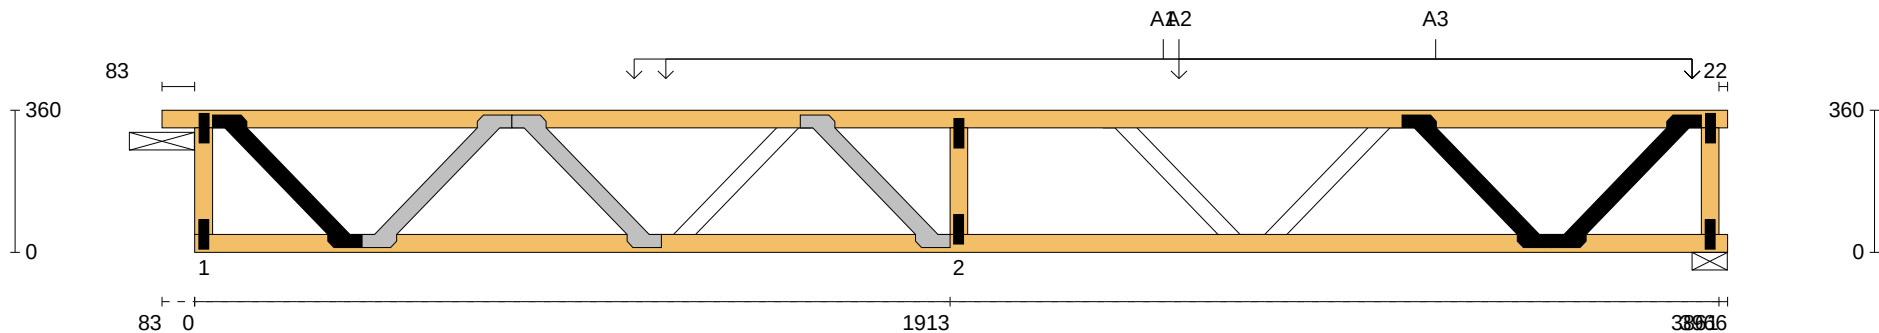


User Def. Load	A1	A2	A3
	8.70 kg/m ²	80.00 kg/m ²	50.00 kg/m ²

Applied Load	
DL	(kN)
LL	(kN)
WL Up	(kN)
WL Dn	(kN)

Span: 3966	Floor Material: Particle (13.9 kg/m²)	Application: General Areas	All dimensions in millimetres. This drawing should be read in conjunction with Multinail Technical sheets. Wall plates must be placed at supports only.	Joey Meriales (TN-012-015)
Overhang: 0/0	Floor Covering: Std Carpet + Underlay (8 kg/m²)	Live Load: 1.5 kPa		Ver: Floor 1.14.3
Spacing: 450	Ceiling Material: Plaster 10mm Std Core (6.7 kg/m²)	Point Load: 1.8 kN		Date: 10/04/2026
Quantity: 4	Ceiling Fixing: Direct fix @ 450c	Design: AS 1720.1-2010		Page: 18 of 45

Client: BSPOKE LUXURY HOMES PTY LTD	BB Truss & Timber Pty Ltd 41 Keilor Park Drive, Keilor Park 3042	Job No: K0964
Site: LOT 735 15 LEICHHARDT AVE BURNSIDE VIC 3023 AUS		Weight: 20.47 kg
Ref:	Joist Name: FJ12 Type: MSJ-400-45 Joists: FJ144, FJ145, FJ146, FJ147, FJ148, FJ149, FJ150	Total Weight: 143.27 kg
		Laminations: 1

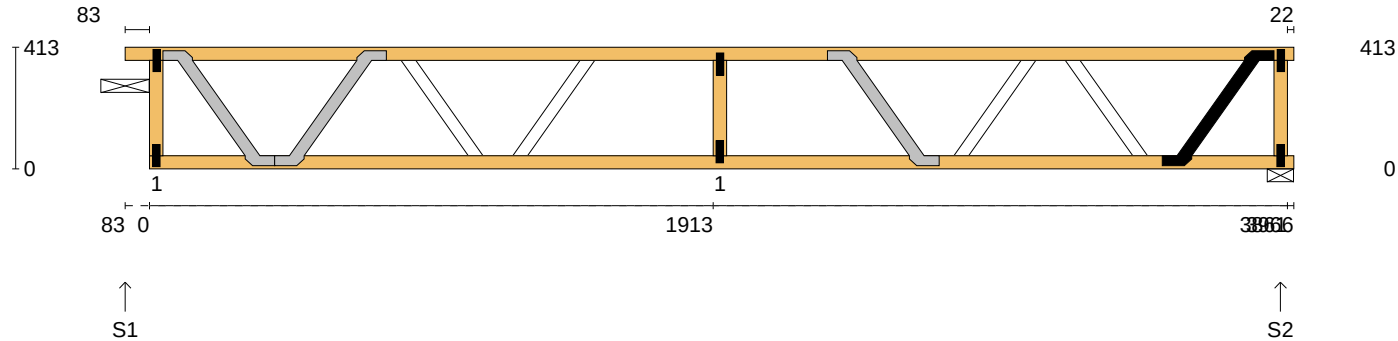

TIMBER / PLATES

Member	Size	Plating	Restraint
TC1	90x45-MGP10 H0 ADS	JD5	300
BC1	90x45-MGP10 H0 ADS	JD5	450
LEW1	90x45-MGP10 H0 ADS	JD5	
W1	90x45-MGP10 H0 ADS	JD5	
REW1	90x45-MGP10 H0 ADS	JD5	

Vertical Reactions at Supports


	S1	S2
1.35DL (kN)	0.53	0.56
1.2DL + 1.5LL (kN)	2.51	2.47

Joint Nail Plate

TL1	25x75-MN
BL2	25x75-MN
T1	25x75-MN
B1	25x75-MN
TR1	25x75-MN
BR2	25x75-MN

Span: 3966	Floor Material: Particle (13.9 kg/m²)	Application: General Areas	All dimensions in millimetres. This drawing should be read in conjunction with Multinail Technical sheets. Wall plates must be placed at supports only.	Joey Meriales (TN-012-015)
Overhang: 0/0	Floor Covering: Std Carpet + Underlay (8 kg/m²)	Live Load: 1.5 kPa		Ver: Floor 1.14.3
Spacing: 450	Ceiling Material: Plaster 10mm Std Core (6.7 kg/m²)	Point Load: 1.8 kN		Date: 10/04/2026
Quantity: 7	Ceiling Fixing: Direct fix @ 450c	Design: AS 1720.1-2010		Page: 19 of 45

Client: BSPOKE LUXURY HOMES PTY LTD	BB Truss & Timber Pty Ltd 41 Keilor Park Drive, Keilor Park 3042	Job No: K0964
Site: LOT 735 15 LEICHHARDT AVE BURNSIDE VIC 3023 AUS		Weight: 20.47 kg
Ref:	Joist Name: FJ13 Type: MSJ-400-45 Joists: FJ151	Total Weight: 20.47 kg
		Laminations: 1

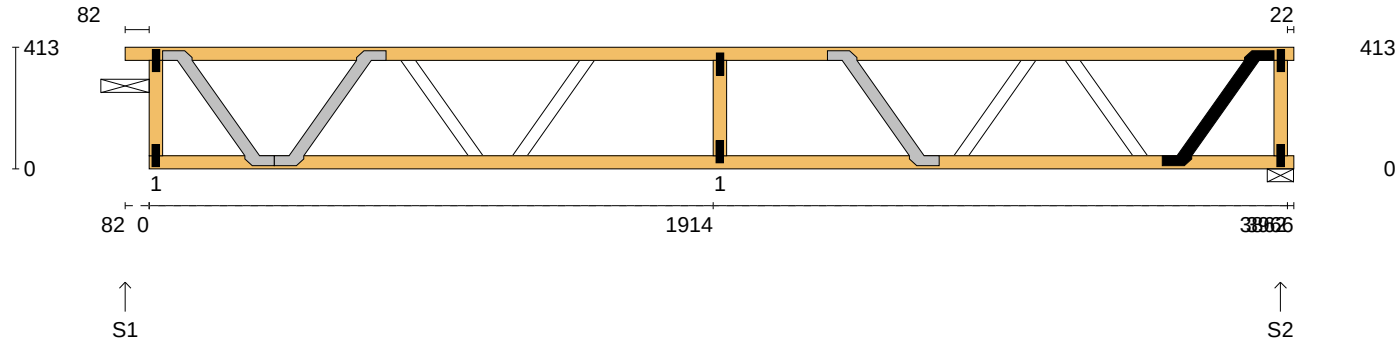

TIMBER / PLATES

Member	Size	Plating	Restraint
TC1	90x45-MGP10 H0 ADS	JD5	300
BC1	90x45-MGP10 H0 ADS	JD5	450
LEW1	90x45-MGP10 H0 ADS	JD5	
W1	90x45-MGP10 H0 ADS	JD5	
REW1	90x45-MGP10 H0 ADS	JD5	

Vertical Reactions at Supports


	S1	S2
1.35DL (kN)	0.52	0.56
1.2DL + 1.5LL (kN)	2.51	2.47

Joint Nail Plate

TL1	25x75-MN
BL2	25x75-MN
T1	25x75-MN
B1	25x75-MN
TR1	25x75-MN
BR2	25x75-MN

Span: 3966	Floor Material: Particle (13.9 kg/m²)	Application: General Areas	All dimensions in millimetres. This drawing should be read in conjunction with Multinail Technical sheets. Wall plates must be placed at supports only.	Joey Meriales (TN-012-015)
Overhang: 0/0	Floor Covering: Std Carpet + Underlay (8 kg/m²)	Live Load: 1.5 kPa		Ver: Floor 1.14.3
Spacing: 450	Ceiling Material: Plaster 10mm Std Core (6.7 kg/m²)	Point Load: 1.8 kN		Date: 10/04/2026
Quantity: 1	Ceiling Fixing: Direct fix @ 450c	Design: AS 1720.1-2010		Page: 21 of 45

Client: BSPOKE LUXURY HOMES PTY LTD	BB Truss & Timber Pty Ltd 41 Keilor Park Drive, Keilor Park 3042	Job No: K0964
Site: LOT 735 15 LEICHHARDT AVE BURNSIDE VIC 3023 AUS		Weight: 20.47 kg
Ref:	Joist Name: FJ13 Type: MSJ-400-45 Joists: FJ151	Total Weight: 20.47 kg
		Laminations: 1

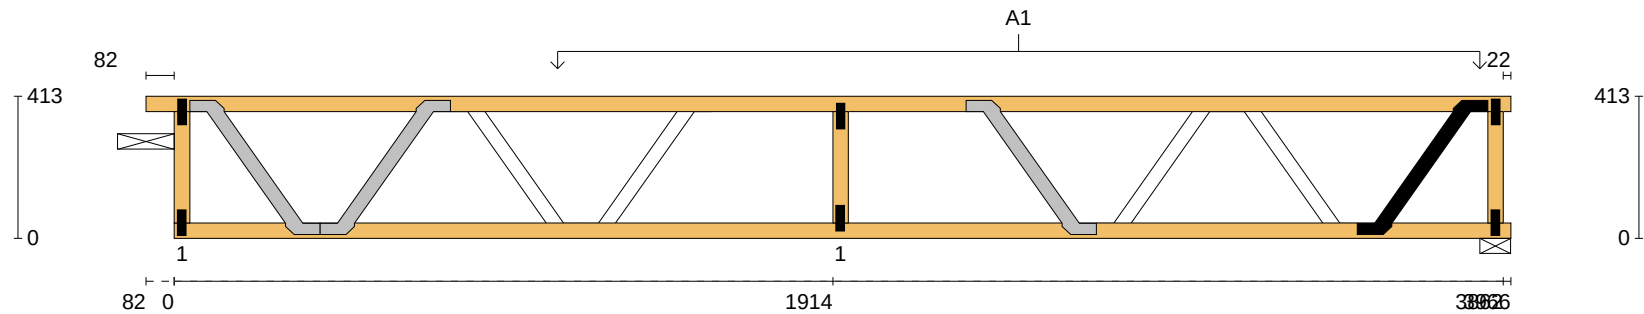


User Def. Load A1
8.70 kg/m²

Applied Load
DL (kN)
LL (kN)
WL Up (kN)
WL Dn (kN)

Span: 3966	Floor Material: Particle (13.9 kg/m²)	Application: General Areas	All dimensions in millimetres. This drawing should be read in conjunction with Multinail Technical sheets. Wall plates must be placed at supports only.	Joey Meriales (TN-012-015)
Overhang: 0/0	Floor Covering: Std Carpet + Underlay (8 kg/m²)	Live Load: 1.5 kPa		Ver: Floor 1.14.3
Spacing: 450	Ceiling Material: Plaster 10mm Std Core (6.7 kg/m²)	Point Load: 1.8 kN		Date: 10/04/2026
Quantity: 1	Ceiling Fixing: Direct fix @ 450c	Design: AS 1720.1-2010		Page: 22 of 45

Client: BSPOKE LUXURY HOMES PTY LTD	BB Truss & Timber Pty Ltd 41 Keilor Park Drive, Keilor Park 3042	Job No: K0964
Site: LOT 735 15 LEICHHARDT AVE BURNSIDE VIC 3023 AUS		Weight: 22.63 kg
Ref:	Joist Name: FJ14 Type: MSJ-400-45 Joists: FJ152	Total Weight: 22.63 kg
		Laminations: 1

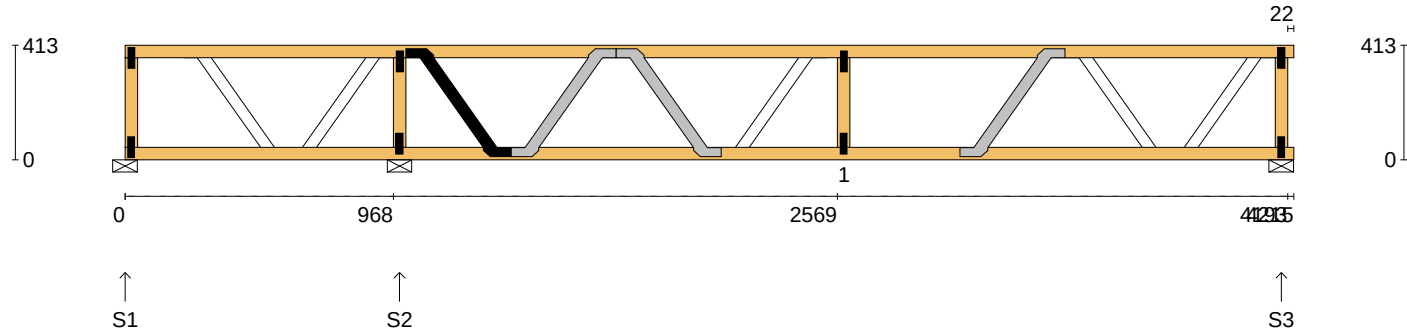

TIMBER / PLATES

Member	Size	Plating	Restraint
BC1	90x45-MGP10 H0 ADS	JD5	450
LEW1	90x45-MGP10 H0 ADS	JD5	
TC1	90x45-MGP10 H0 ADS	JD5	300
W1	90x45-MGP10 H0 ADS	JD5	
W2	90x45-MGP10 H0 ADS	JD5	
REW1	90x45-MGP10 H0 ADS	JD5	

Vertical Reactions at Supports


	S1	S2	S3
1.35DL (kN)	0.01	0.65	0.36
1.2DL + 1.5LL (kN)	-0.06	3.40	1.81

Joint Nail Plate

TL1	25x75-MN
BL2	25x75-MN
T1	25x75-MN
B1	25x75-MN
T2	25x75-MN
B2	25x75-MN
TR1	25x75-MN
BR2	25x75-MN

Span: 4215	Floor Material: Particle (13.9 kg/m²)	Application: General Areas	All dimensions in millimetres. This drawing should be read in conjunction with Multinail Technical sheets. Wall plates must be placed at supports only.	Joey Meriales (TN-012-015)
Overhang: 0/0	Floor Covering: Std Carpet + Underlay (8 kg/m²)	Live Load: 1.5 kPa		Ver: Floor 1.14.3
Spacing: 450	Ceiling Material: Plaster 10mm Std Core (6.7 kg/m²)	Point Load: 1.8 kN		Date: 10/04/2026
Quantity: 1	Ceiling Fixing: Direct fix @ 450c	Design: AS 1720.1-2010		Page: 23 of 45

Client: BSPOKE LUXURY HOMES PTY LTD	BB Truss & Timber Pty Ltd 41 Keilor Park Drive, Keilor Park 3042	Job No: K0964
Site: LOT 735 15 LEICHHARDT AVE BURNSIDE VIC 3023 AUS		Weight: 23.17 kg
Ref:	Joist Name: FJ15 Type: MSJ-400-45 Joists: FJ153, FJ154, FJ155, FJ156, FJ157	Total Weight: 115.84 kg
		Laminations: 1

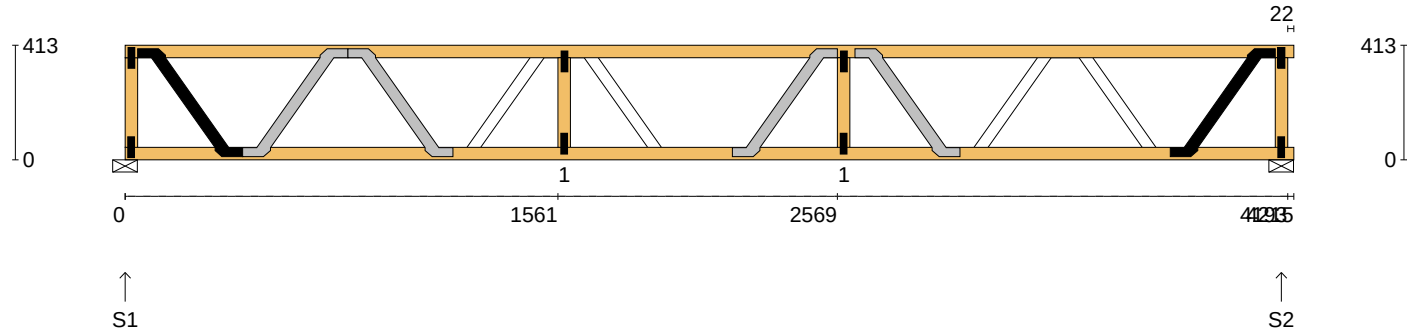

TIMBER / PLATES

Member	Size	Plating	Restraint
BC1	90x45-MGP10 H0 ADS	JD5	450
LEW1	90x45-MGP10 H0 ADS	JD5	
TC1	90x45-MGP10 H0 ADS	JD5	300
W1	90x45-MGP10 H0 ADS	JD5	
W2	90x45-MGP10 H0 ADS	JD5	
REW1	90x45-MGP10 H0 ADS	JD5	

Vertical Reactions at Supports


	S1	S2
1.35DL (kN)	0.50	0.51
1.2DL + 1.5LL (kN)	2.55	2.60

Joint Nail Plate

TL1	25x75-MN
BL2	25x75-MN
T1	25x75-MN
B1	25x75-MN
T2	25x75-MN
B2	25x75-MN
TR1	25x75-MN
BR2	25x75-MN

Span: 4215	Floor Material: Particle (13.9 kg/m²)	Application: General Areas	All dimensions in millimetres. This drawing should be read in conjunction with Multinail Technical sheets. Wall plates must be placed at supports only.	Joey Meriales (TN-012-015)
Overhang: 0/0	Floor Covering: Std Carpet + Underlay (8 kg/m²)	Live Load: 1.5 kPa		Ver: Floor 1.14.3
Spacing: 450	Ceiling Material: Plaster 10mm Std Core (6.7 kg/m²)	Point Load: 1.8 kN		Date: 10/04/2026
Quantity: 5	Ceiling Fixing: Direct fix @ 450c	Design: AS 1720.1-2010		Page: 24 of 45

Client: BSPOKE LUXURY HOMES PTY LTD	BB Truss & Timber Pty Ltd 41 Keilor Park Drive, Keilor Park 3042	Job No: K0964
Site: LOT 735 15 LEICHHARDT AVE BURNSIDE VIC 3023 AUS		Weight: 23.44 kg
Ref:	Joist Name: FJ16 Type: MSJ-400-45 Joists: FJ158, FJ159, FJ160	Total Weight: 70.31 kg
		Laminations: 1

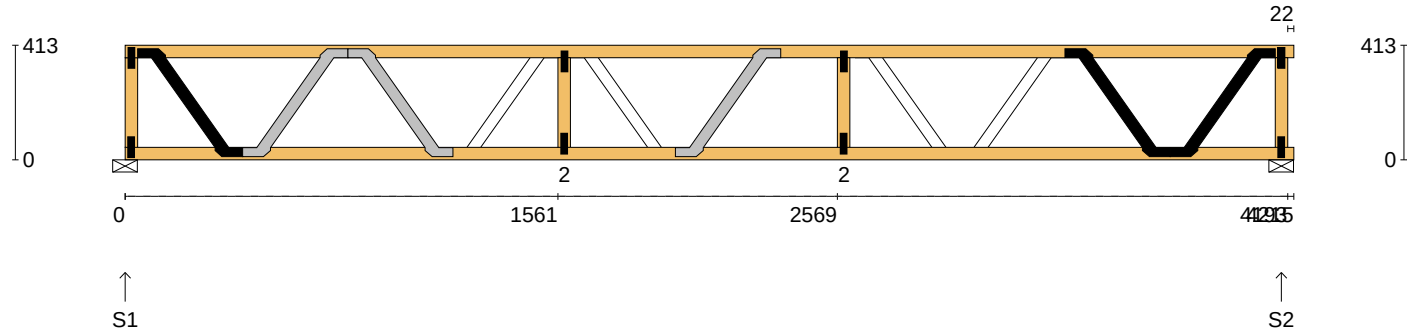

TIMBER / PLATES

Member	Size	Plating	Restraint
BC1	90x45-MGP10 H0 ADS	JD5	450
LEW1	90x45-MGP10 H0 ADS	JD5	
TC1	90x45-MGP10 H0 ADS	JD5	300
W1	90x45-MGP10 H0 ADS	JD5	
W2	90x45-MGP10 H0 ADS	JD5	
REW1	90x45-MGP10 H0 ADS	JD5	

Vertical Reactions at Supports


	S1	S2
1.35DL (kN)	0.77	1.25
1.2DL + 1.5LL (kN)	2.78	3.26

Joint Nail Plate

TL1	25x75-MN
BL2	25x75-MN
T1	25x75-MN
B1	25x75-MN
T2	25x75-MN
B2	25x75-MN
TR1	25x75-MN
BR2	25x75-MN

Span: 4215	Floor Material: Particle (13.9 kg/m²)	Application: General Areas	All dimensions in millimetres. This drawing should be read in conjunction with Multinail Technical sheets. Wall plates must be placed at supports only.	Joey Meriales (TN-012-015)
Overhang: 0/0	Floor Covering: Std Carpet + Underlay (8 kg/m²)	Live Load: 1.5 kPa		Ver: Floor 1.14.3
Spacing: 450	Ceiling Material: Plaster 10mm Std Core (6.7 kg/m²)	Point Load: 1.8 kN		Date: 10/04/2026
Quantity: 3	Ceiling Fixing: Direct fix @ 450c	Design: AS 1720.1-2010		Page: 25 of 45

Client: BSPOKE LUXURY HOMES PTY LTD	BB Truss & Timber Pty Ltd 41 Keilor Park Drive, Keilor Park 3042	Job No: K0964
Site: LOT 735 15 LEICHHARDT AVE BURNSIDE VIC 3023 AUS		Weight: 23.44 kg
Ref:	Joist Name: FJ16 Type: MSJ-400-45 Joists: FJ158, FJ159, FJ160	Total Weight: 70.31 kg
		Laminations: 1

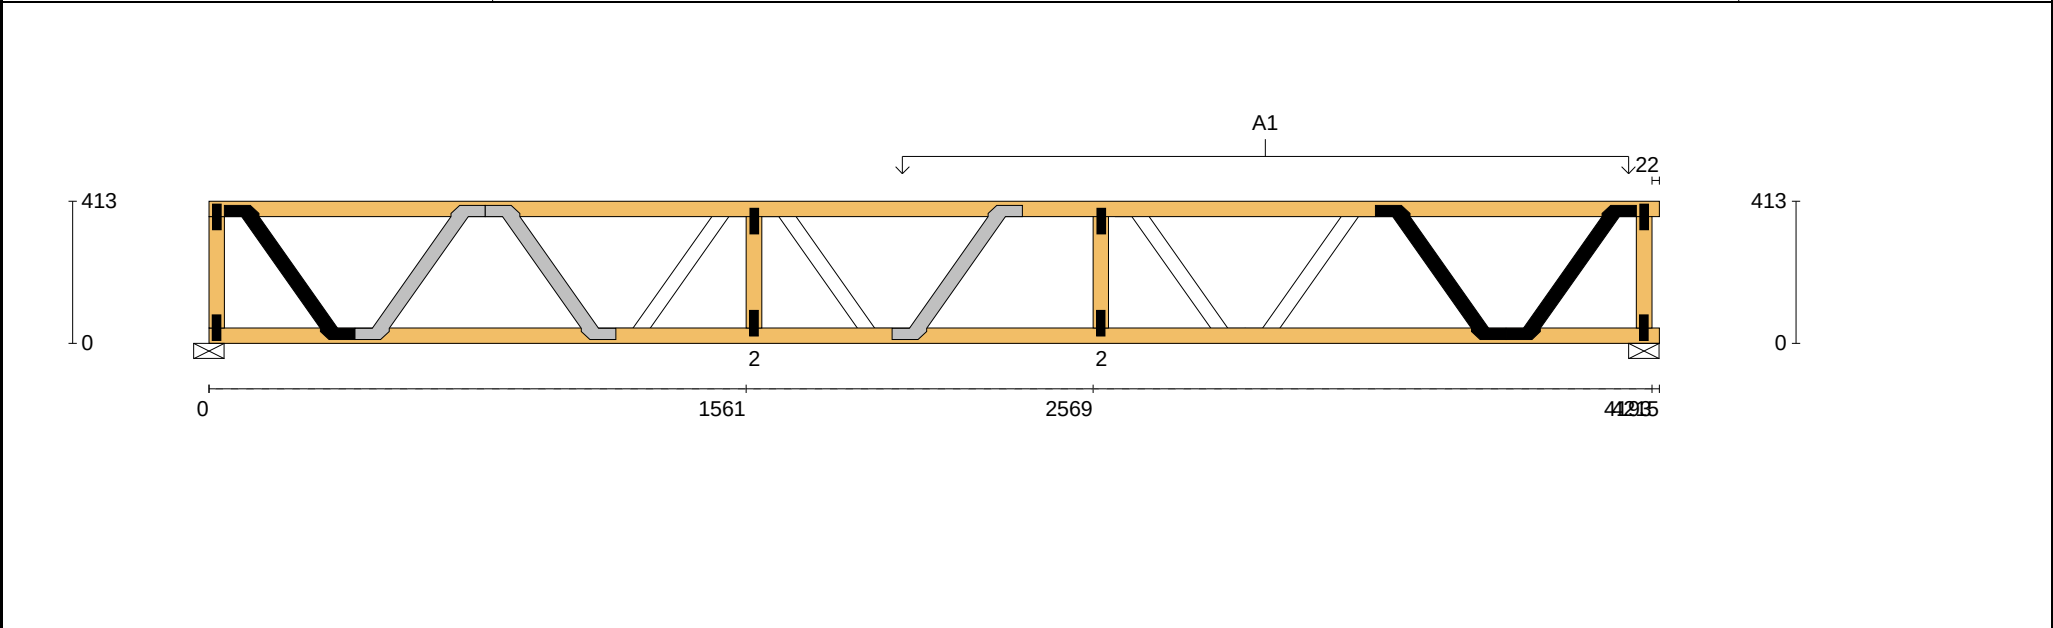


User Def. Load	A1 80.00 kg/m²
----------------	-------------------

Applied Load	
DL (kN)	
LL (kN)	
WL Up (kN)	
WL Dn (kN)	

Span: 4215	Floor Material: Particle (13.9 kg/m³)	Application: General Areas	All dimensions in millimetres. This drawing should be read in conjunction with Multinail Technical sheets. Wall plates must be placed at supports only.	Joey Meriales (TN-012-015)
Overhang: 0/0	Floor Covering: Std Carpet + Underlay (8 kg/m³)	Live Load: 1.5 kPa		Ver: Floor 1.14.3
Spacing: 450	Ceiling Material: Plaster 10mm Std Core (6.7 kg/m³)	Point Load: 1.8 kN		Date: 10/04/2026
Quantity: 3	Ceiling Fixing: Direct fix @ 450c	Design: AS 1720.1-2010		Page: 26 of 45

Client: BSPOKE LUXURY HOMES PTY LTD	BB Truss & Timber Pty Ltd 41 Keilor Park Drive, Keilor Park 3042	Job No: K0964
Site: LOT 735 15 LEICHHARDT AVE BURNSIDE VIC 3023 AUS		Weight: 23.70 kg
Ref:	Joist Name: FJ17 Type: MSJ-400-45 Joists: FJ161	Total Weight: 23.70 kg
		Laminations: 1

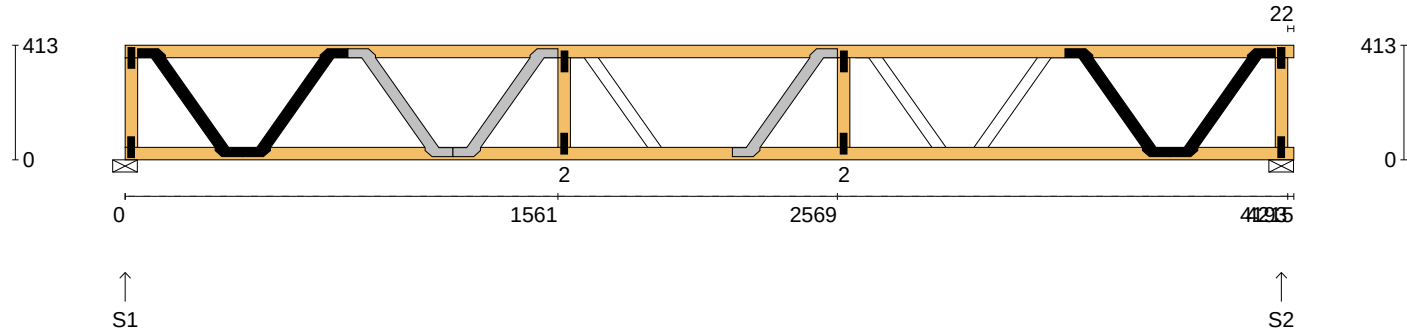

TIMBER / PLATES

Member	Size	Plating	Restraint
BC1	90x45-MGP10 H0 ADS	JD5	450
LEW1	90x45-MGP10 H0 ADS	JD5	
TC1	90x45-MGP10 H0 ADS	JD5	300
W1	90x45-MGP10 H0 ADS	JD5	
W2	90x45-MGP10 H0 ADS	JD5	
REW1	90x45-MGP10 H0 ADS	JD5	

Vertical Reactions at Supports


	S1	S2
1.35DL (kN)	1.11	1.43
1.2DL + 1.5LL (kN)	3.09	3.42

Joint Nail Plate

TL1	25x75-MN
BL2	25x75-MN
T1	25x75-MN
B1	25x75-MN
T2	25x75-MN
B2	25x75-MN
TR1	25x75-MN
BR2	25x75-MN

Span: 4215	Floor Material: Particle (13.9 kg/m²)	Application: General Areas	All dimensions in millimetres. This drawing should be read in conjunction with Multinail Technical sheets. Wall plates must be placed at supports only.	Joey Meriales (TN-012-015)
Overhang: 0/0	Floor Covering: Std Carpet + Underlay (8 kg/m²)	Live Load: 1.5 kPa		Ver: Floor 1.14.3
Spacing: 450	Ceiling Material: Plaster 10mm Std Core (6.7 kg/m²)	Point Load: 1.8 kN		Date: 10/04/2026
Quantity: 1	Ceiling Fixing: Direct fix @ 450c	Design: AS 1720.1-2010		Page: 27 of 45

Client: BSPOKE LUXURY HOMES PTY LTD	BB Truss & Timber Pty Ltd 41 Keilor Park Drive, Keilor Park 3042	Job No: K0964
Site: LOT 735 15 LEICHHARDT AVE BURNSIDE VIC 3023 AUS		Weight: 23.70 kg
Ref:	Joist Name: FJ17 Type: MSJ-400-45 Joists: FJ161	Total Weight: 23.70 kg
		Laminations: 1

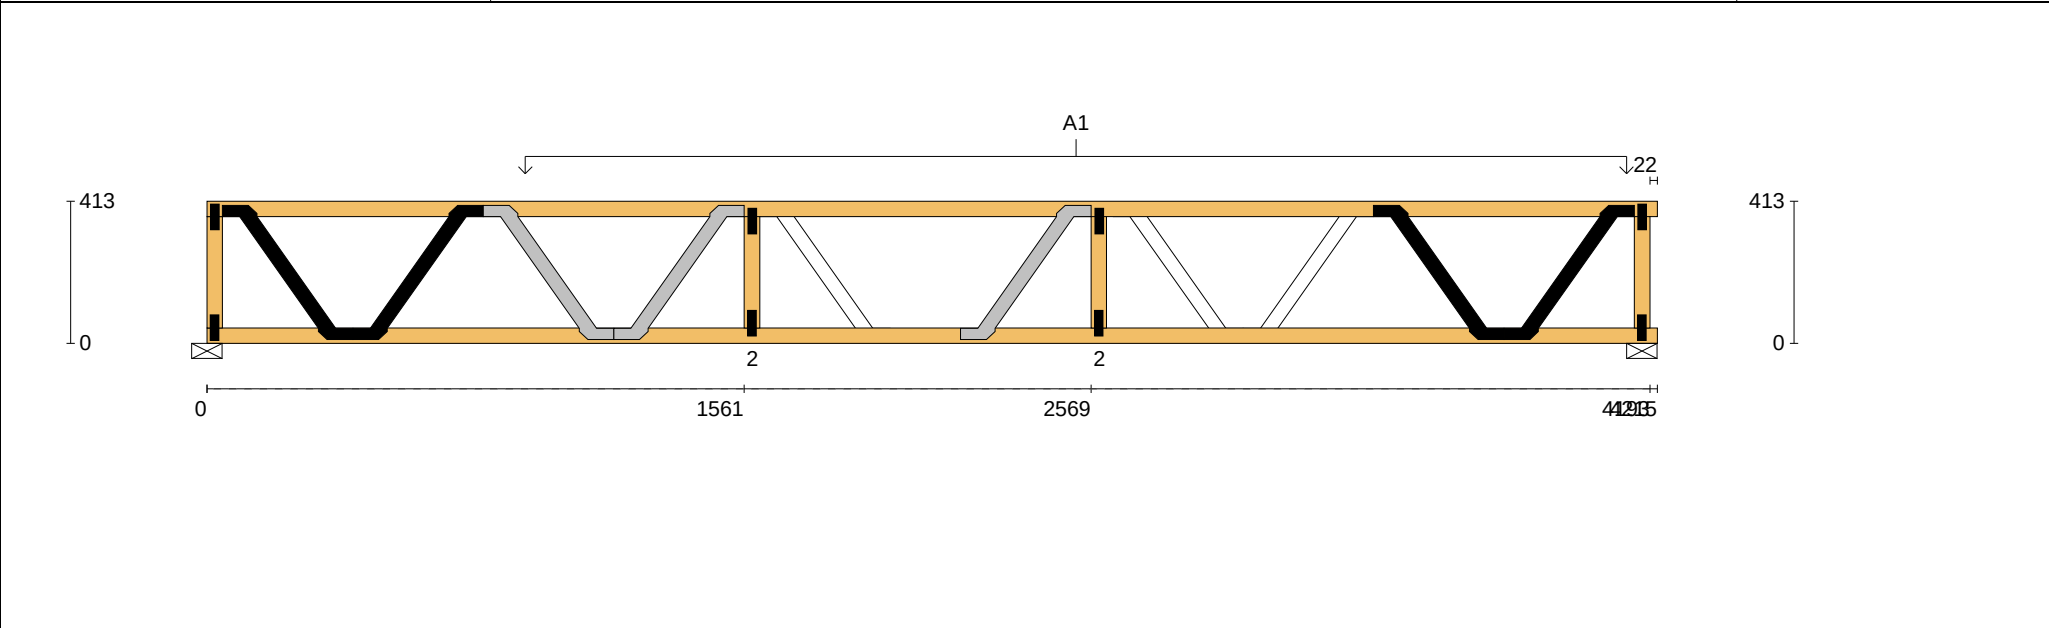


User Def. Load	A1 80.00 kg/m²
----------------	-------------------

Applied Load	
DL (kN)	
LL (kN)	
WL Up (kN)	
WL Dn (kN)	

Span: 4215	Floor Material: Particle (13.9 kg/m³)	Application: General Areas	All dimensions in millimetres. This drawing should be read in conjunction with Multinail Technical sheets. Wall plates must be placed at supports only.	Joey Meriales (TN-012-015)
Overhang: 0/0	Floor Covering: Std Carpet + Underlay (8 kg/m³)	Live Load: 1.5 kPa		Ver: Floor 1.14.3
Spacing: 450	Ceiling Material: Plaster 10mm Std Core (6.7 kg/m³)	Point Load: 1.8 kN		Date: 10/04/2026
Quantity: 1	Ceiling Fixing: Direct fix @ 450c	Design: AS 1720.1-2010		Page: 28 of 45

Client: BSPOKE LUXURY HOMES PTY LTD	BB Truss & Timber Pty Ltd 41 Keilor Park Drive, Keilor Park 3042	Job No: K0964
Site: LOT 735 15 LEICHHARDT AVE BURNSIDE VIC 3023 AUS		Weight: 17.90 kg
Ref:	Joist Name: FJ18 Type: MSJ-400-45 Joists: FJ162, FJ163, FJ164, FJ165	Total Weight: 71.61 kg
		Laminations: 1

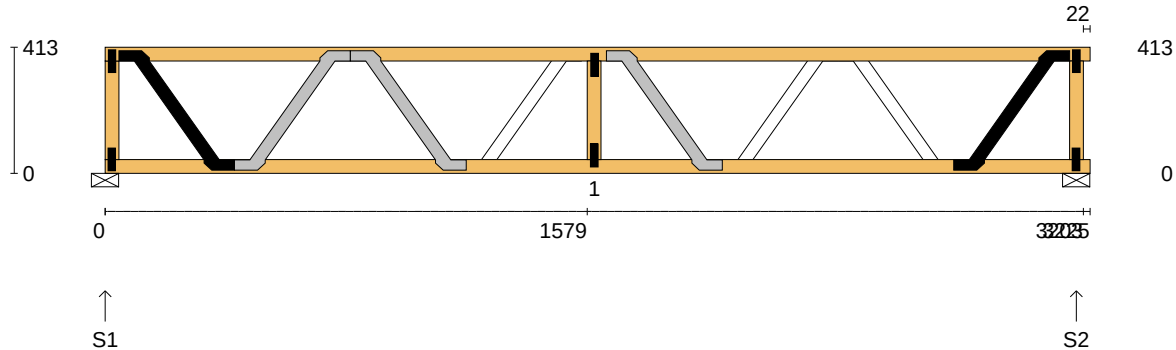

TIMBER / PLATES

Member	Size	Plating	Restraint
BC1	90x45-MGP10 H0 ADS JD5	JD5	450
LEW1	90x45-MGP10 H0 ADS JD5	JD5	
TC1	90x45-MGP10 H0 ADS JD5	JD5	300
W1	90x45-MGP10 H0 ADS JD5	JD5	
REW1	90x45-MGP10 H0 ADS JD5	JD5	

Vertical Reactions at Supports


	S1	S2
1.35DL (kN)	0.38	0.39
1.2DL + 1.5LL (kN)	1.94	1.99

Joint Nail Plate

TL1	25x75-MN
BL2	25x75-MN
T1	25x75-MN
B1	25x75-MN
TR1	25x75-MN
BR2	25x75-MN

Span: 3225	Floor Material: Particle (13.9 kg/m²)	Application: General Areas	All dimensions in millimetres. This drawing should be read in conjunction with Multinail Technical sheets. Wall plates must be placed at supports only.	Joey Meriales (TN-012-015)
Overhang: 0/0	Floor Covering: Std Carpet + Underlay (8 kg/m²)	Live Load: 1.5 kPa		Ver: Floor 1.14.3
Spacing: 450	Ceiling Material: Plaster 10mm Std Core (6.7 kg/m²)	Point Load: 1.8 kN		Date: 10/04/2026
Quantity: 4	Ceiling Fixing: Direct fix @ 450c	Design: AS 1720.1-2010		Page: 29 of 45

Client: BSPOKE LUXURY HOMES PTY LTD	BB Truss & Timber Pty Ltd 41 Keilor Park Drive, Keilor Park 3042 Joist Name: FJ19 Type: MSJ-400-45 P. Ladder Joists: FJ166	Job No: K0964
Site: LOT 735 15 LEICHHARDT AVE BURNSIDE VIC 3023 AUS		Weight: 21.35 kg
Ref:		Total Weight: 21.35 kg Laminations: 1

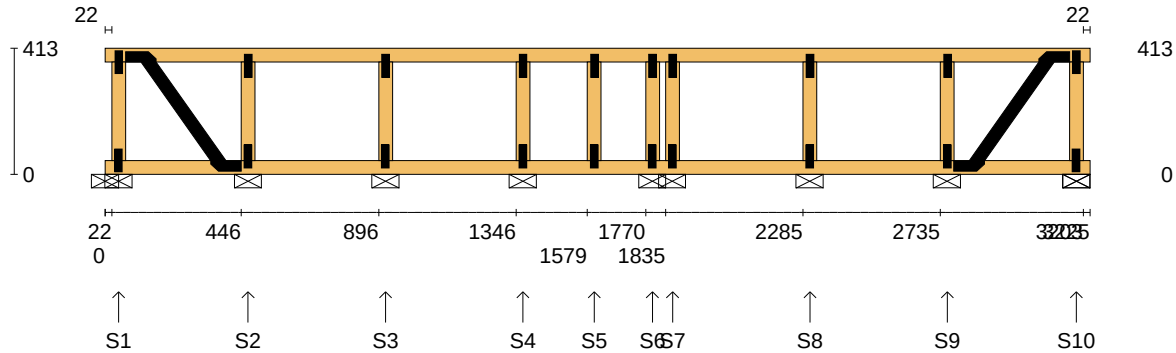

TIMBER / PLATES

Member	Size	Plating	Restraint
BC1	90x45-MGP10 H0 ADS	JD5	450
TC1	90x45-MGP10 H0 ADS	JD5	300
LEW1	90x45-MGP10 H0 ADS	JD5	
W1	90x45-MGP10 H0 ADS	JD5	
W2	90x45-MGP10 H0 ADS	JD5	
W3	90x45-MGP10 H0 ADS	JD5	
W4	90x45-MGP10 H0 ADS	JD5	
W5	90x45-MGP10 H0 ADS	JD5	
W6	90x45-MGP10 H0 ADS	JD5	
W7	90x45-MGP10 H0 ADS	JD5	
W8	90x45-MGP10 H0 ADS	JD5	
REW1	90x45-MGP10 H0 ADS	JD5	

Vertical Reactions at Supports


	S1	S2	S3	S4	S5	S6	S7	S8	S9	S10
1.35DL (kN)	0.05	0.13	0.11	0.10	0.04	0.01	0.10	0.11	0.13	0.05
1.2DL + 1.5LL (kN)	0.20	0.67	0.56	0.47	0.18	0.04	0.45	0.56	0.67	0.19

Joint Nail Plate

Joint	Nail Plate	Joint	Nail Plate
TL1	25x75-MN	B6	25x75-MN
BL2	25x75-MN	T7	25x75-MN
T1	25x75-MN	B7	25x75-MN
B1	25x75-MN	T8	25x75-MN
T2	25x75-MN	B8	25x75-MN
B2	25x75-MN	TR1	25x75-MN
T3	25x75-MN	BR2	25x75-MN
B3	25x75-MN		
T4	25x75-MN		
B4	25x75-MN		
T5	25x75-MN		
B5	25x75-MN		
T6	25x75-MN		

Span: 3225	Floor Material: Particle (13.9 kg/m²)	Application: General Areas	All dimensions in millimetres. This drawing should be read in conjunction with Multinail Technical sheets. Wall plates must be placed at supports only.	Joey Meriales (TN-012-015)
Overhang: 0/0	Floor Covering: Std Carpet + Underlay (8 kg/m²)	Live Load: 1.5 kPa		Ver: Floor 1.14.3
Spacing: 450	Ceiling Material: Plaster 10mm Std Core (6.7 kg/m²)	Point Load: 1.8 kN		Date: 10/04/2026
Quantity: 1	Ceiling Fixing: Direct fix @ 450c	Design: AS 1720.1-2010		Page: 30 of 45

Client: BSPOKE LUXURY HOMES PTY LTD	BB Truss & Timber Pty Ltd 41 Keilor Park Drive, Keilor Park 3042 Joist Name: FJ20 Type: MSJ-400-45 P. Ladder Joists: FJ167	Job No: K0964
Site: LOT 735 15 LEICHHARDT AVE BURNSIDE VIC 3023 AUS		Weight: 28.59 kg
Ref:		Total Weight: 28.59 kg Laminations: 1

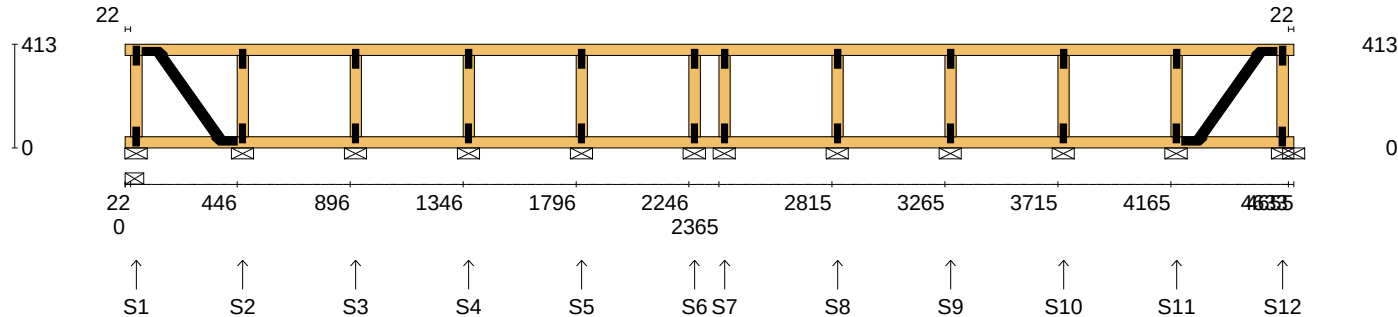

TIMBER / PLATES

Member	Size	Plating	Restraint
BC1	90x45-MGP10 H0 ADS	JD5	450
TC1	90x45-MGP10 H0 ADS	JD5	300
LEW1	90x45-MGP10 H0 ADS	JD5	
W1	90x45-MGP10 H0 ADS	JD5	
W2	90x45-MGP10 H0 ADS	JD5	
W3	90x45-MGP10 H0 ADS	JD5	
W4	90x45-MGP10 H0 ADS	JD5	
W5	90x45-MGP10 H0 ADS	JD5	
W6	90x45-MGP10 H0 ADS	JD5	
W7	90x45-MGP10 H0 ADS	JD5	
W8	90x45-MGP10 H0 ADS	JD5	
W9	90x45-MGP10 H0 ADS	JD5	
W10	90x45-MGP10 H0 ADS	JD5	

- 1 more member was not shown -


Vertical Reactions at Supports

	S1	S2	S3	S4	S5	S6	S7	S8	S9	S10	S11	S12
1.35DL (kN)	0.05	0.13	0.11	0.11	0.12	0.07	0.08	0.13	0.11	0.11	0.13	0.05
1.2DL + 1.5LL (kN)	0.20	0.67	0.54	0.55	0.57	0.34	0.34	0.59	0.56	0.54	0.67	0.20

Joint	Nail Plate	Joint	Nail Plate
TL1	25x75-MN	B6	25x75-MN
BL2	25x75-MN	T7	25x75-MN
T1	25x75-MN	B7	25x75-MN
B1	25x75-MN	T8	25x75-MN
T2	25x75-MN	B8	25x75-MN
B2	25x75-MN	T9	25x75-MN
T3	25x75-MN	B9	25x75-MN
B3	25x75-MN	T10	25x75-MN
T4	25x75-MN	B10	25x75-MN
B4	25x75-MN	TR1	25x75-MN
T5	25x75-MN	BR2	25x75-MN
B5	25x75-MN		
T6	25x75-MN		

Span: 4655	Floor Material: Particle (13.9 kg/m²)	Application: General Areas	All dimensions in millimetres. This drawing should be read in conjunction with Multinail Technical sheets. Wall plates must be placed at supports only.	Joey Meriales (TN-012-015)
Overhang: 0/0	Floor Covering: Std Carpet + Underlay (8 kg/m²)	Live Load: 1.5 kPa		Ver: Floor 1.14.3
Spacing: 450	Ceiling Material: Plaster 10mm Std Core (6.7 kg/m²)	Point Load: 1.8 kN		Date: 10/04/2026
Quantity: 1	Ceiling Fixing: Direct fix @ 450c	Design: AS 1720.1-2010		Page: 31 of 45


Client: BSPOKE LUXURY HOMES PTY LTD	BB Truss & Timber Pty Ltd 41 Keilor Park Drive, Keilor Park 3042	Job No: K0964
Site: LOT 735 15 LEICHHARDT AVE BURNSIDE VIC 3023 AUS		Weight: 28.59 kg
Ref:	Joist Name: FJ20 Type: MSJ-400-45 P. Ladder Joists: FJ167	Total Weight: 28.59 kg
		Laminations: 1

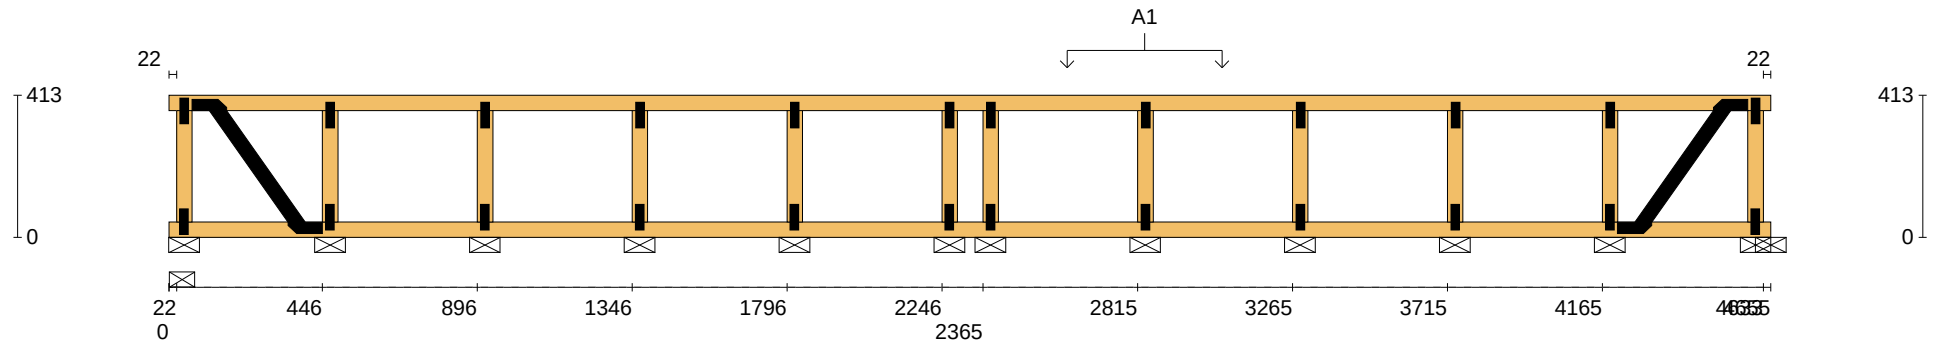

User Def. Load	A1 8.70 kg/m ²
Applied Load	
DL (kN)	
LL (kN)	
WL Up (kN)	
WL Dn (kN)	

Span: 4655	Floor Material: Particle (13.9 kg/m²)	Application: General Areas	All dimensions in millimetres. This drawing should be read in conjunction with Multinail Technical sheets. Wall plates must be placed at supports only.	Joey Meriales (TN-012-015)
Overhang: 0/0	Floor Covering: Std Carpet + Underlay (8 kg/m²)	Live Load: 1.5 kPa		Ver: Floor 1.14.3
Spacing: 450	Ceiling Material: Plaster 10mm Std Core (6.7 kg/m²)	Point Load: 1.8 kN		Date: 10/04/2026
Quantity: 1	Ceiling Fixing: Direct fix @ 450c	Design: AS 1720.1-2010		Page: 32 of 45

Client: BSPOKE LUXURY HOMES PTY LTD	BB Truss & Timber Pty Ltd 41 Keilor Park Drive, Keilor Park 3042	Job No: K0964
Site: LOT 735 15 LEICHHARDT AVE BURNSIDE VIC 3023 AUS	Joist Name: FJ21 Type: MSJ-400-45	Weight: 21.35 kg
Ref:	Joists: FJ171, FJ172, FJ173, FJ174	Total Weight: 85.41 kg
		Laminations: 1

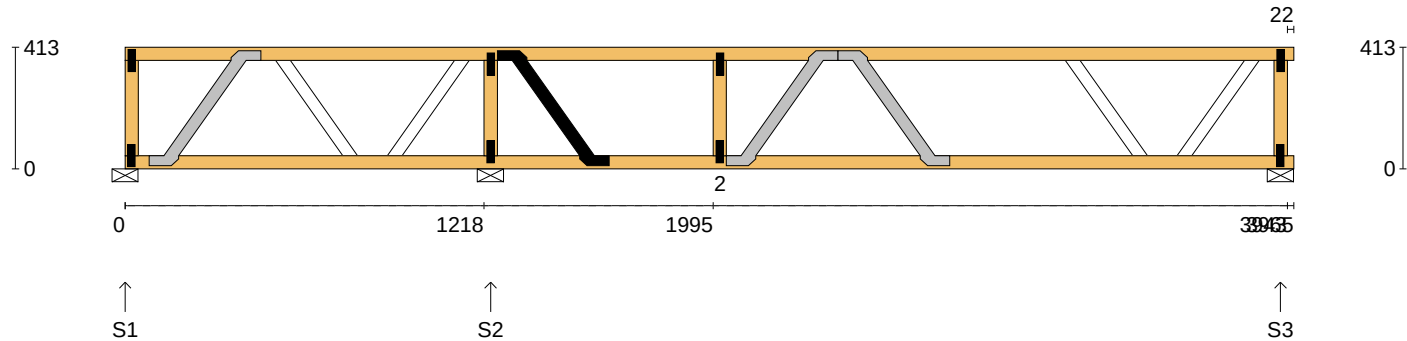

TIMBER / PLATES

Member	Size	Plating	Restraint
BC1	90x45-MGP10 H0 ADS	JD5	450
LEW1	90x45-MGP10 H0 ADS	JD5	
TC1	90x45-MGP10 H0 ADS	JD5	300
W1	90x45-MGP10 H0 ADS	JD5	
W2	90x45-MGP10 H0 ADS	JD5	
REW1	90x45-MGP10 H0 ADS	JD5	

Vertical Reactions at Supports


	S1	S2	S3
1.35DL (kN)	0.10	0.61	0.38
1.2DL + 1.5LL (kN)	0.67	2.57	1.72

Joint Nail Plate

TL1	25x75-MN
BL2	25x75-MN
T1	25x75-MN
B1	25x75-MN
T2	25x75-MN
B2	25x75-MN
TR1	25x75-MN
BR2	25x75-MN

Span: 3965	Floor Material: Particle (13.9 kg/m²)	Application: General Areas	All dimensions in millimetres. This drawing should be read in conjunction with Multinail Technical sheets.	Joey Meriales (TN-012-015)
Overhang: 0/0	Floor Covering: Std Carpet + Underlay (8 kg/m²)	Live Load: 1.5 kPa	Wall plates must be placed at supports only.	Ver: Floor 1.14.3
Spacing: 450	Ceiling Material: Plaster 10mm Std Core (6.7 kg/m²)	Point Load: 1.8 kN		Date: 10/04/2026
Quantity: 4	Ceiling Fixing: Direct fix @ 450c	Design: AS 1720.1-2010		Page: 33 of 45

Client: BSPOKE LUXURY HOMES PTY LTD	BB Truss & Timber Pty Ltd 41 Keilor Park Drive, Keilor Park 3042	Job No: K0964
Site: LOT 735 15 LEICHHARDT AVE BURNSIDE VIC 3023 AUS		Weight: 21.35 kg
Ref:	Joist Name: FJ21 Type: MSJ-400-45	Total Weight: 85.41 kg
	Joists: FJ171, FJ172, FJ173, FJ174	Laminations: 1

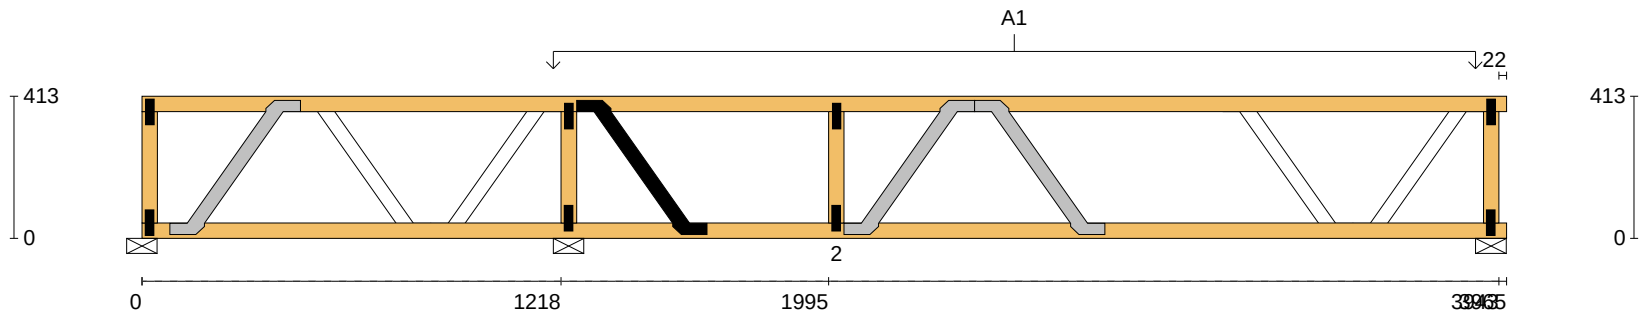


User Def. Load A1
8.70 kg/m²

Applied Load
DL (kN)
LL (kN)
WL Up (kN)
WL Dn (kN)

Span: 3965	Floor Material: Particle (13.9 kg/m²)	Application: General Areas	All dimensions in millimetres. This drawing should be read in conjunction with Multinail Technical sheets. Wall plates must be placed at supports only.	Joey Meriales (TN-012-015)
Overhang: 0/0	Floor Covering: Std Carpet + Underlay (8 kg/m²)	Live Load: 1.5 kPa		Ver: Floor 1.14.3
Spacing: 450	Ceiling Material: Plaster 10mm Std Core (6.7 kg/m²)	Point Load: 1.8 kN		Date: 10/04/2026
Quantity: 4	Ceiling Fixing: Direct fix @ 450c	Design: AS 1720.1-2010		Page: 34 of 45

Client: BSPOKE LUXURY HOMES PTY LTD	BB Truss & Timber Pty Ltd 41 Keilor Park Drive, Keilor Park 3042	Job No: K0964
Site: LOT 735 15 LEICHHARDT AVE BURNSIDE VIC 3023 AUS		Weight: 21.35 kg
Ref:	Joist Name: FJ22 Type: MSJ-400-45 Joists: FJ175, FJ200	Total Weight: 42.71 kg
		Laminations: 1

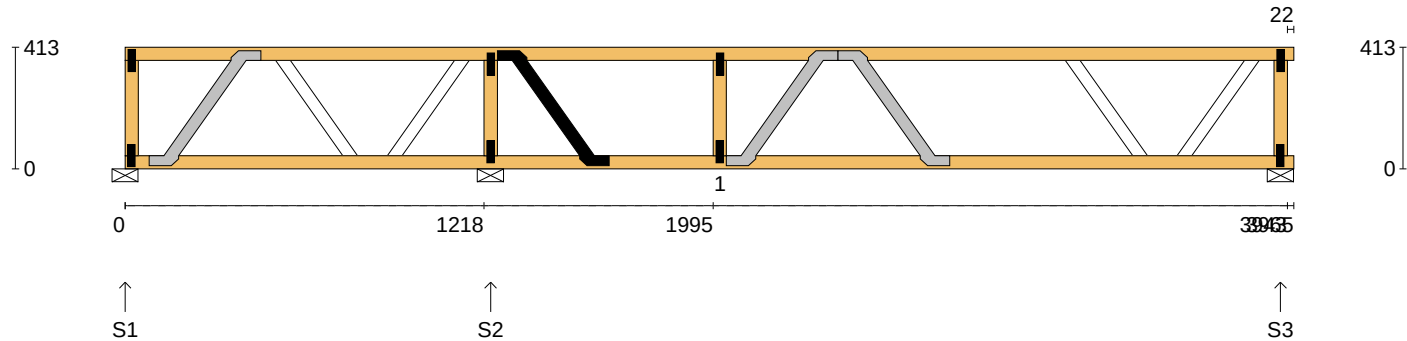

TIMBER / PLATES

Member	Size	Plating	Restraint
BC1	90x45-MGP10 H0 ADS	JD5	450
LEW1	90x45-MGP10 H0 ADS	JD5	
TC1	90x45-MGP10 H0 ADS	JD5	300
W1	90x45-MGP10 H0 ADS	JD5	
W2	90x45-MGP10 H0 ADS	JD5	
REW1	90x45-MGP10 H0 ADS	JD5	

Vertical Reactions at Supports


	S1	S2	S3
1.35DL (kN)	0.12	0.52	0.32
1.2DL + 1.5LL (kN)	0.69	2.48	1.67

Joint Nail Plate

TL1	25x75-MN
BL2	25x75-MN
T1	25x75-MN
B1	25x75-MN
T2	25x75-MN
B2	25x75-MN
TR1	25x75-MN
BR2	25x75-MN

Span: 3965	Floor Material: Particle (13.9 kg/m²)	Application: General Areas	All dimensions in millimetres. This drawing should be read in conjunction with Multinail Technical sheets. Wall plates must be placed at supports only.	Joey Meriales (TN-012-015)
Overhang: 0/0	Floor Covering: Std Carpet + Underlay (8 kg/m²)	Live Load: 1.5 kPa		Ver: Floor 1.14.3
Spacing: 450	Ceiling Material: Plaster 10mm Std Core (6.7 kg/m²)	Point Load: 1.8 kN		Date: 10/04/2026
Quantity: 2	Ceiling Fixing: Direct fix @ 450c	Design: AS 1720.1-2010		Page: 35 of 45

Client: BSPOKE LUXURY HOMES PTY LTD	BB Truss & Timber Pty Ltd 41 Keilor Park Drive, Keilor Park 3042	Job No: K0964
Site: LOT 735 15 LEICHHARDT AVE BURNSIDE VIC 3023 AUS		Weight: 14.82 kg
Ref:	Joist Name: FJ23 Type: MSJ-400-45 Joists: FJ177, FJ178	Total Weight: 29.63 kg
		Laminations: 1

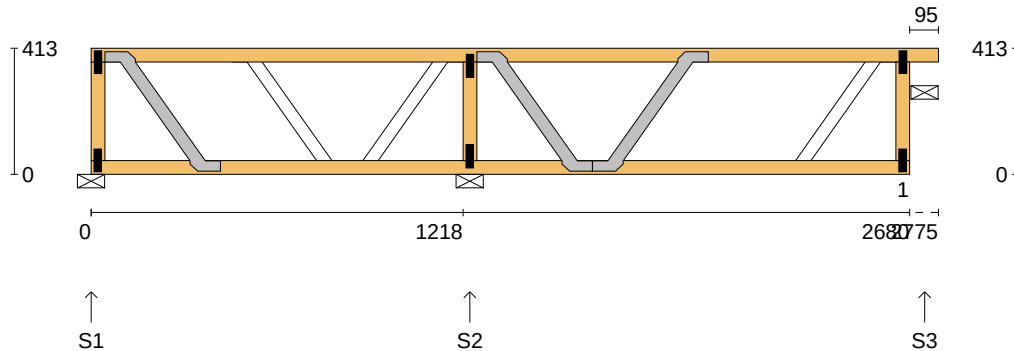

TIMBER / PLATES

Member	Size	Plating	Restraint
BC1	90x45-MGP10 H0 ADS	JD5	450
LEW1	90x45-MGP10 H0 ADS	JD5	
TC1	90x45-MGP10 H0 ADS	JD5	300
W1	90x45-MGP10 H0 ADS	JD5	
REW1	90x45-MGP10 H0 ADS	JD5	

Vertical Reactions at Supports


	S1	S2	S3
1.35DL (kN)	0.08	0.44	0.13
1.2DL + 1.5LL (kN)	0.29	2.46	0.62

Joint Nail Plate

TL1	25x75-MN
BL2	25x75-MN
T1	25x75-MN
B1	25x75-MN
TR1	25x75-MN
BR2	25x75-MN

Span: 2775	Floor Material: Particle (13.9 kg/m²)	Application: General Areas	All dimensions in millimetres. This drawing should be read in conjunction with Multinail Technical sheets. Wall plates must be placed at supports only.	Joey Meriales (TN-012-015)
Overhang: 0/0	Floor Covering: Std Carpet + Underlay (8 kg/m²)	Live Load: 1.5 kPa		Ver: Floor 1.14.3
Spacing: 450	Ceiling Material: Plaster 10mm Std Core (6.7 kg/m²)	Point Load: 1.8 kN		Date: 10/04/2026
Quantity: 2	Ceiling Fixing: Direct fix @ 450c	Design: AS 1720.1-2010		Page: 36 of 45

Client: BSPOKE LUXURY HOMES PTY LTD	BB Truss & Timber Pty Ltd 41 Keilor Park Drive, Keilor Park 3042	Job No: K0964
Site: LOT 735 15 LEICHHARDT AVE BURNSIDE VIC 3023 AUS		Weight: 15.35 kg
Ref:	Joist Name: FJ24 Type: MSJ-400-45 Joists: FJ179, FJ180, FJ199	Total Weight: 46.06 kg
		Laminations: 1

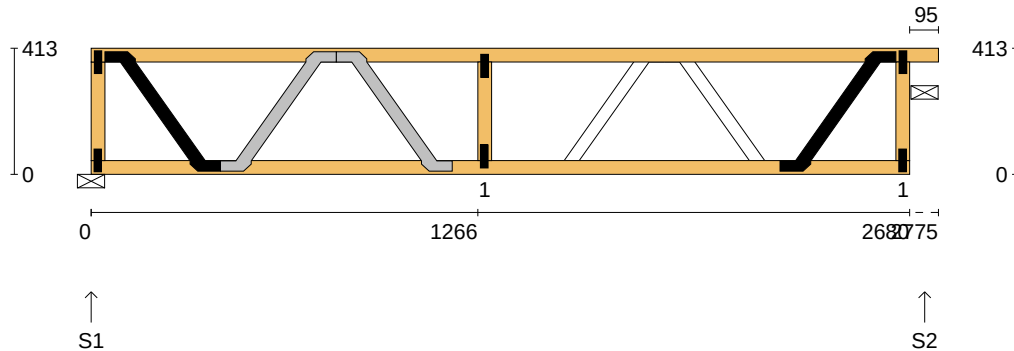

TIMBER / PLATES

Member	Size	Plating	Restraint
BC1	90x45-MGP10 H0 ADS	JD5	450
LEW1	90x45-MGP10 H0 ADS	JD5	
TC1	90x45-MGP10 H0 ADS	JD5	300
W1	90x45-MGP10 H0 ADS	JD5	
REW1	90x45-MGP10 H0 ADS	JD5	

Vertical Reactions at Supports


	S1	S2
1.35DL (kN)	0.32	0.34
1.2DL + 1.5LL (kN)	1.62	1.76

Joint Nail Plate

TL1	25x75-MN
BL2	25x75-MN
T1	25x75-MN
B1	25x75-MN
TR1	25x75-MN
BR2	25x75-MN

Span: 2775	Floor Material: Particle (13.9 kg/m²)	Application: General Areas	All dimensions in millimetres. This drawing should be read in conjunction with Multinail Technical sheets. Wall plates must be placed at supports only.	Joey Meriales (TN-012-015)
Overhang: 0/0	Floor Covering: Std Carpet + Underlay (8 kg/m²)	Live Load: 1.5 kPa		Ver: Floor 1.14.3
Spacing: 450	Ceiling Material: Plaster 10mm Std Core (6.7 kg/m²)	Point Load: 1.8 kN		Date: 10/04/2026
Quantity: 3	Ceiling Fixing: Direct fix @ 450c	Design: AS 1720.1-2010		Page: 37 of 45

Client: BSPOKE LUXURY HOMES PTY LTD	BB Truss & Timber Pty Ltd 41 Keilor Park Drive, Keilor Park 3042	Job No: K0964
Site: LOT 735 15 LEICHHARDT AVE BURNSIDE VIC 3023 AUS		Weight: 11.37 kg
Ref:	Joist Name: FJ25 Type: MSJ-400-45 Joists: FJ181, FJ182, FJ183, FJ184	Total Weight: 45.46 kg
		Laminations: 1

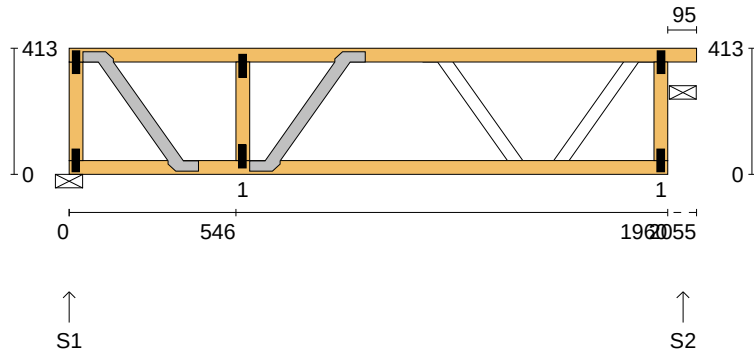

TIMBER / PLATES

Member	Size	Plating	Restraint
BC1	90x45-MGP10 H0 ADS	JD5	450
LEW1	90x45-MGP10 H0 ADS	JD5	
TC1	90x45-MGP10 H0 ADS	JD5	300
W1	90x45-MGP10 H0 ADS	JD5	
REW1	90x45-MGP10 H0 ADS	JD5	

Vertical Reactions at Supports


	S1	S2
1.35DL (kN)	0.24	0.25
1.2DL + 1.5LL (kN)	1.18	1.32

Joint Nail Plate

TL1	25x75-MN
BL2	25x75-MN
T1	25x75-MN
B1	25x75-MN
TR1	25x75-MN
BR2	25x75-MN

Span: 2055	Floor Material: Particle (13.9 kg/m²)	Application: General Areas	All dimensions in millimetres. This drawing should be read in conjunction with Multinail Technical sheets. Wall plates must be placed at supports only.	Joey Meriales (TN-012-015)
Overhang: 0/0	Floor Covering: Std Carpet + Underlay (8 kg/m²)	Live Load: 1.5 kPa		Ver: Floor 1.14.3
Spacing: 450	Ceiling Material: Plaster 10mm Std Core (6.7 kg/m²)	Point Load: 1.8 kN		Date: 10/04/2026
Quantity: 4	Ceiling Fixing: Direct fix @ 450c	Design: AS 1720.1-2010		Page: 38 of 45


Client: BSPOKE LUXURY HOMES PTY LTD	BB Truss & Timber Pty Ltd 41 Keilor Park Drive, Keilor Park 3042	Job No: K0964
Site: LOT 735 15 LEICHHARDT AVE BURNSIDE VIC 3023 AUS		Weight: 6.14 kg
Ref:	Joist Name: SJ27 Type: 53x90-MGP10 H0 ADS Joists: SJ186, SJ187, SJ188, SJ189	Total Weight: 24.58 kg
		Laminations: 1

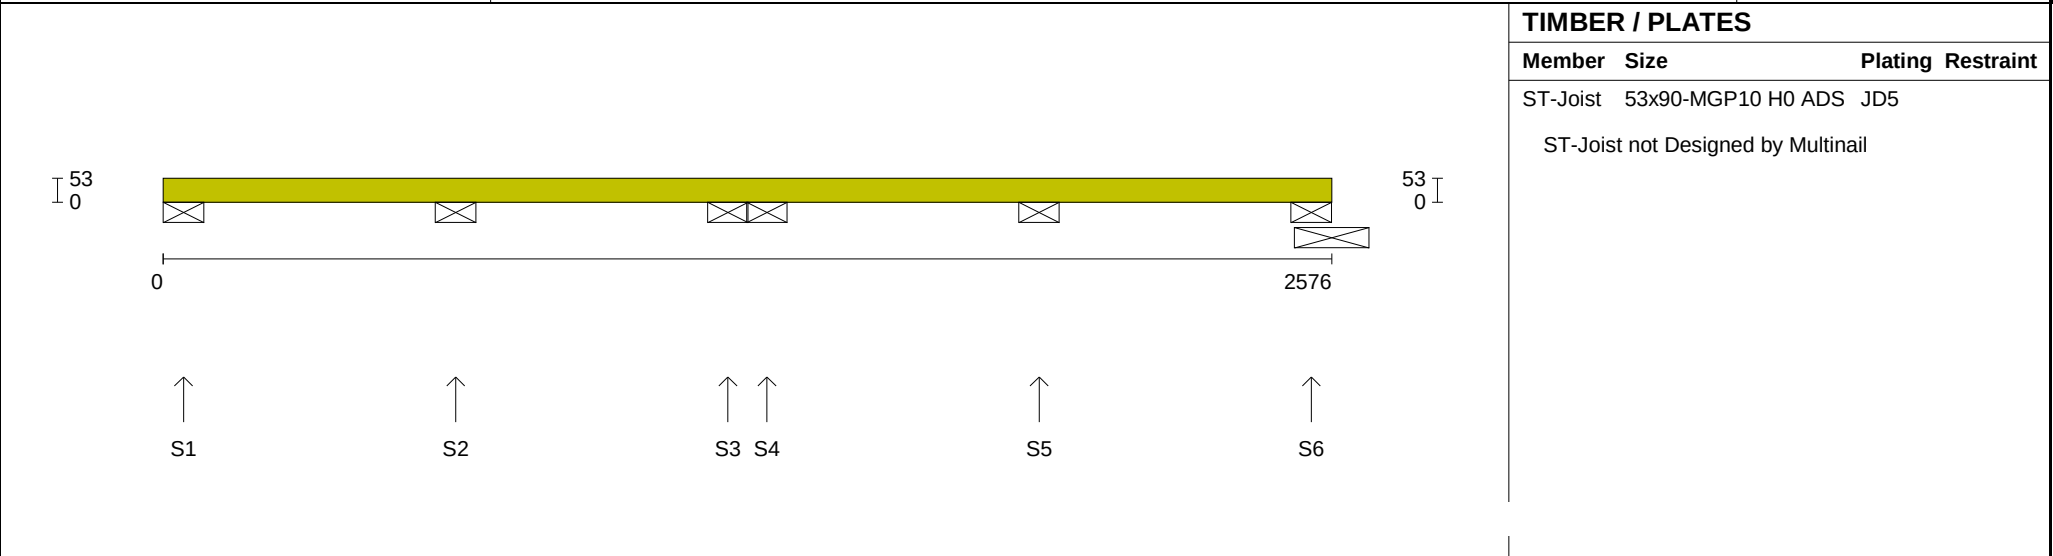

Vertical Reactions at Supports							Joint	Nail Plate
	S1	S2	S3	S4	S5	S6		
1.35DL (kN)	0.17	0.51	0.37	-0.07	0.14	0.05		
1.2DL + 1.5LL (kN)	0.39	1.16	0.65	0.25	0.83	0.28		

Span: 2576	Floor Material: Particle (13.9 kg/m²)	Application: General Areas	All dimensions in millimetres. This drawing should be read in conjunction with Multinail Technical sheets. Wall plates must be placed at supports only.	Joey Meriales (TN-012-015)
Overhang: 0/0	Floor Covering: Std Carpet + Underlay (8 kg/m²)	Live Load: 1.5 kPa		Ver: Floor 1.14.3
Spacing: 450	Ceiling Material: Plaster 10mm Std Core (6.7 kg/m²)	Point Load: 1.8 kN		Date: 10/04/2026
Quantity: 4	Ceiling Fixing: Direct fix @ 450c	Design: By Others		Page: 40 of 45

Client: BSPOKE LUXURY HOMES PTY LTD	BB Truss & Timber Pty Ltd 41 Keilor Park Drive, Keilor Park 3042	Job No: K0964
Site: LOT 735 15 LEICHHARDT AVE BURNSIDE VIC 3023 AUS		Weight: 6.14 kg
Ref:	Joist Name: SJ27 Type: 53x90-MGP10 H0 ADS Joists: SJ186, SJ187, SJ188, SJ189	Total Weight: 24.58 kg
		Laminations: 1

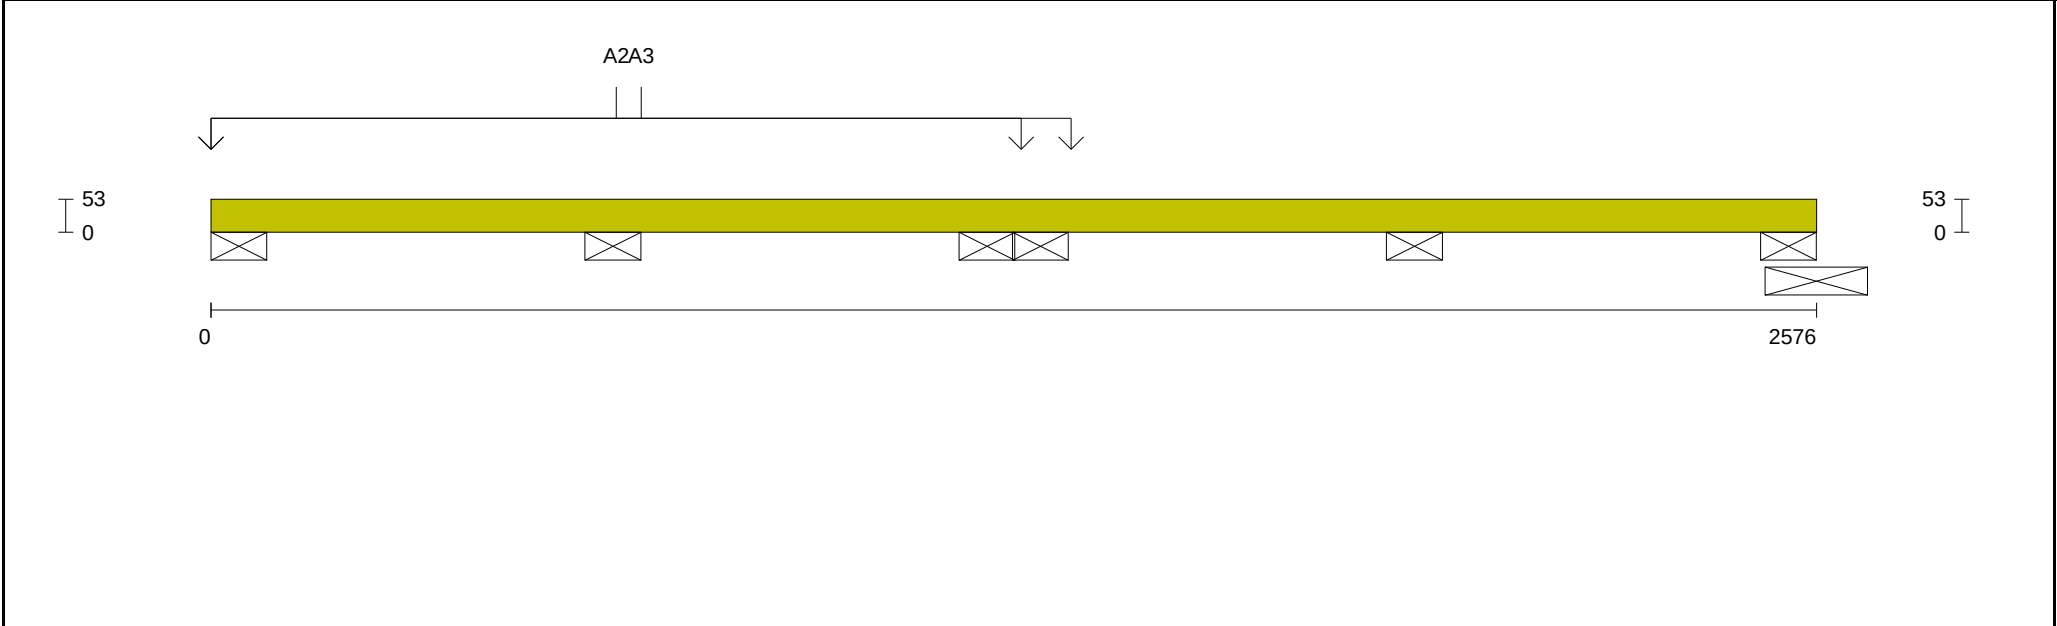


User Def. Load	A1	A2	A3
	50.00 kg/m²	80.00 kg/m²	8.70 kg/m²

Applied Load	
DL	(kN)
LL	(kN)
WL Up	(kN)
WL Dn	(kN)

Span:	2576	Floor Material:	Particle (13.9 kg/m³)	Application:	General Areas	All dimensions in millimetres. This drawing should be read in conjunction with Multinail Technical sheets. Wall plates must be placed at supports only.	Joey Meriales (TN-012-015)
Overhang:	0/0	Floor Covering:	Std Carpet + Underlay (8 kg/m³)	Live Load:	1.5 kPa		Ver: Floor 1.14.3
Spacing:	450	Ceiling Material:	Plaster 10mm Std Core (6.7 kg/m³)	Point Load:	1.8 kN		Date: 10/04/2026
Quantity:	4	Ceiling Fixing:	Direct fix @ 450c	Design:	By Others		Page: 41 of 45


Client: BSPOKE LUXURY HOMES PTY LTD	BB Truss & Timber Pty Ltd 41 Keilor Park Drive, Keilor Park 3042 Joist Name: SJ28 Type: 53x90-MGP10 H0 ADS Joists: SJ190, SJ191, SJ192, SJ193	Job No: K0964
Site: LOT 735 15 LEICHHARDT AVE BURNSIDE VIC 3023 AUS		Weight: 3.49 kg
Ref:		Total Weight: 13.98 kg
		Laminations: 1

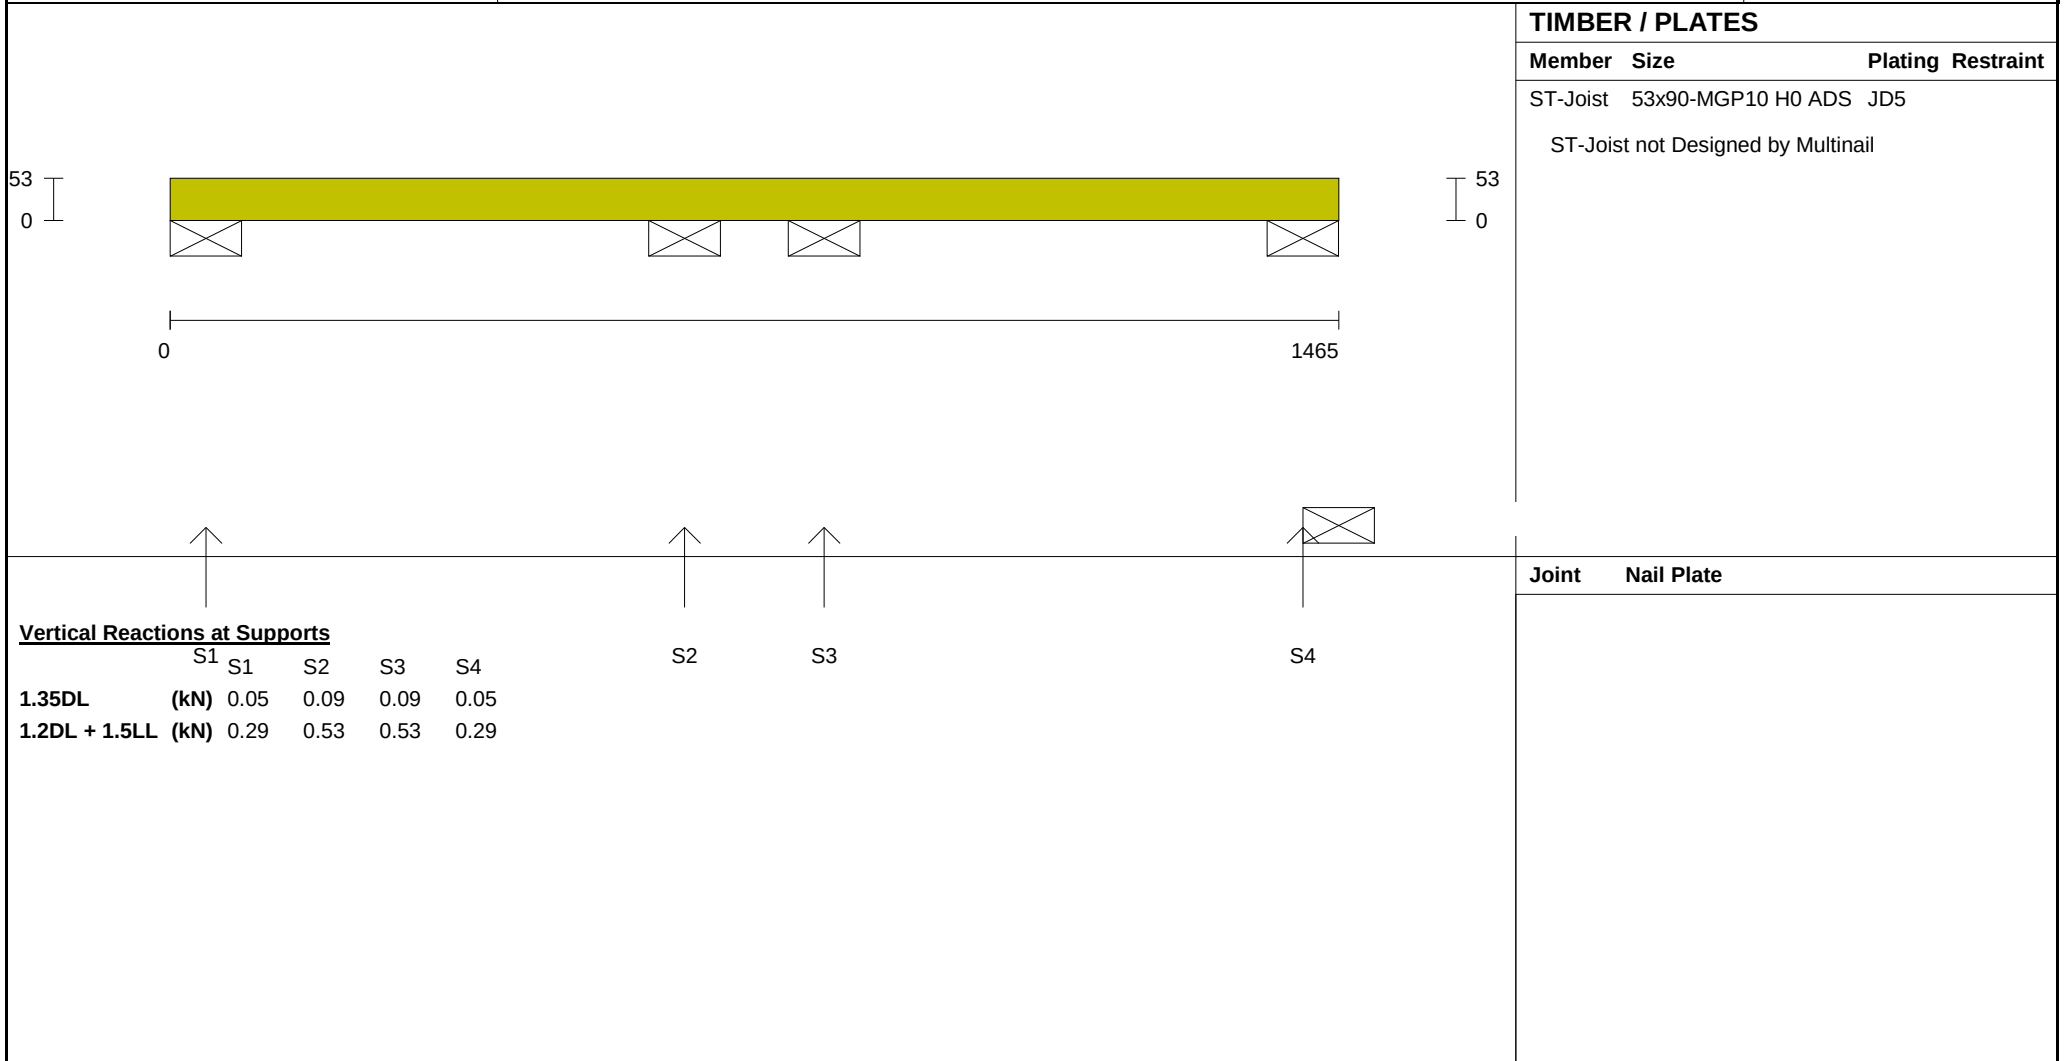

TIMBER / PLATES		
Member	Size	Plating Restraint
ST-Joist	53x90-MGP10 H0 ADS	JD5
ST-Joist not Designed by Multinail		
Joint	Nail Plate	

Span: 1465	Floor Material: Particle (13.9 kg/m²)	Application: General Areas	All dimensions in millimetres. This drawing should be read in conjunction with Multinail Technical sheets. Wall plates must be placed at supports only.	Joey Meriales (TN-012-015)
Overhang: 0/0	Floor Covering: Std Carpet + Underlay (8 kg/m²)	Live Load: 1.5 kPa		Ver: Floor 1.14.3
Spacing: 450	Ceiling Material: Plaster 10mm Std Core (6.7 kg/m²)	Point Load: 1.8 kN		Date: 10/04/2026
Quantity: 4	Ceiling Fixing: Direct fix @ 450c	Design: By Others		Page: 42 of 45

Client: BSPOKE LUXURY HOMES PTY LTD	BB Truss & Timber Pty Ltd 41 Keilor Park Drive, Keilor Park 3042	Job No: K0964
Site: LOT 735 15 LEICHHARDT AVE BURNSIDE VIC 3023 AUS		Weight: 3.49 kg
Ref:	Joist Name: SJ28 Type: 53x90-MGP10 H0 ADS Joists: SJ190, SJ191, SJ192, SJ193	Total Weight: 13.98 kg
		Laminations: 1

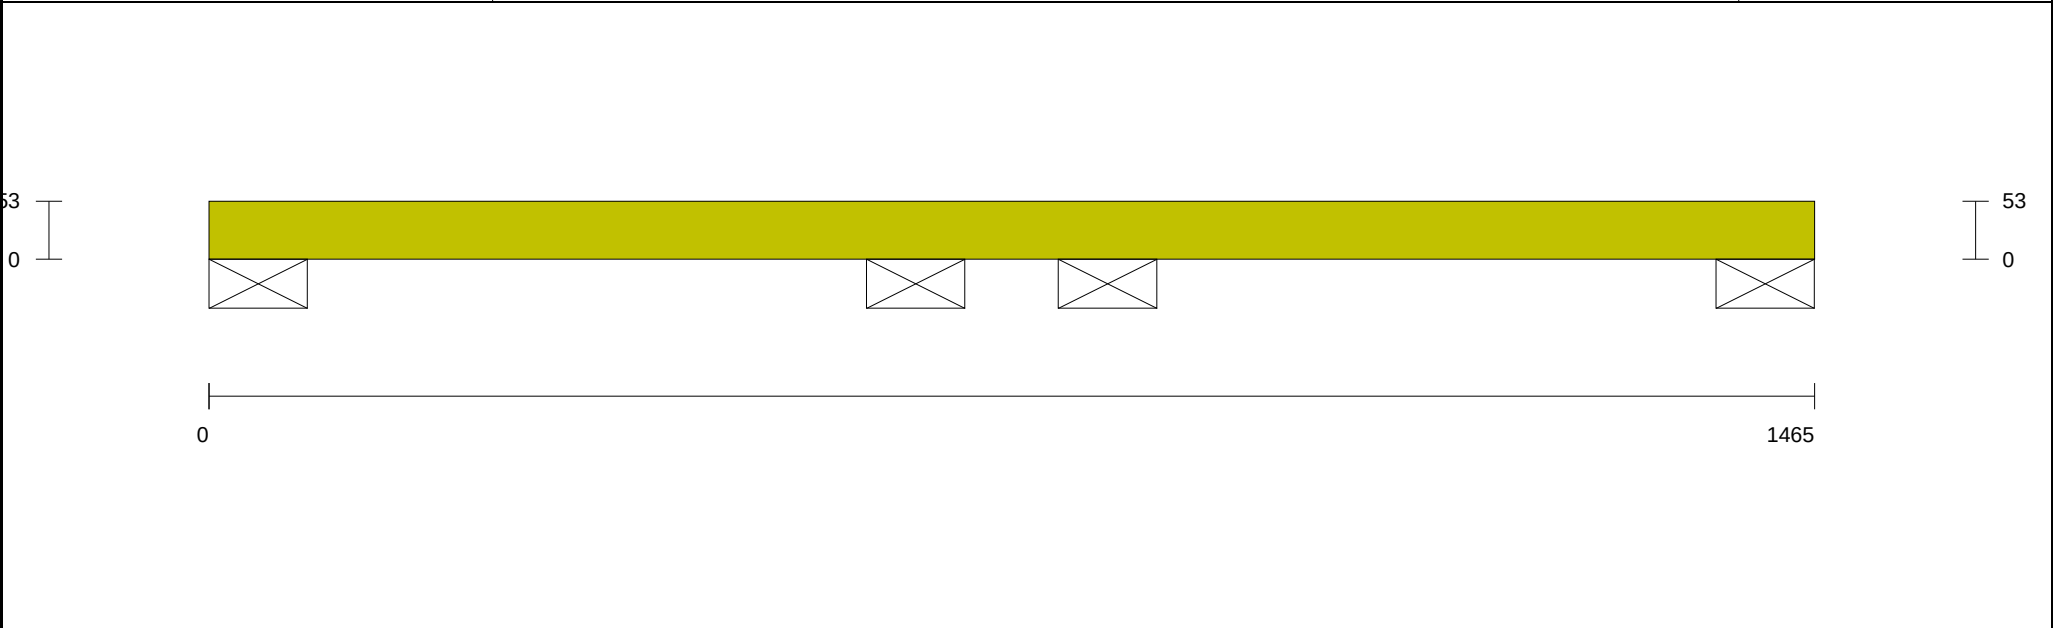


User Def. Load	A1 80.00 kg/m²	A2 50.00 kg/m²	
-----------------------	-------------------	-------------------	---

Applied Load	
DL (kN)	
LL (kN)	
WL Up (kN)	
WL Dn (kN)	

Span: 1465	Floor Material: Particle (13.9 kg/m²)	Application: General Areas	All dimensions in millimetres. This drawing should be read in conjunction with Multinail Technical sheets. Wall plates must be placed at supports only.	Joey Meriales (TN-012-015)
Overhang: 0/0	Floor Covering: Std Carpet + Underlay (8 kg/m²)	Live Load: 1.5 kPa		Ver: Floor 1.14.3
Spacing: 450	Ceiling Material: Plaster 10mm Std Core (6.7 kg/m²)	Point Load: 1.8 kN		Date: 10/04/2026
Quantity: 4	Ceiling Fixing: Direct fix @ 450c	Design: By Others		Page: 43 of 45

Client: BSPOKE LUXURY HOMES PTY LTD	BB Truss & Timber Pty Ltd 41 Keilor Park Drive, Keilor Park 3042	Job No: K0964
Site: LOT 735 15 LEICHHARDT AVE BURNSIDE VIC 3023 AUS		Weight: 3.10 kg
Ref:	Joist Name: SJ29 Type: 53x90-MGP10 H0 ADS Joists: SJ194, SJ195, SJ196, SJ197	Total Weight: 12.40 kg
		Laminations: 1

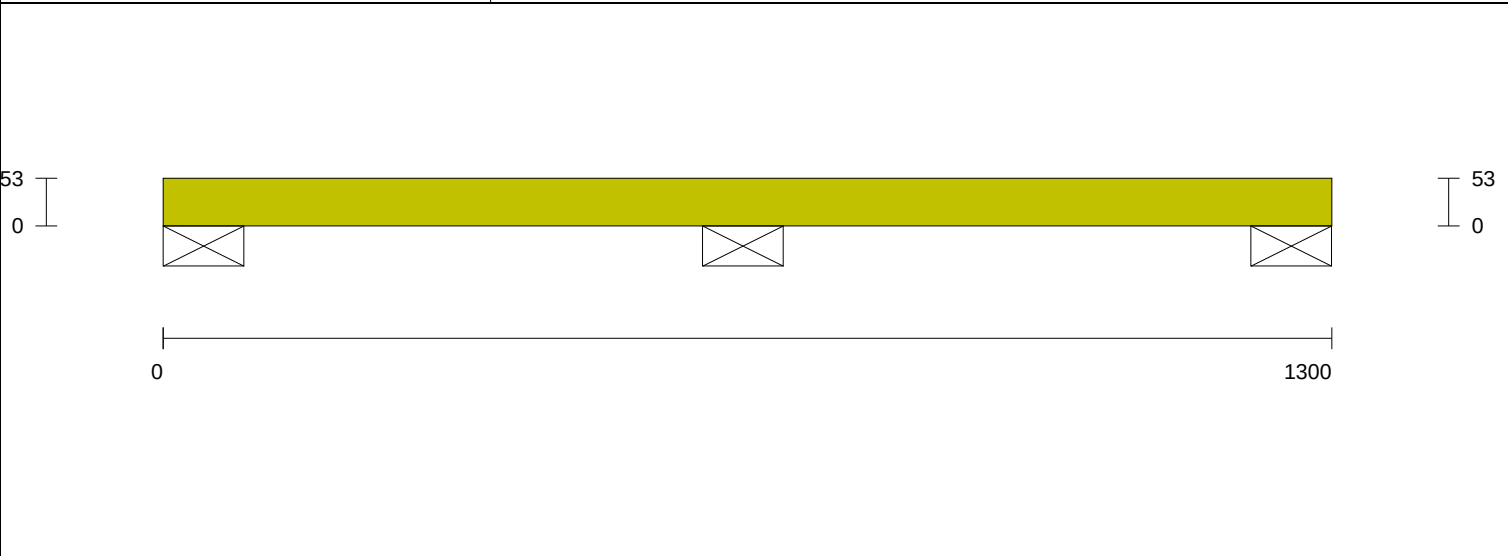


TIMBER / PLATES			
Member	Size	Plating	Restraint
ST-Joist	53x90-MGP10 H0 ADS	JD5	
ST-Joist not Designed by Multinail			

Vertical Reactions at Supports			
	S1	S2	S3
1.35DL (kN)	0.13	0.51	0.16
1.2DL + 1.5LL (kN)	0.34	1.22	0.37

Joint	Nail Plate

Span: 1300	Floor Material: Particle (13.9 kg/m²)	Application: General Areas	All dimensions in millimetres. This drawing should be read in conjunction with Multinail Technical sheets. Wall plates must be placed at supports only.	Joey Meriales (TN-012-015)
Overhang: 0/0	Floor Covering: Std Carpet + Underlay (8 kg/m²)	Live Load: 1.5 kPa		Ver: Floor 1.14.3
Spacing: 450	Ceiling Material: Plaster 10mm Std Core (6.7 kg/m²)	Point Load: 1.8 kN		Date: 10/04/2026
Quantity: 4	Ceiling Fixing: Direct fix @ 450c	Design: By Others		Page: 44 of 45

Client: BSPOKE LUXURY HOMES PTY LTD	BB Truss & Timber Pty Ltd 41 Keilor Park Drive, Keilor Park 3042 A1 Joist Name: SJ29 Type: 53x90-MGP10 H0 ADS Joists: SJ194, SJ195, SJ196, SJ197	Job No: K0964
Site: LOT 735 15 LEICHHARDT AVE BURNSIDE VIC 3023 AUS		Weight: 3.10 kg
Ref:		Total Weight: 12.40 kg
		Laminations: 1

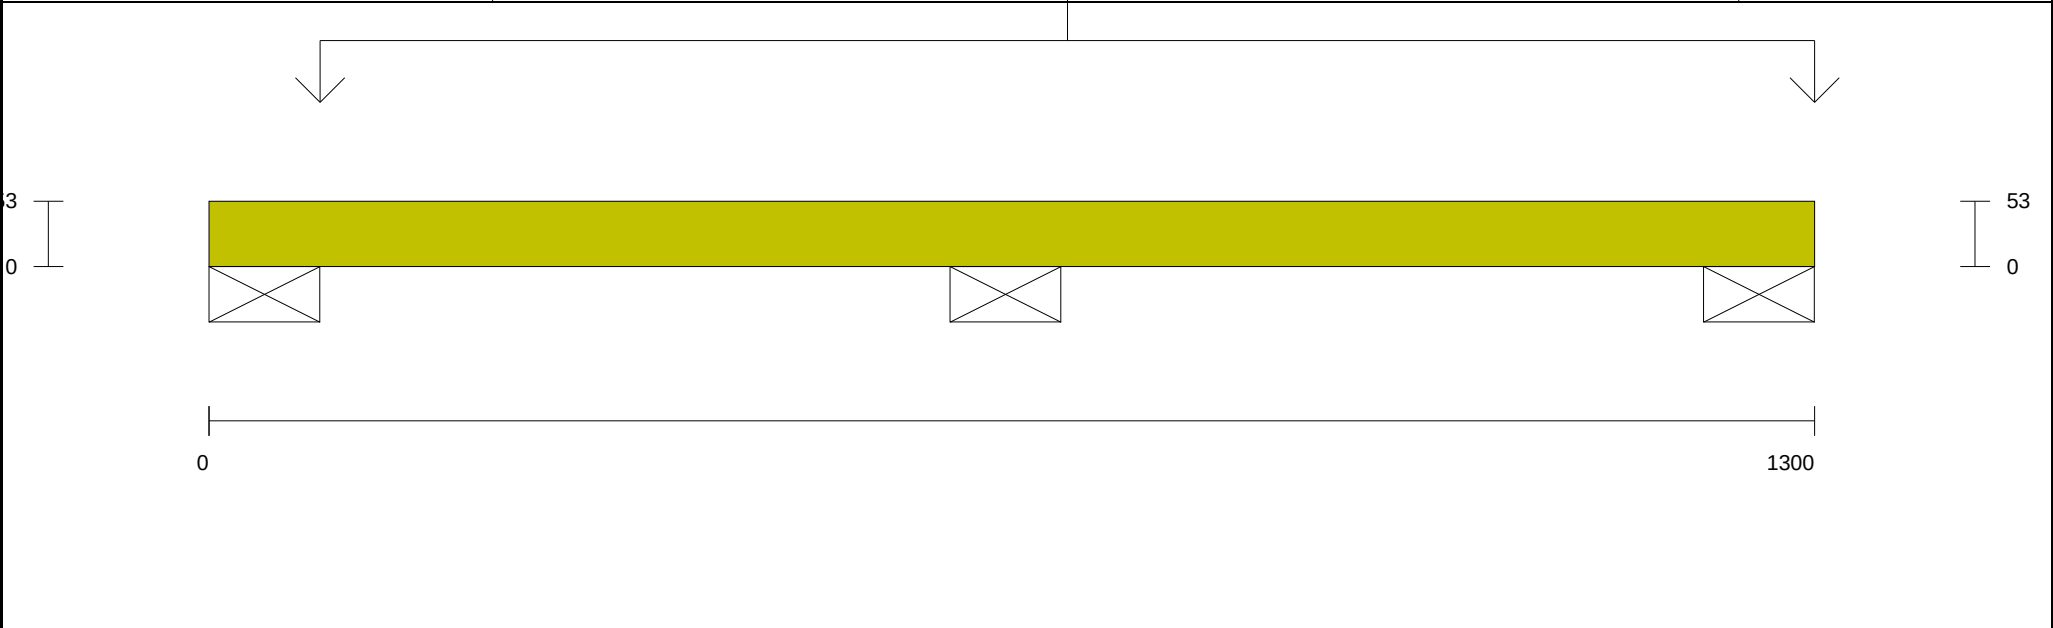


User Def. Load	A1	A2
	80.00 kg/m²	50.00 kg/m²

Applied Load		
DL	(kN)	
LL	(kN)	
WL Up	(kN)	
WL Dn	(kN)	

Span:	1300	Floor Material:	Particle (13.9 kg/m³)	Application:	General Areas	All dimensions in millimetres. This drawing should be read in conjunction with Multinail Technical sheets. Wall plates must be placed at supports only.	Joey Meriales (TN-012-015)
Overhang:	0/0	Floor Covering:	Std Carpet + Underlay (8 kg/m³)	Live Load:	1.5 kPa		Ver: Floor 1.14.3
Spacing:	450	Ceiling Material:	Plaster 10mm Std Core (6.7 kg/m³)	Point Load:	1.8 kN		Date: 10/04/2026
Quantity:	4	Ceiling Fixing:	Direct fix @ 450c	Design:	By Others		Page: 45 of 45




BALLARAT: 5333 1100

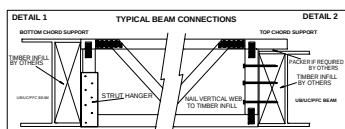

Trusses to be erected in accordance with Australian Standard AS4440 -1997
Trusses are not to be cut, modified or altered without prior authorisation

NOTE 1 : All beams by others to engineers comps.
NOTE 2 : Flooring to be fixed as per manufacturers specs
NOTE 3 : All steel beams to have infill as per detail 1 & 2
NOTE 4 : Bearers to fully support all loadbearing walls by others

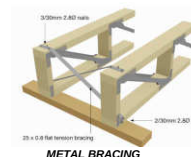

SPECIFICATIONS: MS 413's		Joist Type: MultiStrut - 413/360mm High	Spacing: 450	BSPOKE LUXURY HOMES PTY LTD LOT 735 15 LEICHHARDT AVE BURNSIDE VIC 3023 AUS 	Detailer: JOEY
Structure: House	Flooring: Particle	Dist. Live Load: 1.50			Date: 3/04/2026
Floor Appl: General Areas	Flooring Size: 3600x900x19	Concat. Point Load: 1.80			Scale: 1 : 100
Wind Speed: N2	Ceiling: Plaster 10mm Std Core	Timber Dry Timber			Job No: K0964